



SETTING-OUT POINTS (mm, from datum)

- A x=0 y=0 datum, front-left internal corner
- B x=2400 y=0 front-right corner
- C x=2400 y=3106 rear-right corner
- D x=0 y=3106 rear-left corner
- E x=450 y=0 left column inner face
- F x=1950 y=0 right column inner face
- G x=454 y=0 fixed glass
- H x=946 y=0 door leaf
- J x=250 y=- left unit face line
- K x=2150 y=- right unit face line

Glass joints 4 mm (glazier to confirm).

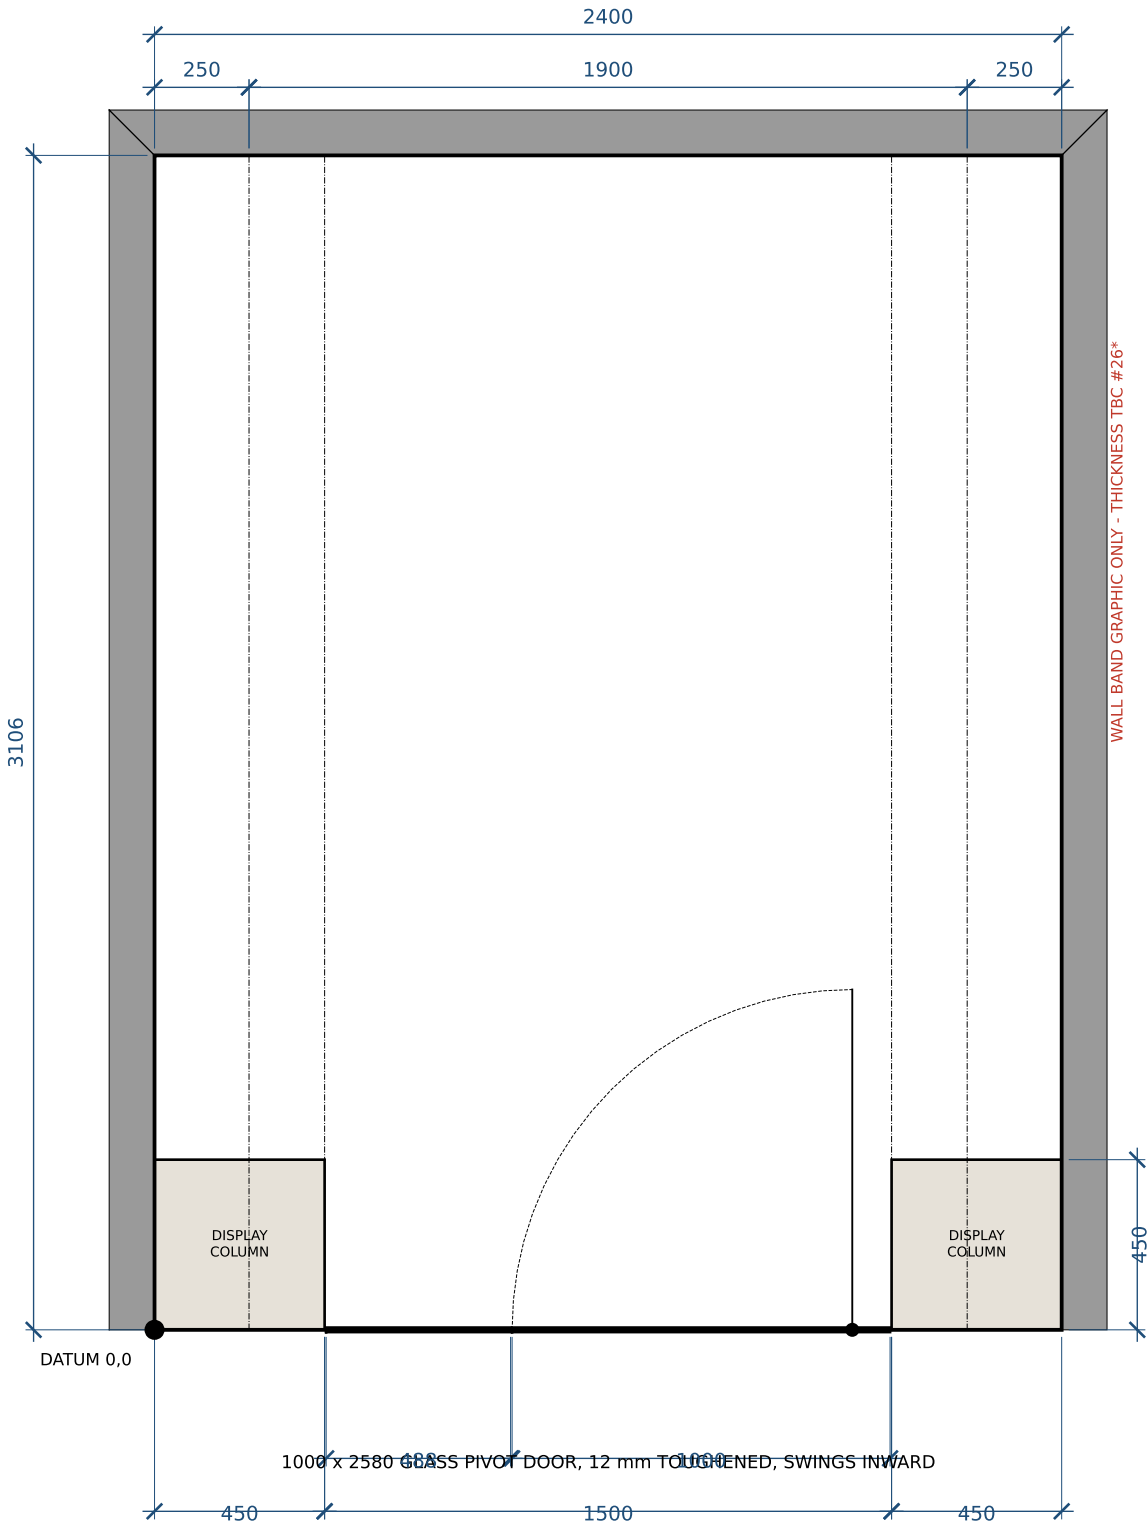

Site / consultant items still open: #4 finished size, #16 MEP/fire, #23 north, #26 datum + wall thickness. Verify before fabrication.

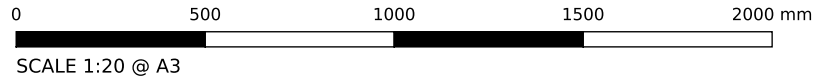

BORN FRAGRANCE

PROJECT BORN FRAGRANCE - shop fit-out

SHEET SD-01

TITLE SETTING-OUT PLAN

SCALE 1:20 @ A3

DATE 2026-10-05

REV A - owner-approved TBC answers

SPEC spec/SHOP_SPEC.json @ fb5eebb


DRAWN Claude Code (AI), for owner review

TBC ITEMS ON THIS SHEET

- #4 Is 2400 x 3106 the finished size (after plaster)?
- #16 Fixings, MEP, fire and escape requirements
- #23* North direction
- #26* Vertical datum (FFL) and wall thickness / construction
- * proposed item, not yet in spec/TBC.md
- TBC items are shown in revision clouds.
- Dimensions computed from SHOP_SPEC.json.
- Do not scale from the render.
- FOR COORDINATION - SITE ITEMS OPEN

LEGEND


Side runs 4 bays, 25x25 + 20x20 MS SHS, black PPC, 250 deep
Rear unit zones 500 + 900 + 500 (centre = logo)
Base cabinets 600 H incl. 100x50 recessed plinth
Cabinet doors: 1.5 mm powder-coated steel, light neutral, flush handleless
Storefront columns 450x450, shelves face street
Counter x 700-1700, rear edge y 2156
No timber, brass, plants or loose products.

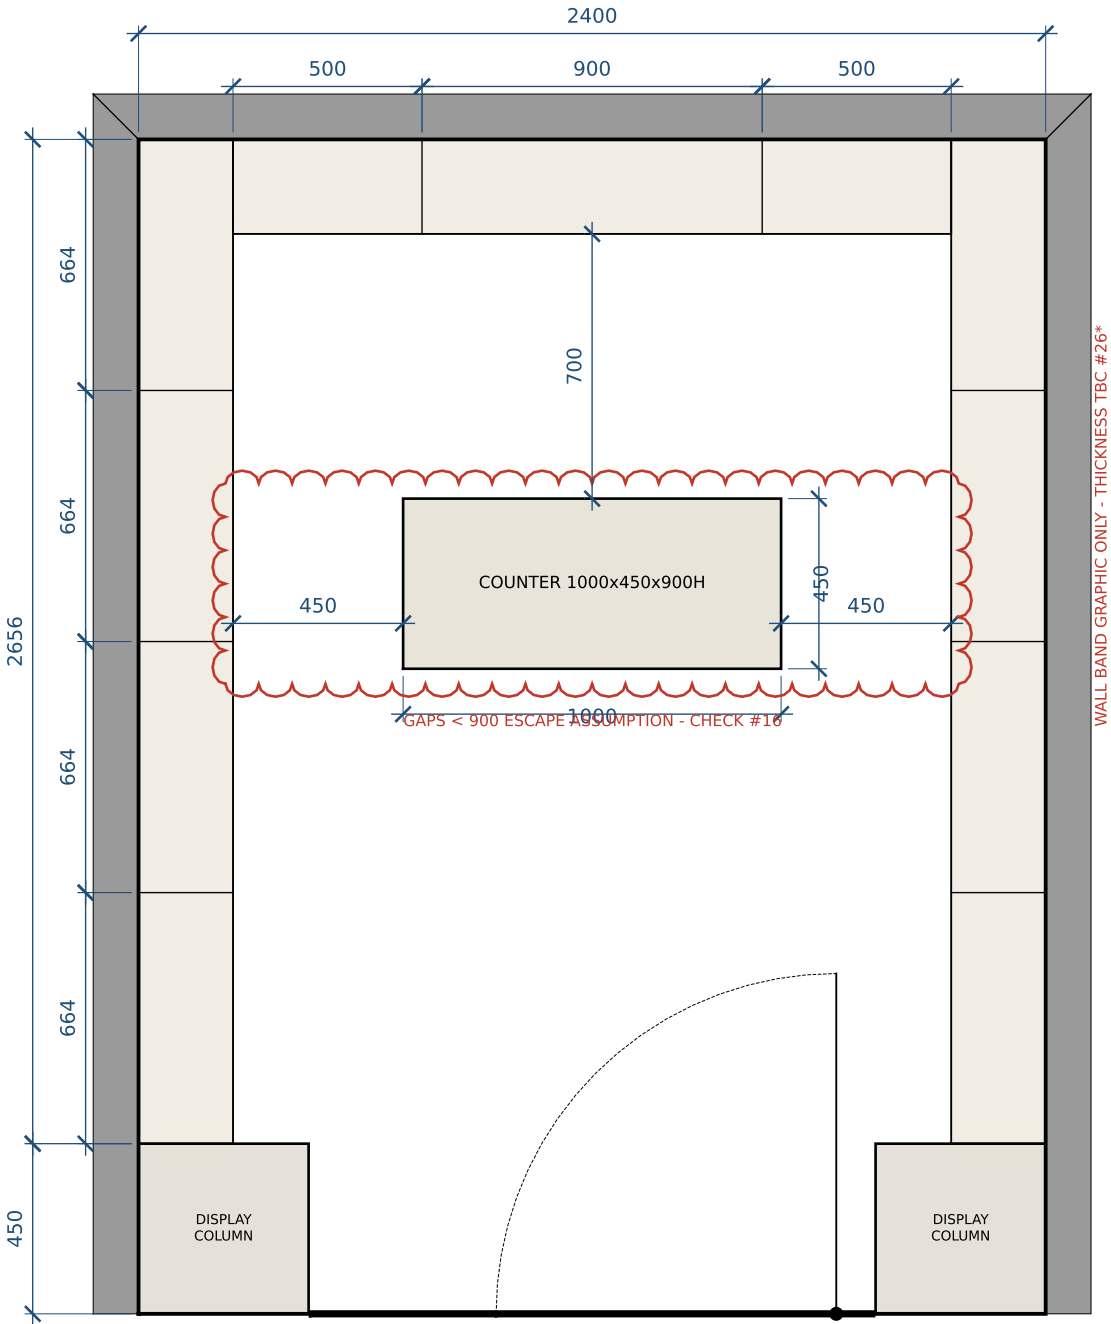

WALL BAND GRAPHIC ONLY - THICKNESS TBC #26*

1000 x 2580 GLASS PIVOT DOOR, 12 mm TOUGHENED, SWINGS INWARD

Site / consultant items still open: #4 finished size, #16 MEP/fire, #23 north, #26 datum + wall thickness. Verify before fabrication.

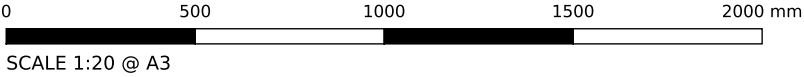

BORN FRAGRANCE

PROJECT BORN FRAGRANCE - shop fit-out

SHEET SD-02

TITLE DISPLAY / FURNITURE PLAN

SCALE 1:20 @ A3

DATE 2026-10-05

REV A - owner-approved TBC answers

SPEC spec/SHOP_SPEC.json @ fb5eebb

DRAWN Claude Code (AI), for owner review

TBC ITEMS ON THIS SHEET


#4 Is 2400 x 3106 the finished size (after plaster)?
#16 Fixings, MEP, fire and escape requirements
#23* North direction
#26* Vertical datum (FFL) and wall thickness / construction

* proposed item, not yet in spec/TBC.md
TBC items are shown in revision clouds.
Dimensions computed from SHOP_SPEC.json.
Do not scale from the render.


FOR COORDINATION - SITE ITEMS OPEN

FLOOR: 1200x600 RECTIFIED STONE-LOOK PORCELAIN

Option A: 1200 across the width, 600 along the depth.
Across: 0 full + 2 x 1194 cut. Depth: 4 full + 2 x 343 cut.
Grout 2 mm between tiles; 5 mm perimeter movement joint.
Tiles run under all units and the counter (full 2400 x 3106).
Threshold flush, no level change (#20). Set out from the centre line.

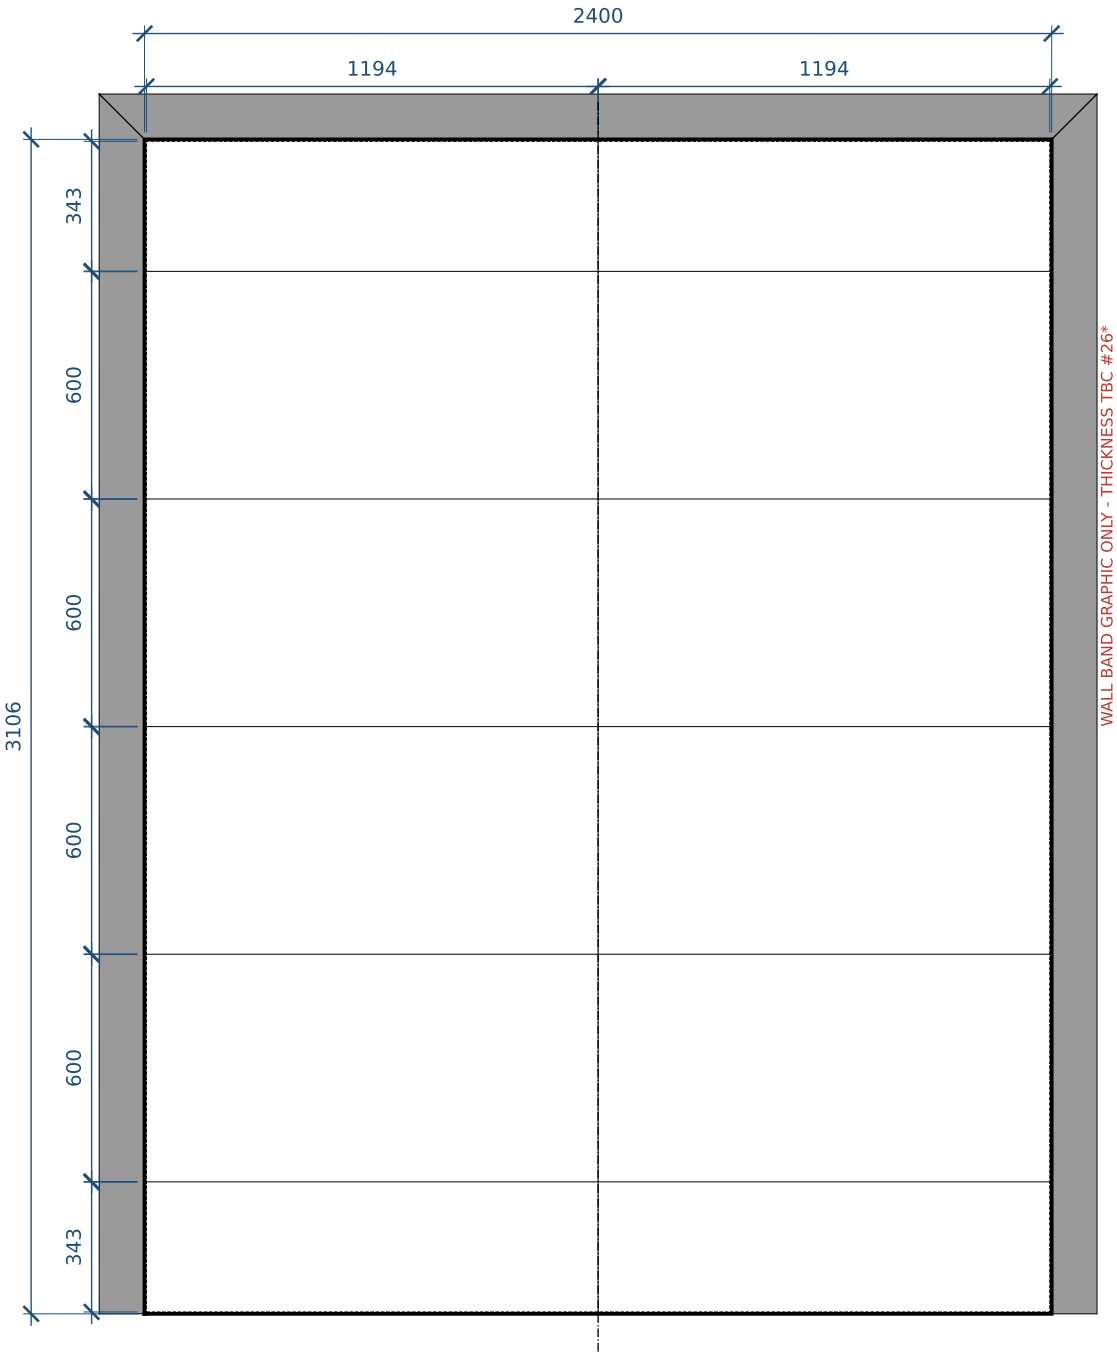

Site / consultant items still open: #4 finished size, #16 MEP/fire, #23 north, #26 datum + wall thickness. Verify before fabrication.

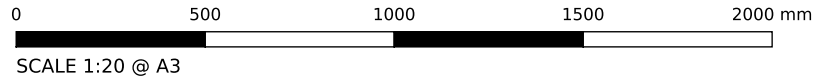

BORN FRAGRANCE

PROJECT BORN FRAGRANCE - shop fit-out

SHEET SD-03

TITLE FLOOR FINISH PLAN

SCALE 1:20 @ A3

DATE 2026-10-05

REV A - owner-approved TBC answers

SPEC spec/SHOP_SPEC.json @ fb5eebb

DRAWN Claude Code (AI), for owner review

TBC ITEMS ON THIS SHEET


#4 Is 2400 x 3106 the finished size (after plaster)?
#16 Fixings, MEP, fire and escape requirements
#23* North direction
#26* Vertical datum (FFL) and wall thickness / construction

* proposed item, not yet in spec/TBC.md
TBC items are shown in revision clouds.
Dimensions computed from SHOP_SPEC.json.
Do not scale from the render.
FOR COORDINATION - SITE ITEMS OPEN


LIGHTING LEGEND (3000K)

- Black track, 2 no., 2206 long
- Black cylindrical spot, 4 per track
- Recessed downlight, 3 no.
- Concealed LED under shelves + toe-kick LED

No pendants or decorative ceiling features.

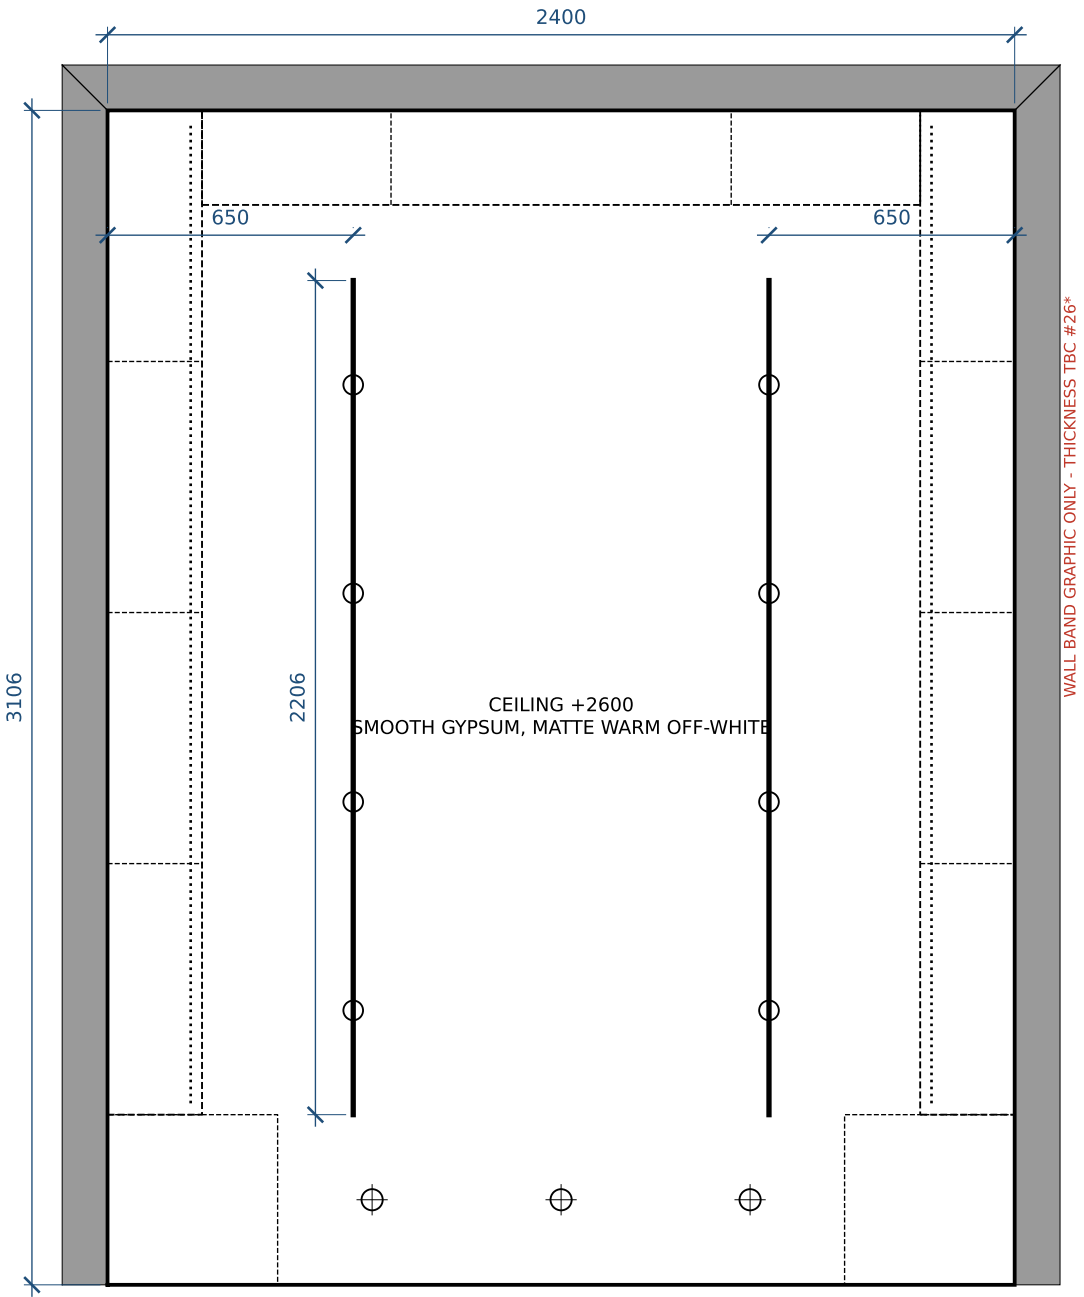

Site / consultant items still open: #4 finished size, #16 MEP/fire, #23 north, #26 datum + wall thickness. Verify before fabrication.

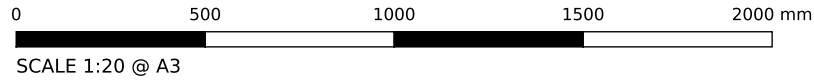

BORN FRAGRANCE

PROJECT BORN FRAGRANCE - shop fit-out

SHEET SD-04

TITLE REFLECTED CEILING PLAN

SCALE 1:20 @ A3

DATE 2026-10-05

REV A - owner-approved TBC answers

SPEC spec/SHOP_SPEC.json @ fb5eebb

DRAWN Claude Code (AI), for owner review


TBC ITEMS ON THIS SHEET

#4 Is 2400 x 3106 the finished size (after plaster)?
#16 Fixings, MEP, fire and escape requirements
#23* North direction
#26* Vertical datum (FFL) and wall thickness / construction
* proposed item, not yet in spec/TBC.md
TBC items are shown in revision clouds.
Dimensions computed from SHOP_SPEC.json.
Do not scale from the render.
FOR COORDINATION - SITE ITEMS OPEN


MATERIALS (LOCKED)

M1 Raw textured light plaster
M2 25x25x1.6 / 20x20x1.6 MS SHS, matte black PPC
M3 ~20x40 diamond expanded mesh, black
M4 1200x600 stone-look porcelain floor
L1 Concealed 3000 K LED under shelves
Heights not listed are TBC - never scaled.

BLACK HALO-LIT LOGO ON 25 mm STAND-OFFS

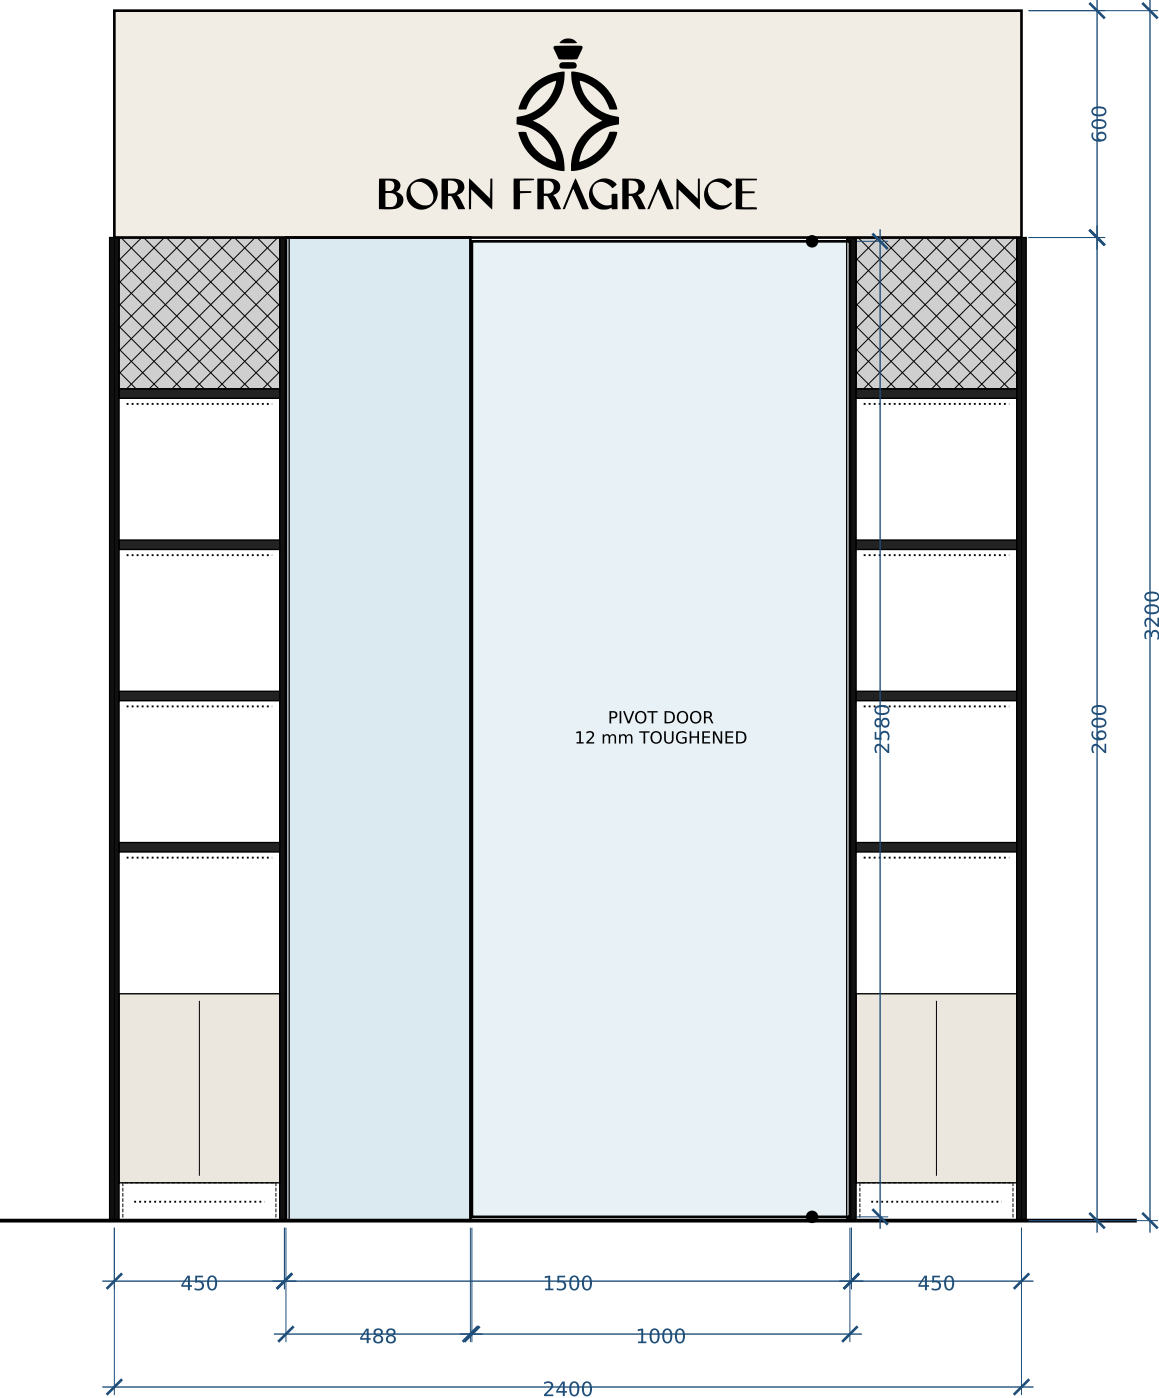

Site / consultant items still open: #4 finished size, #16 MEP/fire, #23 north, #26 datum + wall thickness. Verify before fabrication.

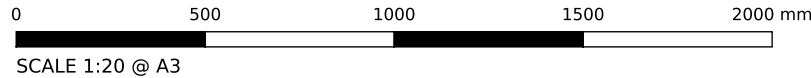

BORN FRAGRANCE

PROJECT BORN FRAGRANCE - shop fit-out

SHEET SD-05

TITLE STOREFRONT ELEVATION (EXTERNAL)

SCALE 1:20 @ A3

DATE 2026-10-05

REV A - owner-approved TBC answers

SPEC spec/SHOP_SPEC.json @ fb5eebb


DRAWN Claude Code (AI), for owner review

TBC ITEMS ON THIS SHEET


#4 Is 2400 x 3106 the finished size (after plaster)?
#16 Fixings, MEP, fire and escape requirements
#23* North direction
#26* Vertical datum (FFL) and wall thickness / construction
#16 Fixings, MEP, fire and escape requirements
* proposed item, not yet in spec/TBC.md
TBC items are shown in revision clouds.
Dimensions computed from SHOP_SPEC.json.
Do not scale from the render.
FOR COORDINATION - SITE ITEMS OPEN

MATERIALS (LOCKED)

M1 Raw textured light plaster
M2 25x25x1.6 / 20x20x1.6 MS SHS, matte black PPC
M3 ~20x40 diamond expanded mesh, black
M4 1200x600 stone-look porcelain floor
L1 Concealed 3000 K LED under shelves
Heights not listed are TBC - never scaled.

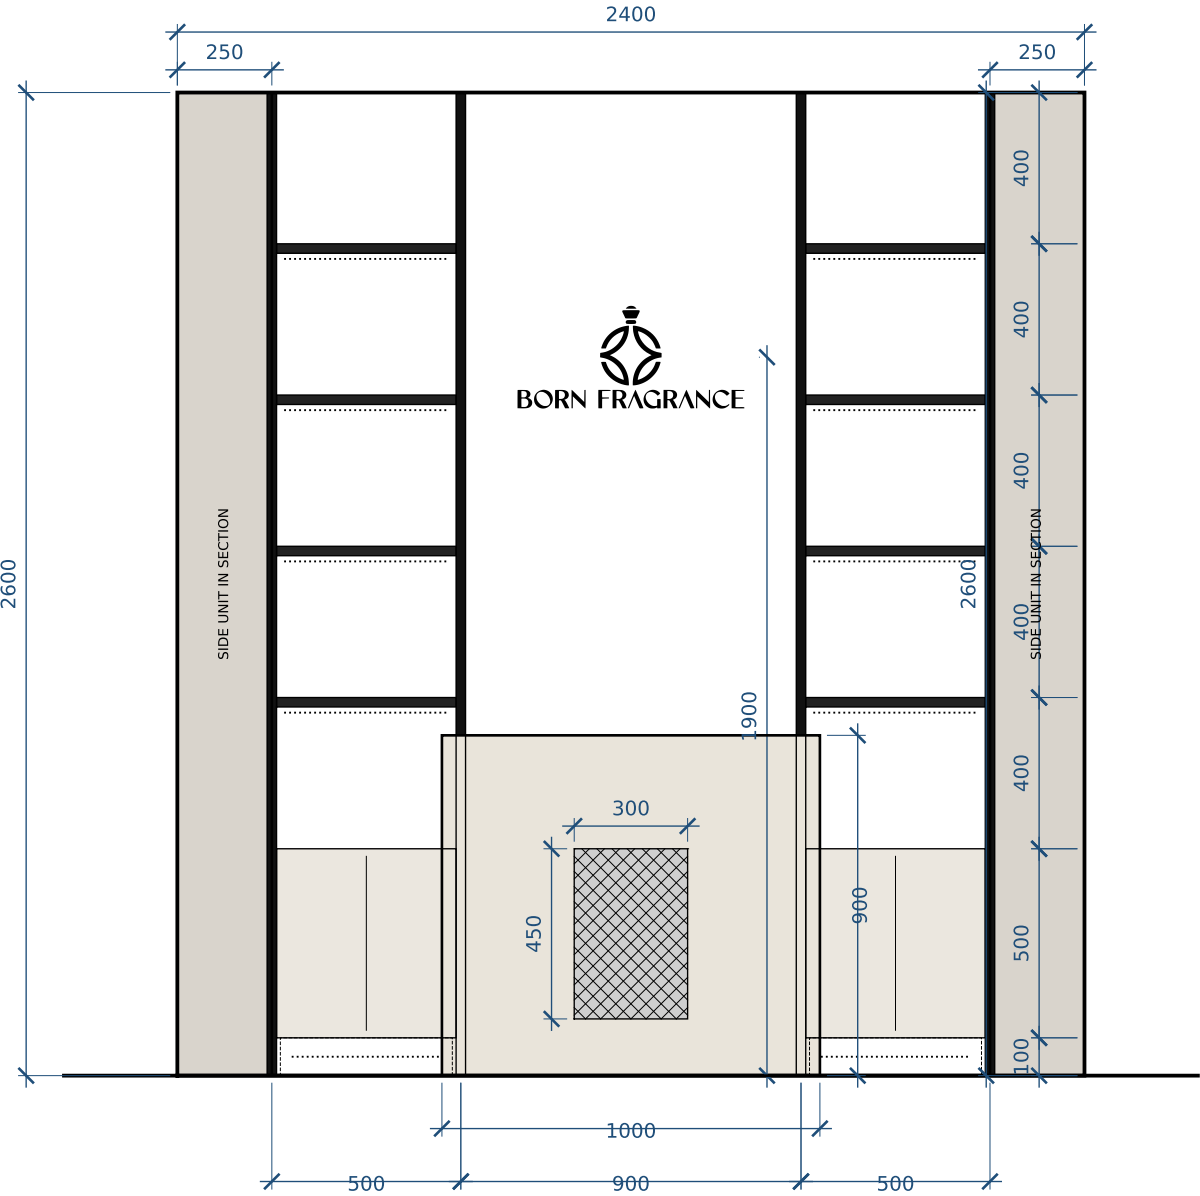

Site / consultant items still open: #4 finished size, #16 MEP/fire, #23 north, #26 datum + wall thickness. Verify before fabrication.

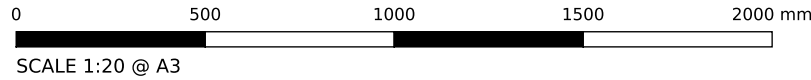

BORN FRAGRANCE

PROJECT BORN FRAGRANCE - shop fit-out

SHEET SD-06

TITLE REAR ELEVATION (INTERNAL)

SCALE 1:20 @ A3

DATE 2026-10-05

REV A - owner-approved TBC answers

SPEC spec/SHOP_SPEC.json @ fb5eebb

DRAWN Claude Code (AI), for owner review

TBC ITEMS ON THIS SHEET

#4 Is 2400 x 3106 the finished size (after plaster)?
#16 Fixings, MEP, fire and escape requirements
#23* North direction
#26* Vertical datum (FFL) and wall thickness / construction

* proposed item, not yet in spec/TBC.md
TBC items are shown in revision clouds.
Dimensions computed from SHOP_SPEC.json.
Do not scale from the render.
FOR COORDINATION - SITE ITEMS OPEN

MATERIALS (LOCKED)

M1 Raw textured light plaster
M2 25x25x1.6 / 20x20x1.6 MS SHS, matte black PPC
M3 ~20x40 diamond expanded mesh, black
M4 1200x600 stone-look porcelain floor
L1 Concealed 3000 K LED under shelves
Heights not listed are TBC - never scaled.



BORN FRAGRANCE

PROJECT BORN FRAGRANCE - shop fit-out

SHEET SD-07

TITLE LEFT ELEVATION (INTERNAL)

SCALE 1:20 @ A3

DATE 2026-10-05

REV A - owner-approved TBC answers


SPEC spec/SHOP_SPEC.json @ fb5eebb

DRAWN Claude Code (AI), for owner review


TBC ITEMS ON THIS SHEET

#4 Is 2400 x 3106 the finished size (after plaster)?
#16 Fixings, MEP, fire and escape requirements
#23* North direction
#26* Vertical datum (FFL) and wall thickness / construction

* proposed item, not yet in spec/TBC.md
TBC items are shown in revision clouds.
Dimensions computed from SHOP_SPEC.json.
Do not scale from the render.
FOR COORDINATION - SITE ITEMS OPEN

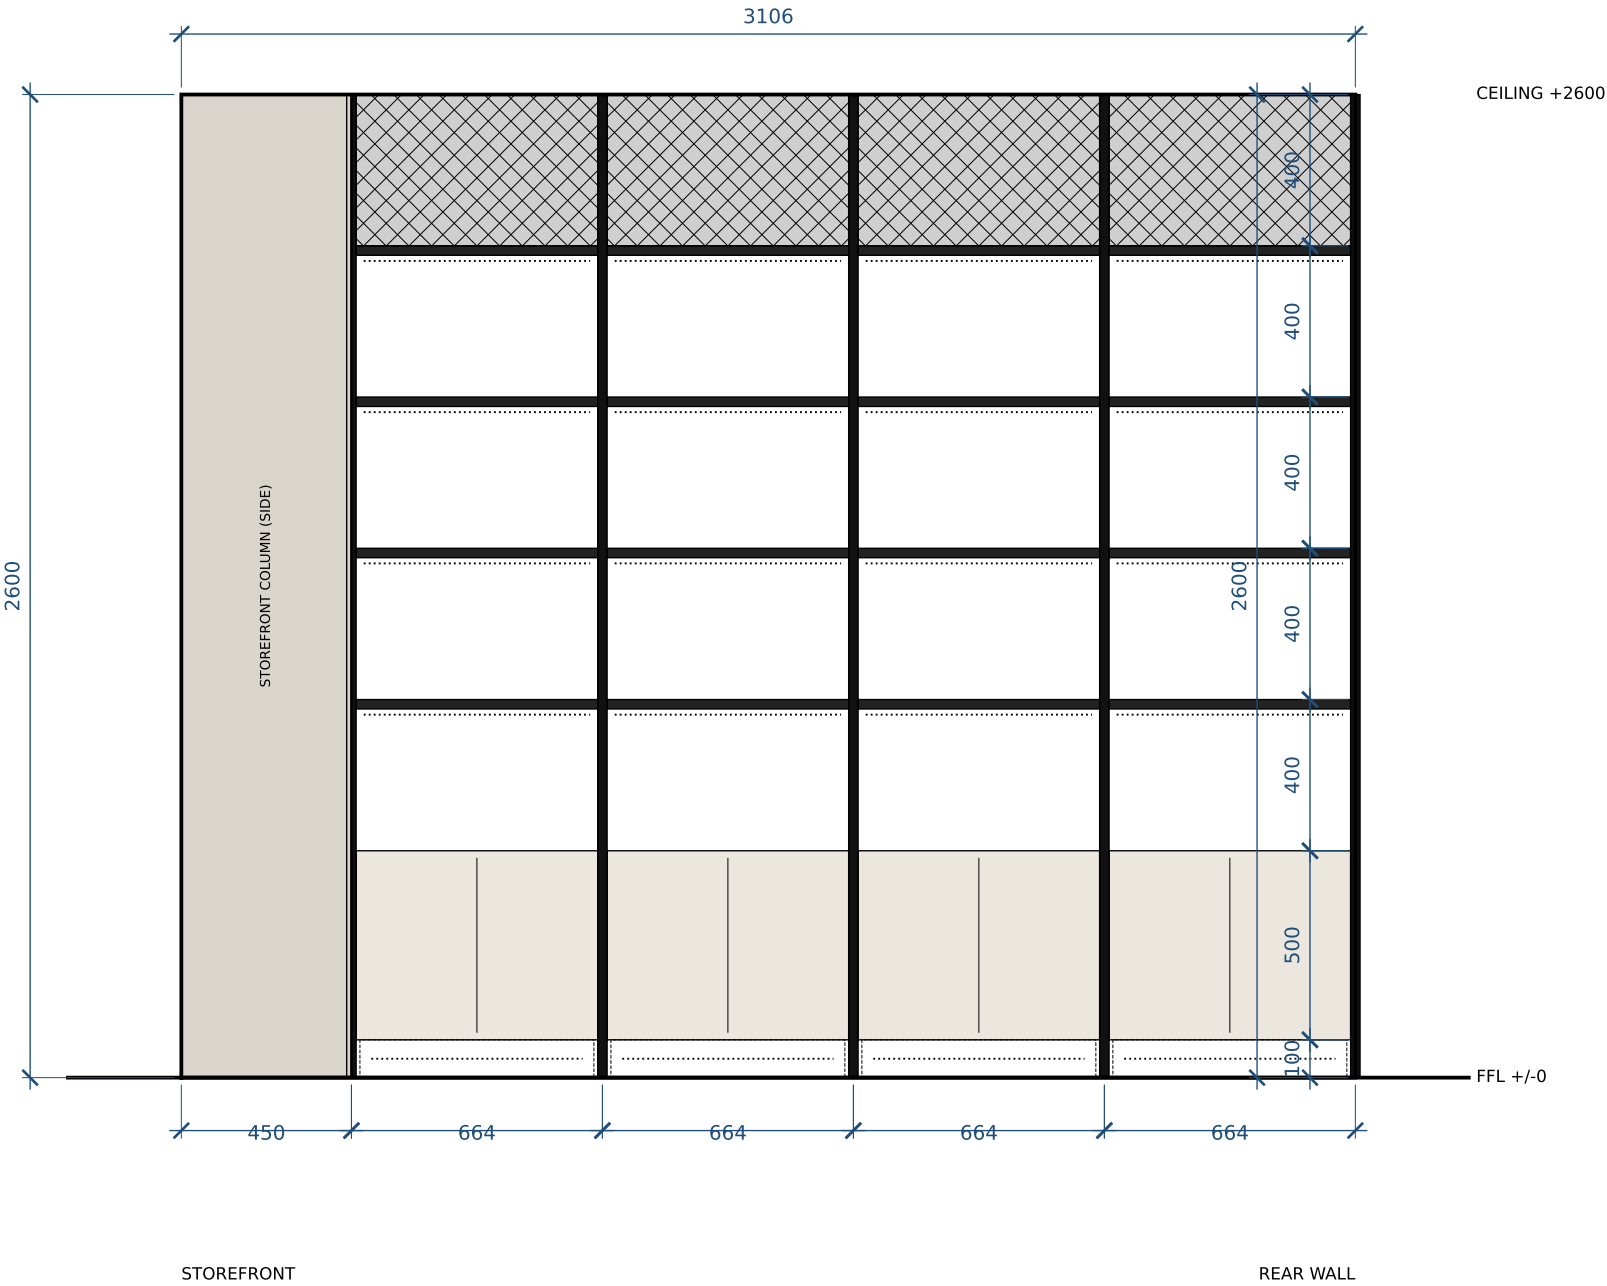

Site / consultant items still open: #4 finished size, #16 MEP/fire, #23 north, #26 datum + wall thickness. Verify before fabrication.

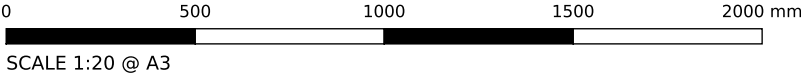

MATERIALS (LOCKED)

M1 Raw textured light plaster
M2 25x25x1.6 / 20x20x1.6 MS SHS, matte black PPC
M3 ~20x40 diamond expanded mesh, black
M4 1200x600 stone-look porcelain floor
L1 Concealed 3000 K LED under shelves
Heights not listed are TBC - never scaled.



BORN FRAGRANCE

PROJECT BORN FRAGRANCE - shop fit-out

SHEET SD-08

TITLE RIGHT ELEVATION (INTERNAL)

SCALE 1:20 @ A3

DATE 2026-10-05

REV A - owner-approved TBC answers


SPEC spec/SHOP_SPEC.json @ fb5eebb

DRAWN Claude Code (AI), for owner review

TBC ITEMS ON THIS SHEET

#4 Is 2400 x 3106 the finished size (after plaster)?
#16 Fixings, MEP, fire and escape requirements
#23* North direction
#26* Vertical datum (FFL) and wall thickness / construction

* proposed item, not yet in spec/TBC.md
TBC items are shown in revision clouds.
Dimensions computed from SHOP_SPEC.json.
Do not scale from the render.
FOR COORDINATION - SITE ITEMS OPEN

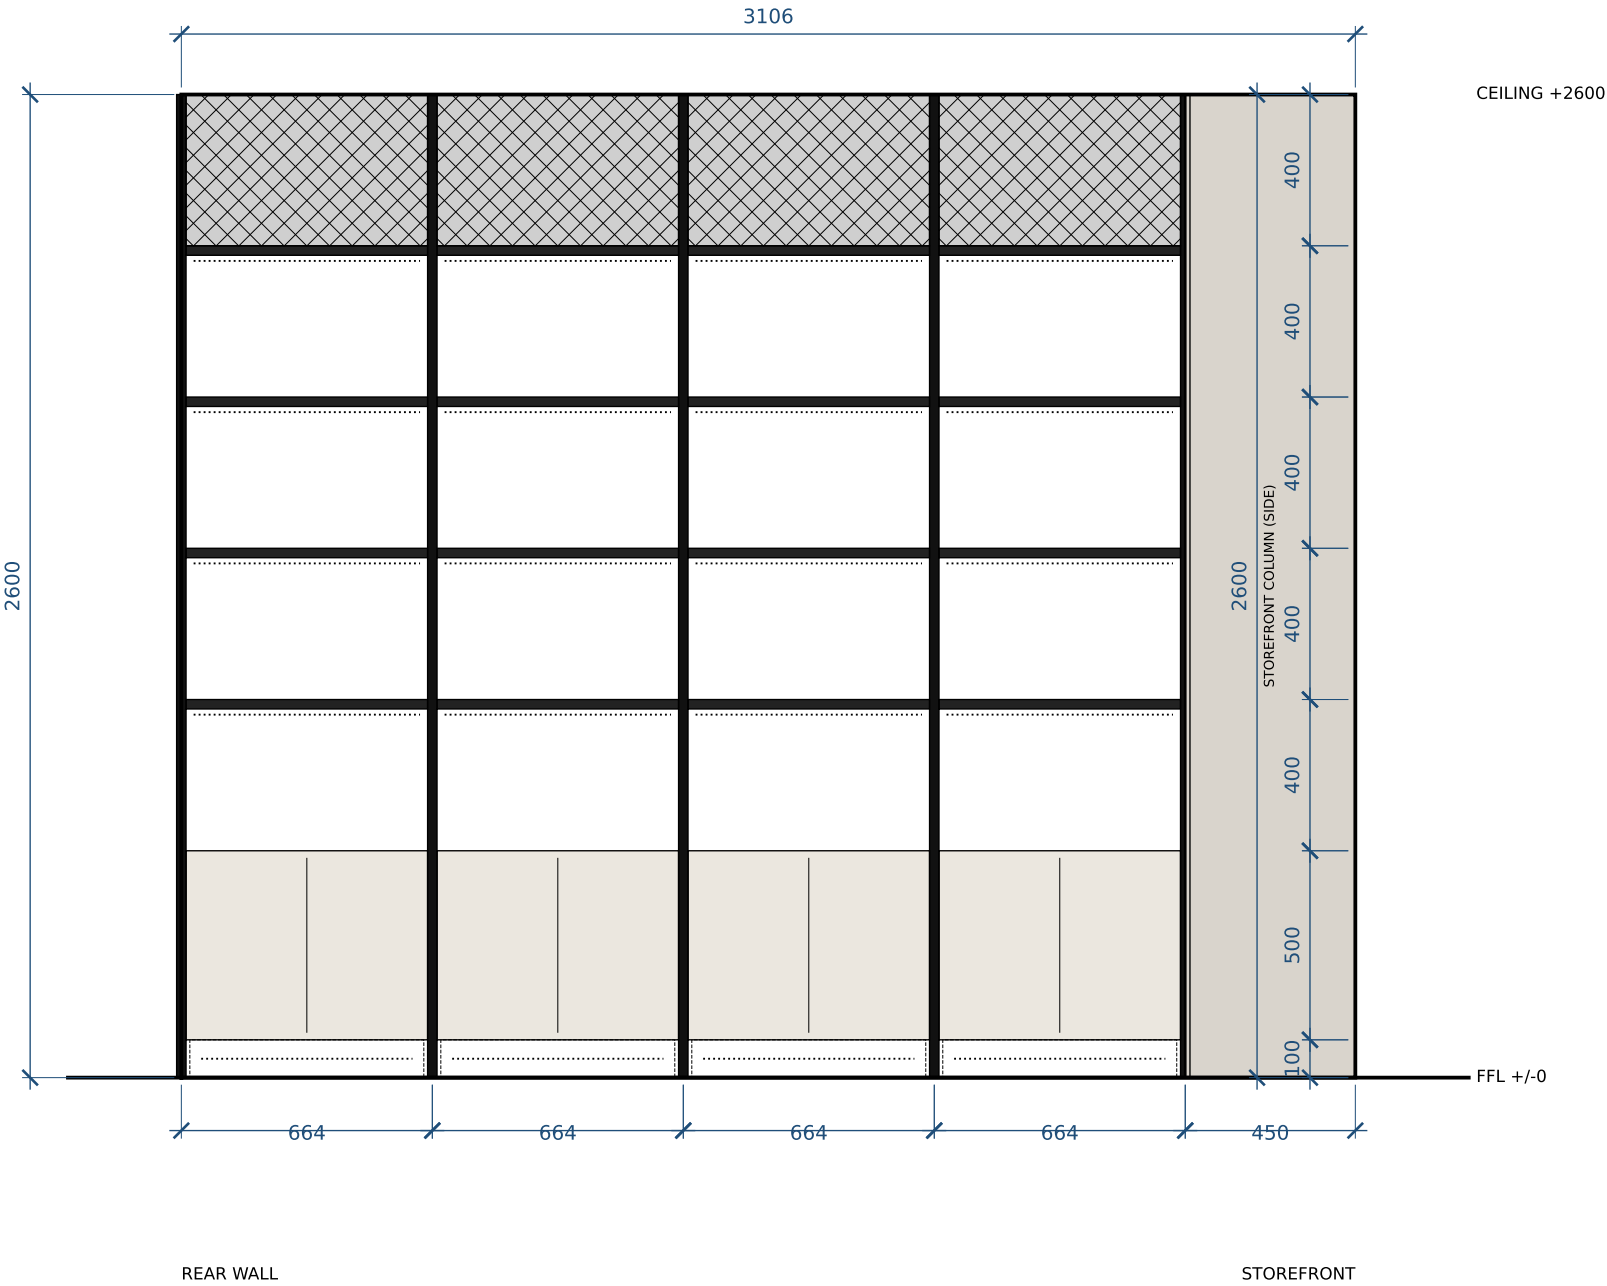

Site / consultant items still open: #4 finished size, #16 MEP/fire, #23 north, #26 datum + wall thickness. Verify before fabrication.

