
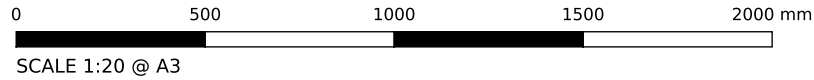


SETTING-OUT POINTS (mm, from datum)

- A x=0 y=0 datum / front-left internal corner
- B x=2400 y=0 front-right internal corner
- C x=2400 y=3106 rear-right internal corner
- D x=0 y=3106 rear-left internal corner
- E x=250 y=- left unit face line
- F x=2150 y=- right unit face line
- G x=1200 y=- shop centre line

Ceiling +2600 above FFL (locked).
Clear aisle 1900 = 2400 - 2 x 250 (derived).
Is 2400 x 3106 finished size? TBC #4.

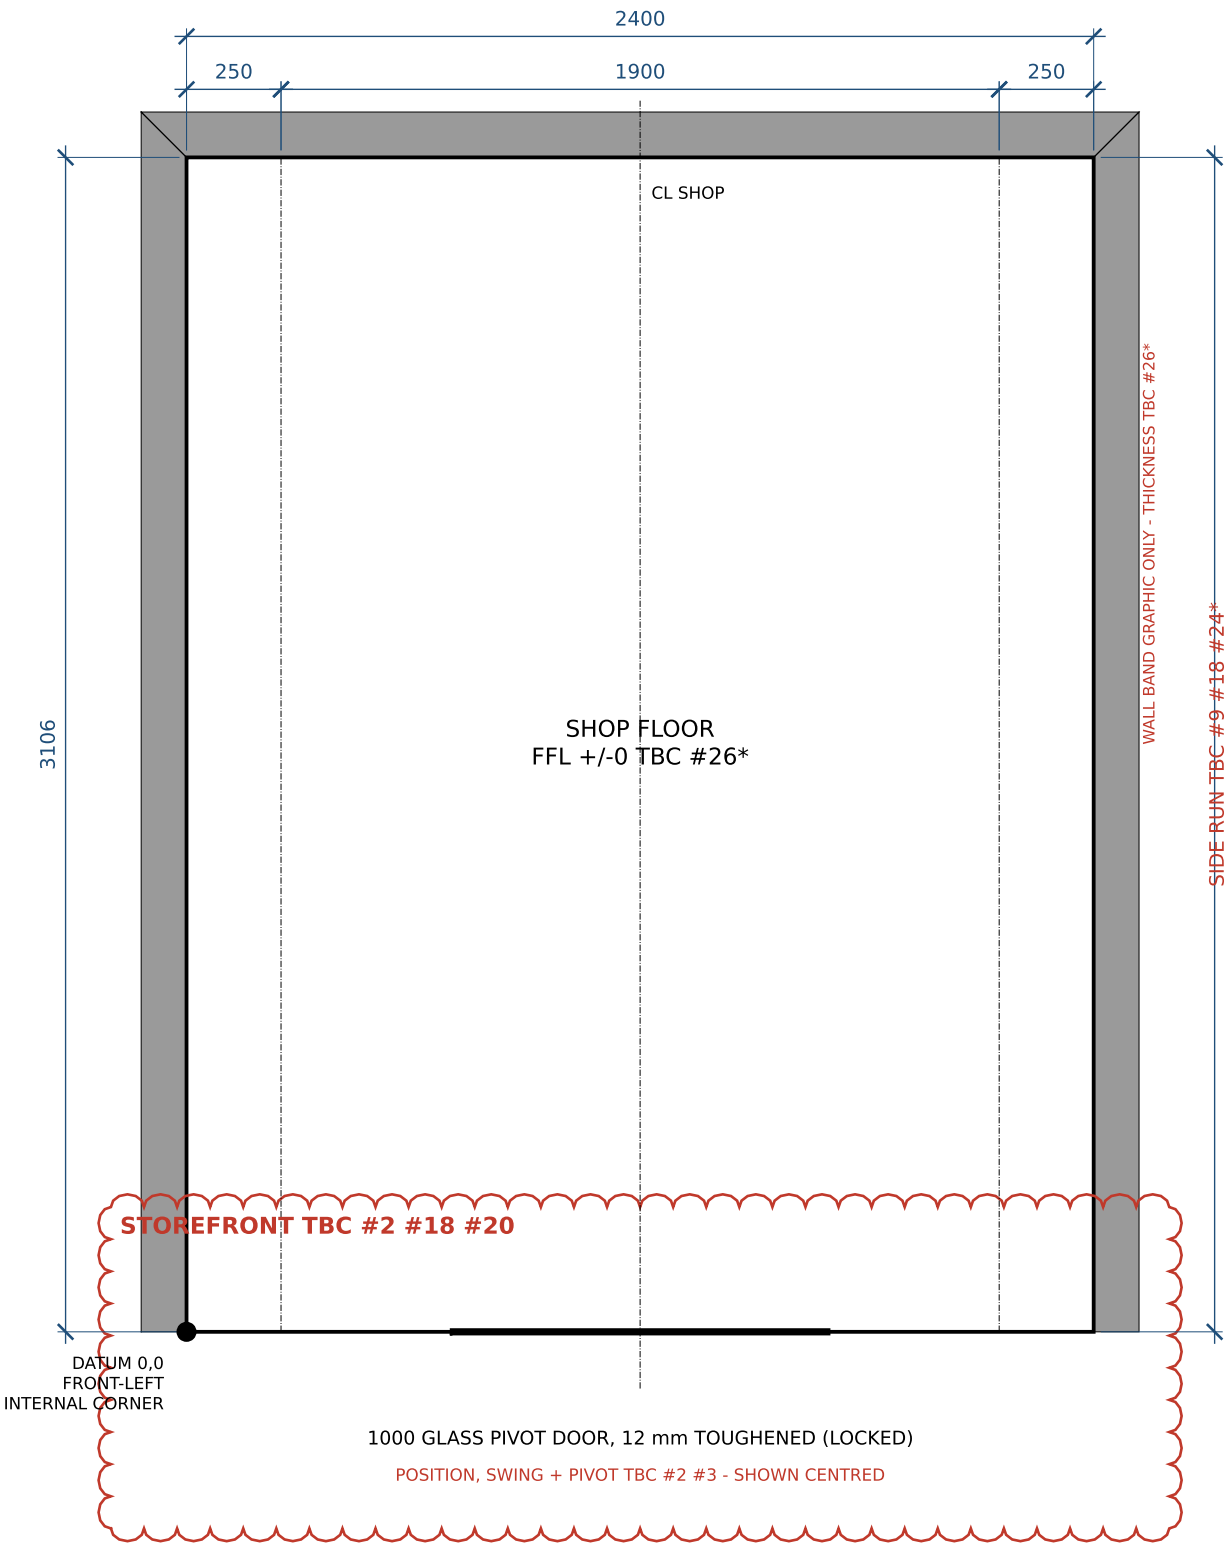

BORN FRAGRANCE

PROJECT BORN FRAGRANCE - shop fit-out

SHEET **SD-01**

TITLE **SETTING-OUT PLAN**

SCALE 1:20 @ A3

DATE 2026-10-05

REV 00 - preliminary

SPEC spec/SHOP_SPEC.json @ e1fbc1c

DRAWN Claude Code (AI), for owner review

TBC ITEMS ON THIS SHEET

- #2 Display column width, door opening width, fixed glass
- #3 Door swing direction and pivot offset
- #4 Is 2400 x 3106 the finished size (after plaster)?
- #18 Storefront display column depth, and shelf facing (street, shop or both)
- #20 Entrance threshold / step and any floor level change
- #23* North direction
- #26* Vertical datum (FFL) and wall thickness / construction
- #16 Fixings, MEP, fire and escape requirements



* proposed item, not yet in spec/TBC.md
TBC items are shown in revision clouds.
Dimensions computed from SHOP_SPEC.json.
Do not scale from the render.

PRELIMINARY - NOT FOR CONSTRUCTION

LEGEND

- Display unit, 25x25x1.6 + 20x20x1.6 MS SHS, matte black powder coat, 250 deep (locked)
- Counter 1000x450x900H, 20x20 black frame, light panel + mesh insert, light top (locked)

Counter centred x 700-1700 is a PROPOSAL.
Side clearance 450 < 600: CHECK staff access.
Exclusions: no timber, brass, plants, products.

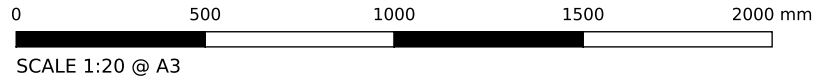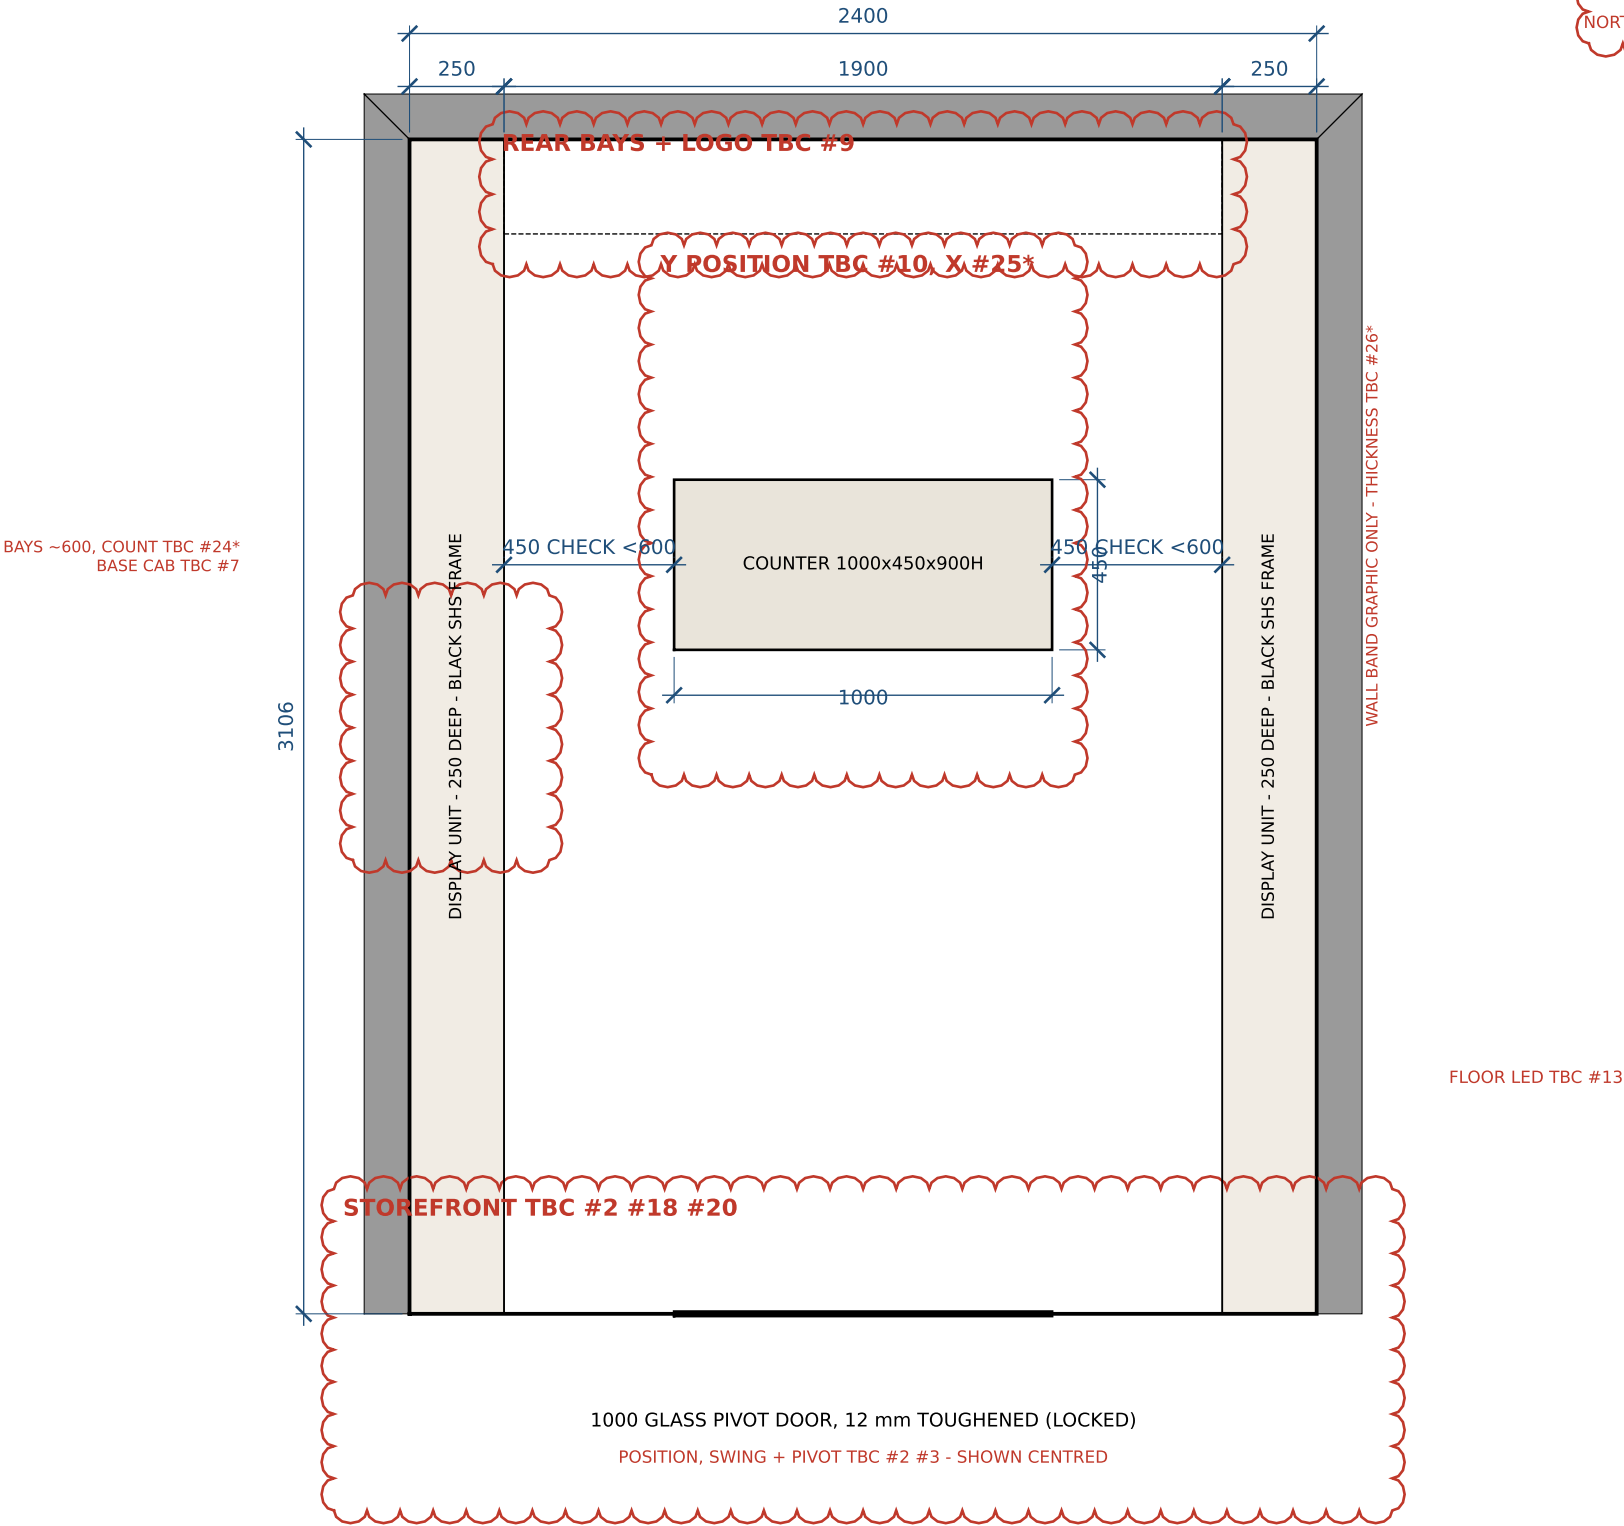

BORN FRAGRANCE

PROJECT BORN FRAGRANCE - shop fit-out

SHEET **SD-02**

TITLE **DISPLAY / FURNITURE PLAN**

SCALE 1:20 @ A3

DATE 2026-10-05

REV 00 - preliminary

SPEC spec/SHOP_SPEC.json @ e1fbc1c

DRAWN Claude Code (AI), for owner review

TBC ITEMS ON THIS SHEET

- #7 Base cabinet height and door type
- #9 Rear wall bay width, shelf count, logo size and height
- #10 Counter distance from rear wall and staff clearance
- #13 Floor-level LED strip (visible in render): keep or omit
- #18 Storefront display column depth, and shelf facing (street, shop or both)
- #24* Side bay count, widths and upright spacing
- #25* Counter lateral position (centring is a proposal)
- #4 Is 2400 x 3106 the finished size (after plaster)?

* proposed item, not yet in spec/TBC.md
TBC items are shown in revision clouds.
Dimensions computed from SHOP_SPEC.json.
Do not scale from the render.

PRELIMINARY - NOT FOR CONSTRUCTION

2 mm grout. Joints between tiles only;
perimeter/movement joint TBC #26*.

across: 0 full + 2 x 1199
depth: 4 full + 2 x 348

across: 2 full + 2 x 597
depth: 1 full + 2 x 951

TILE UNDER
UNITS TBC #14



N ?
NORTH TBC #23*



SHEET **SD-03**

SCALE 1:20 @ A3


REV 00 - preliminary

DRAWN Claude Code (AI), for owner review

- #22 Floor tile orientation (1200 across or along), and cut sizes allowing for 2 mm grout ($2 \times 1200 + \text{joint} = 2402 > 2400$; depth cuts approx 348, not 353)
- #14 Floor tile extent under display units
- #20 Entrance threshold / step and any floor level change
- #4 Is 2400 x 3106 the finished size (after plaster)?
- #26* Vertical datum (FFL) and wall thickness / construction

* proposed item, not yet in spec/TBC.md
TBC items are shown in revision clouds.
Dimensions computed from SHOP_SPEC.json.
Do not scale from the render.
PRELIMINARY - NOT FOR CONSTRUCTION



PRELIMINARY - NOT FOR CONSTRUCTION

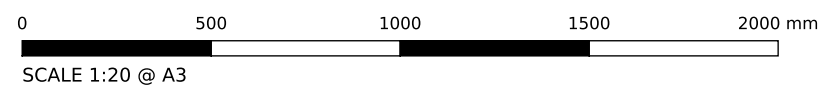

LIGHTING LEGEND (3000 K)

- Black ceiling track (2 no., locked)
- Black cylindrical adjustable spot (count TBC #11)
- Concealed 3000 K LED under shelves (locked)

No pendants or decorative ceiling features.
Positions shown are diagrammatic only.
Floor-level LED strip TBC #13.

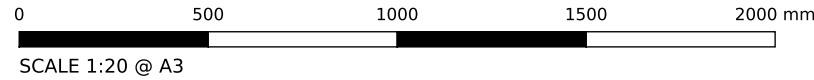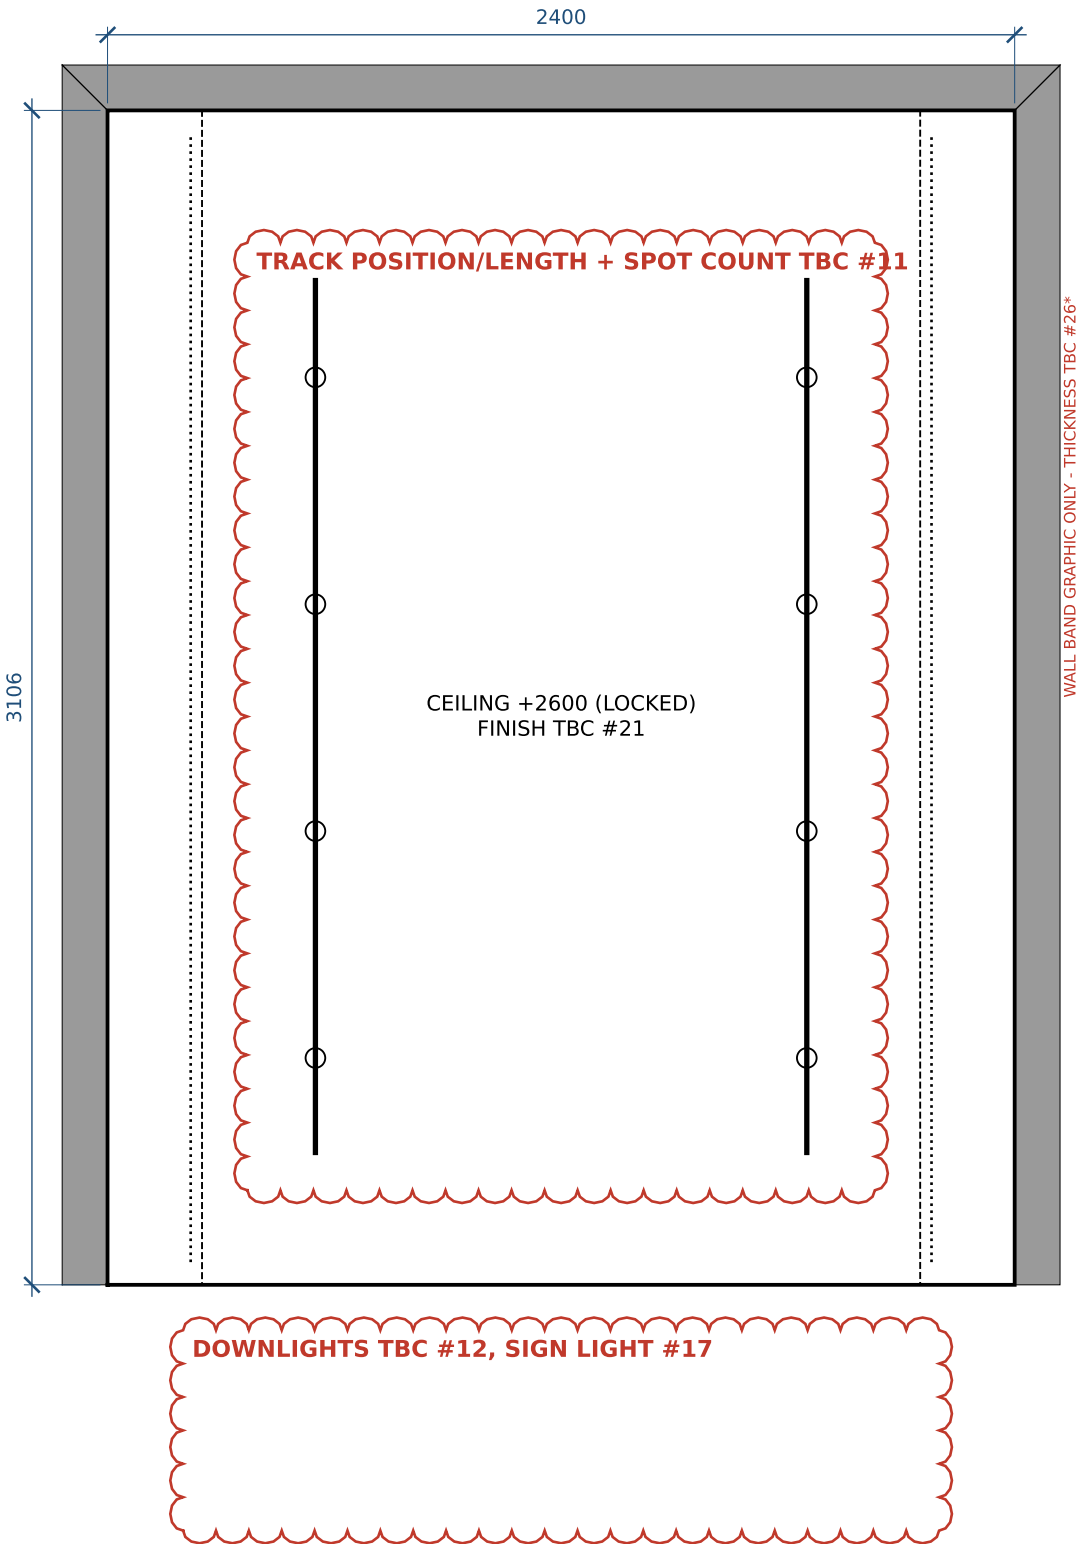

BORN FRAGRANCE

PROJECT BORN FRAGRANCE - shop fit-out

SHEET **SD-04**

TITLE **REFLECTED CEILING PLAN**

SCALE 1:20 @ A3

DATE 2026-10-05

REV 00 - preliminary

SPEC spec/SHOP_SPEC.json @ e1fbc1c

DRAWN Claude Code (AI), for owner review

TBC ITEMS ON THIS SHEET



- #11 Track positions and lengths, spotlight count
- #12 Recessed downlights (visible in render): keep or omit
- #13 Floor-level LED strip (visible in render): keep or omit
- #17 Exterior sign illumination: halo-lit (spec) vs front-lit by downlights (render)
- #21 Ceiling finish
- #4 Is 2400 x 3106 the finished size (after plaster)?

* proposed item, not yet in spec/TBC.md
TBC items are shown in revision clouds.
Dimensions computed from SHOP_SPEC.json.
Do not scale from the render.

PRELIMINARY - NOT FOR CONSTRUCTION

MATERIALS (LOCKED)

M1 Raw textured light plaster
M2 25x25x1.6 / 20x20x1.6 MS SHS, matte black PPC
M3 ~20x40 diamond expanded mesh, black
M4 1200x600 stone-look porcelain floor
L1 Concealed 3000 K LED under shelves
Heights not listed are TBC - never scaled.

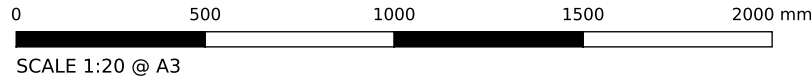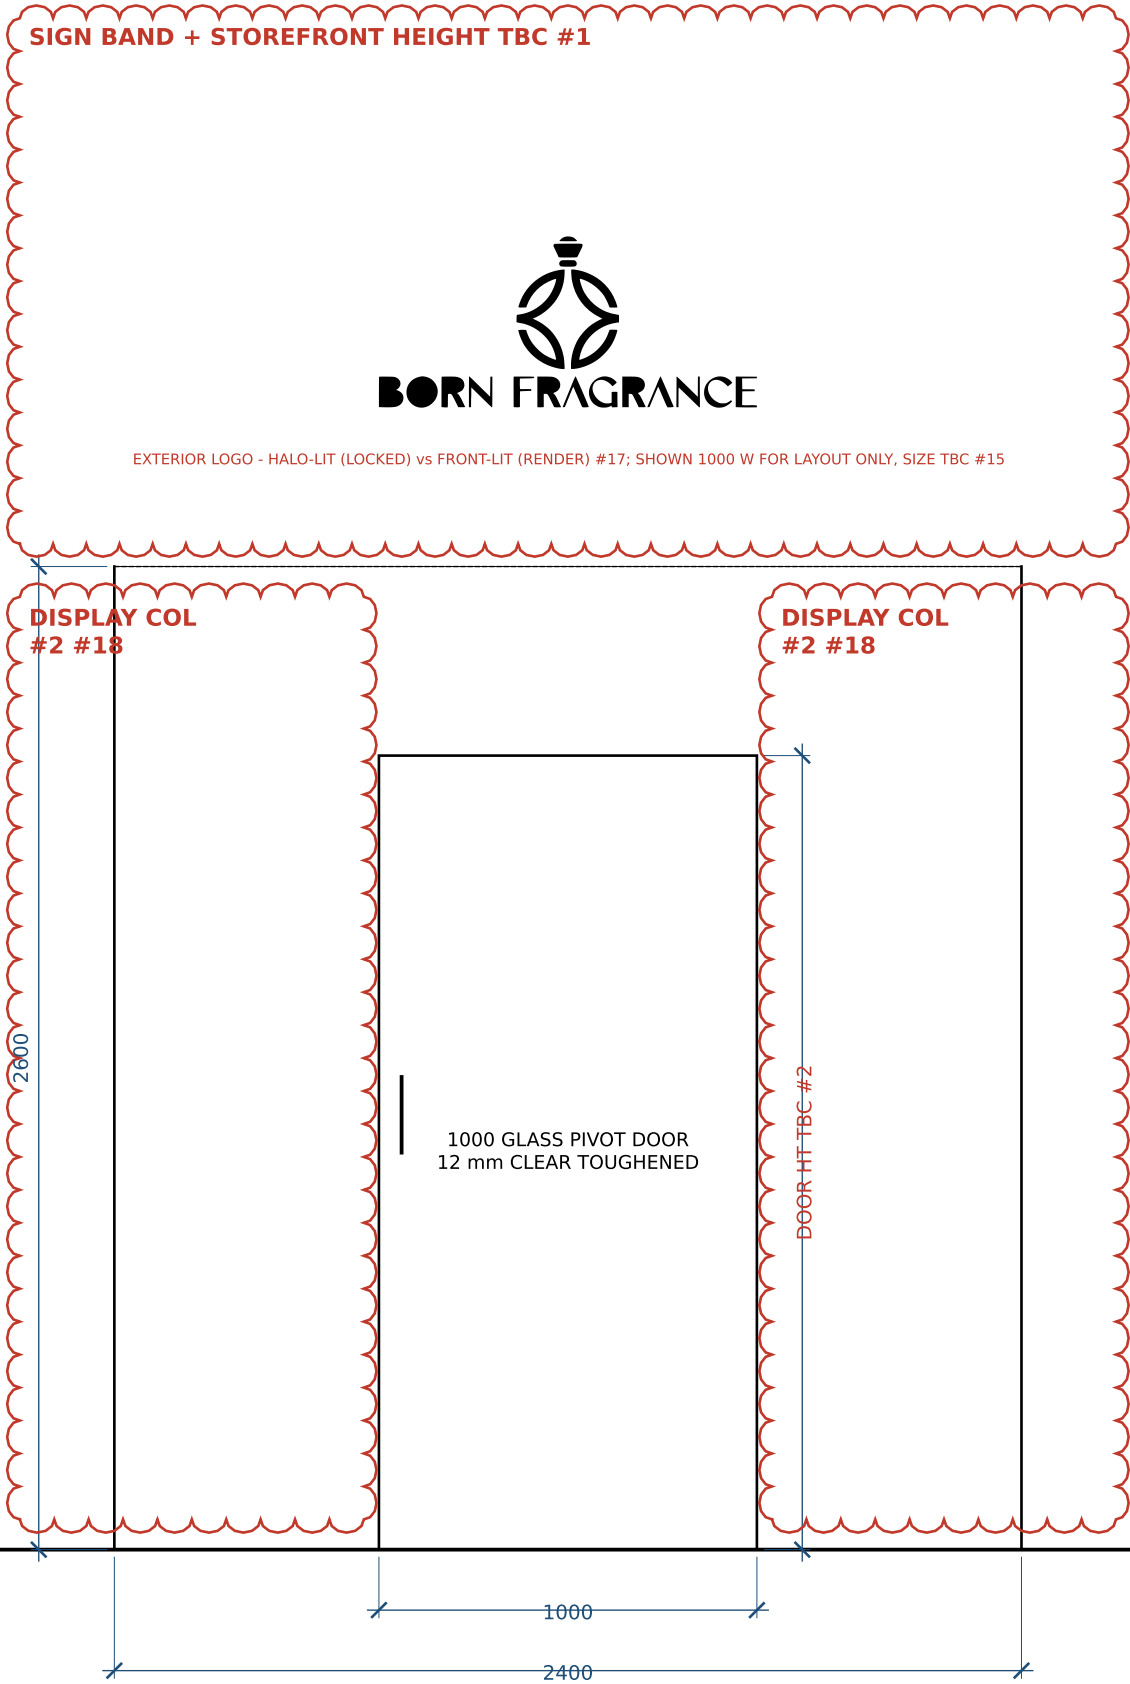

BORN FRAGRANCE

PROJECT BORN FRAGRANCE - shop fit-out

SHEET **SD-05**

TITLE **STOREFRONT ELEVATION (EXTERNAL)**

SCALE 1:20 @ A3

DATE 2026-10-05

REV 00 - preliminary

SPEC spec/SHOP_SPEC.json @ e1fbc1c

DRAWN Claude Code (AI), for owner review

TBC ITEMS ON THIS SHEET


- #1 Storefront overall height and sign band height
- #2 Display column width, door opening width, fixed glass
- #3 Door swing direction and pivot offset
- #12 Recessed downlights (visible in render): keep or omit
- #15 Exterior and interior sign sizes
- #17 Exterior sign illumination: halo-lit (spec) vs front-lit by downlights (render)
- #18 Storefront display column depth, and shelf facing (street, shop or both)
- #20 Entrance threshold / step and any floor level change

* proposed item, not yet in spec/TBC.md
TBC items are shown in revision clouds.
Dimensions computed from SHOP_SPEC.json.
Do not scale from the render.

PRELIMINARY - NOT FOR CONSTRUCTION

MATERIALS (LOCKED)

M1 Raw textured light plaster
M2 25x25x1.6 / 20x20x1.6 MS SHS, matte black PPC
M3 ~20x40 diamond expanded mesh, black
M4 1200x600 stone-look porcelain floor
L1 Concealed 3000 K LED under shelves
Heights not listed are TBC - never scaled.

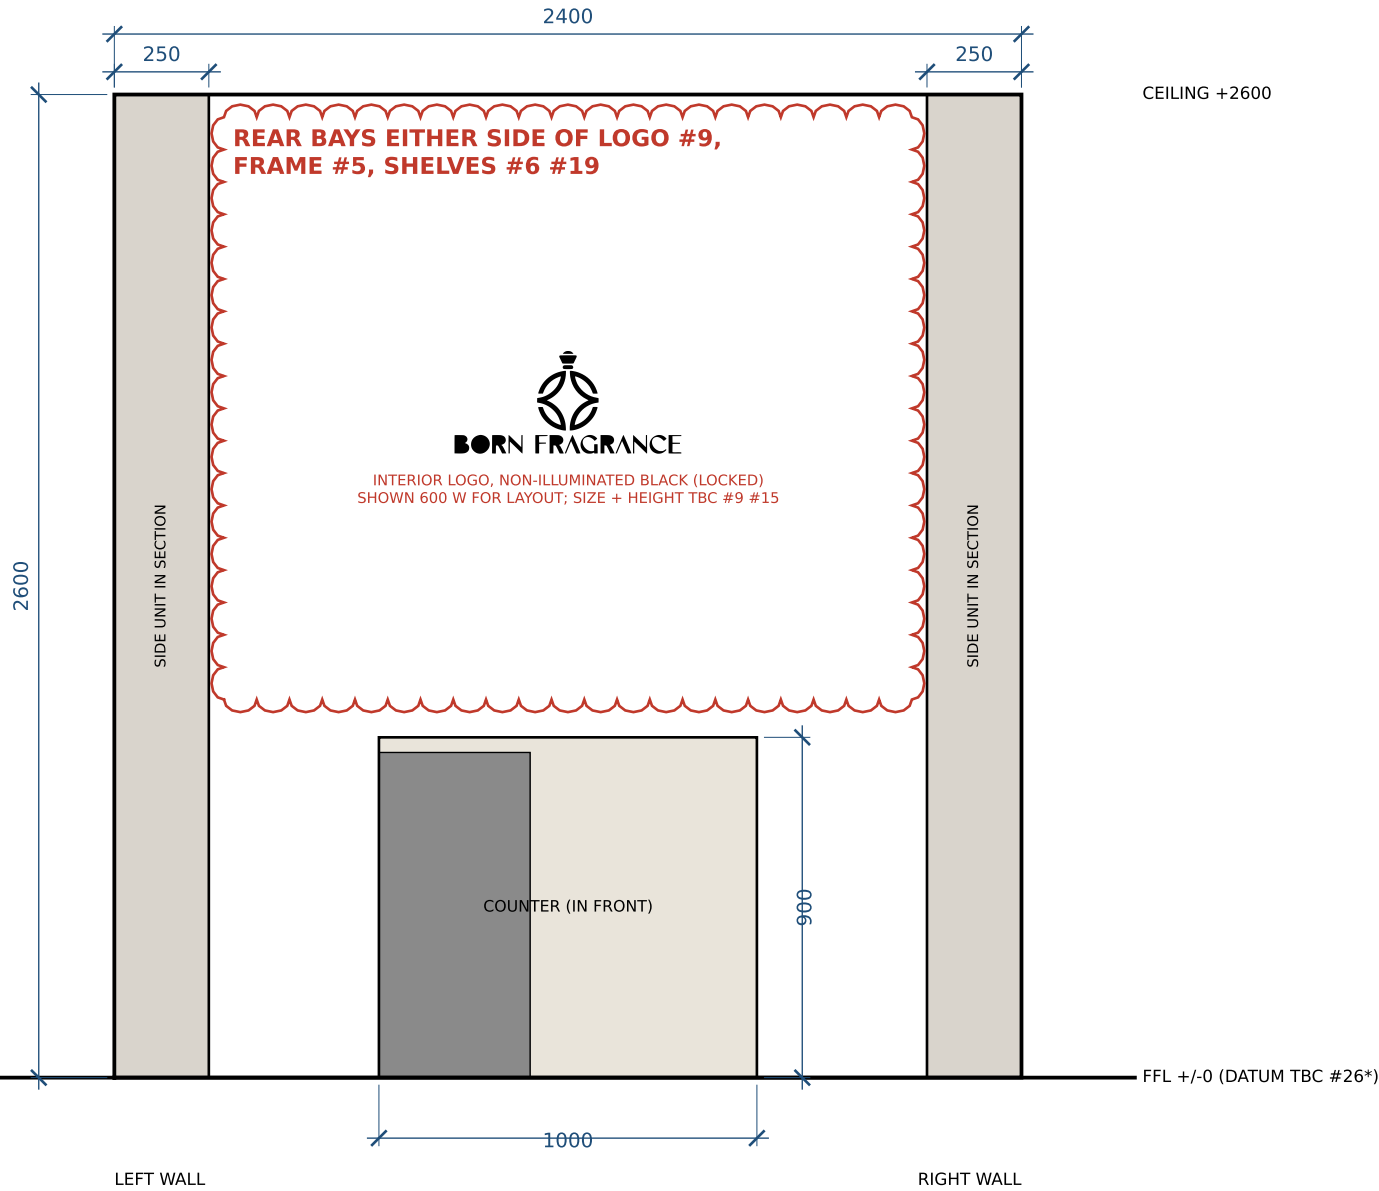

Counter x 700-1700 is a PROPOSAL (#25*); mesh insert size TBC #27*.



BORN FRAGRANCE

PROJECT BORN FRAGRANCE - shop fit-out

SHEET **SD-06**

TITLE **REAR ELEVATION (INTERNAL)**

SCALE 1:20 @ A3

DATE 2026-10-05

REV 00 - preliminary

SPEC spec/SHOP_SPEC.json @ e1fbc1c

DRAWN Claude Code (AI), for owner review

TBC ITEMS ON THIS SHEET



- #5 Display frame height (to ceiling or stopped short)
- #6 Shelf count and pitch per bay
- #7 Base cabinet height and door type
- #9 Rear wall bay width, shelf count, logo size and height
- #15 Exterior and interior sign sizes
- #19 Shelf material and thickness (render board: "black metal shelf")
- #25* Counter lateral position (centring is a proposal)
- #26* Vertical datum (FFL) and wall thickness / construction
- #27* Counter mesh insert size

* proposed item, not yet in spec/TBC.md
TBC items are shown in revision clouds.
Dimensions computed from SHOP_SPEC.json.
Do not scale from the render.

PRELIMINARY - NOT FOR CONSTRUCTION

MATERIALS (LOCKED)

M1 Raw textured light plaster
M2 25x25x1.6 / 20x20x1.6 MS SHS, matte black PPC
M3 ~20x40 diamond expanded mesh, black
M4 1200x600 stone-look porcelain floor
L1 Concealed 3000 K LED under shelves
Heights not listed are TBC - never scaled.

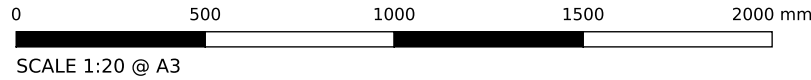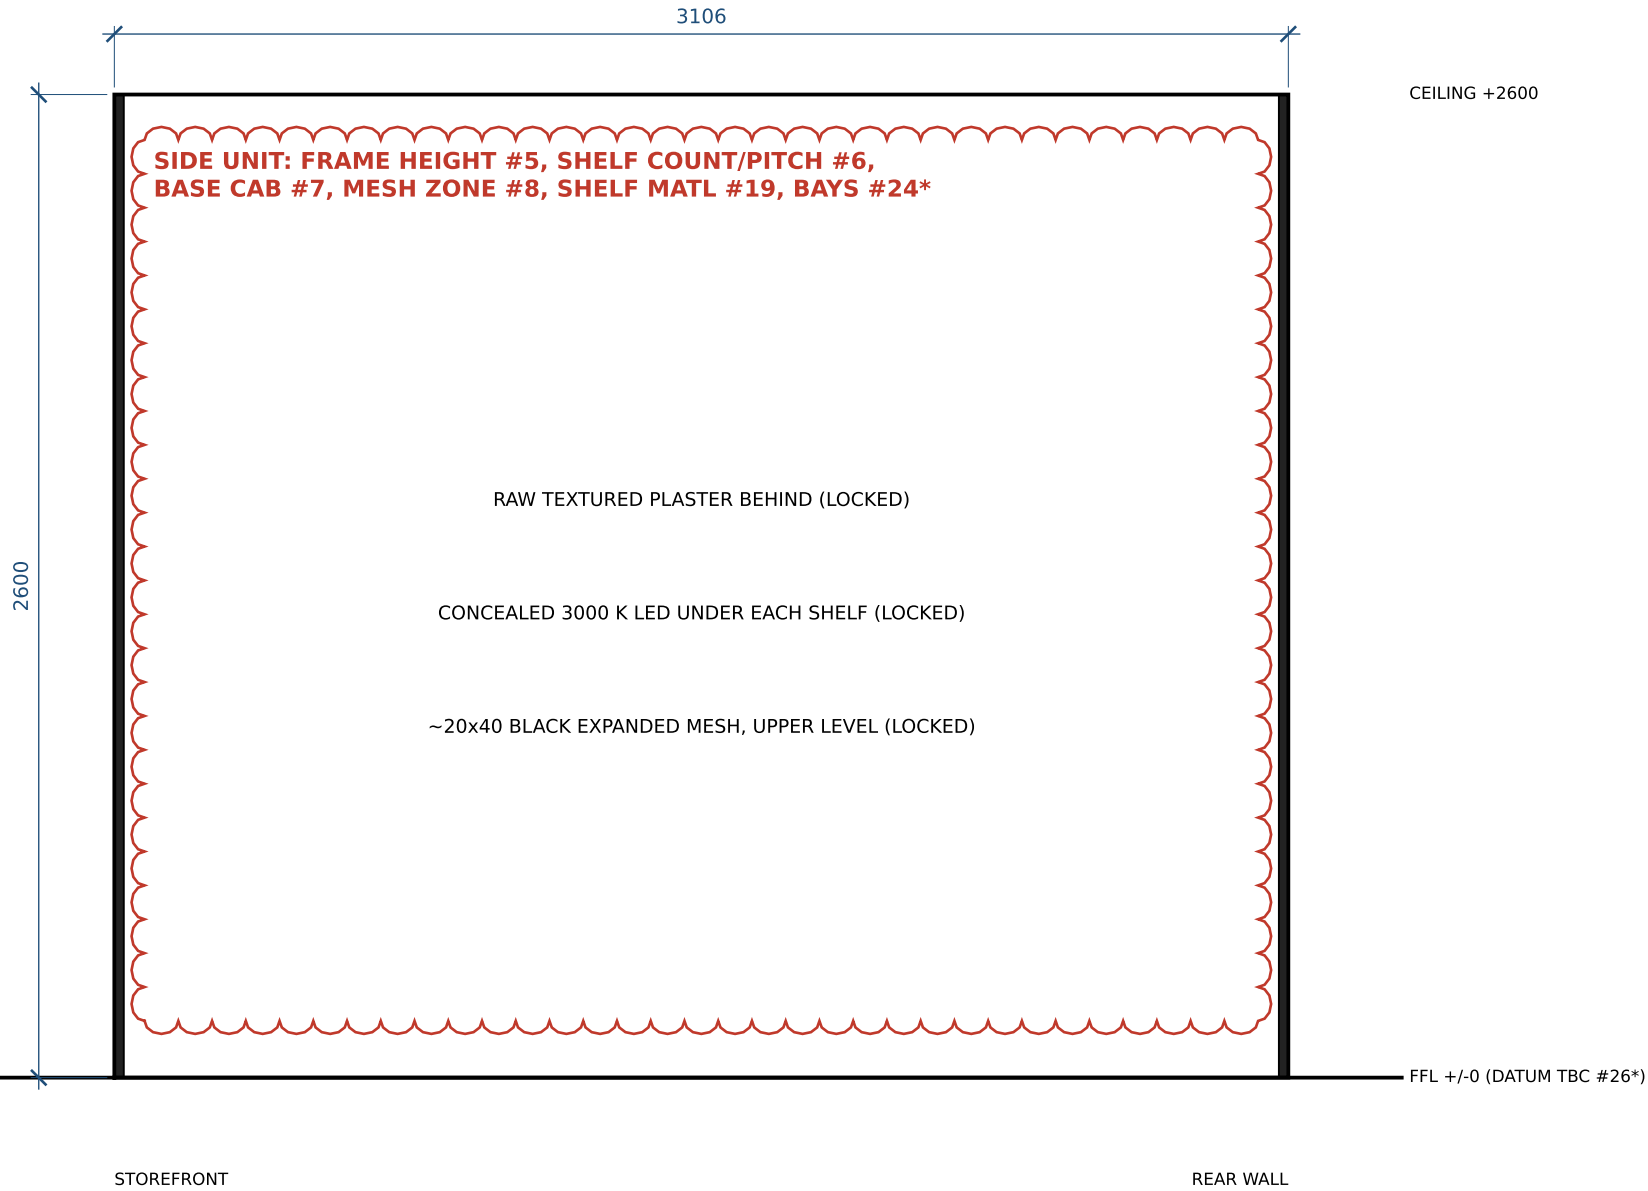

BORN FRAGRANCE

PROJECT BORN FRAGRANCE - shop fit-out

SHEET SD-07

TITLE LEFT ELEVATION (INTERNAL)

SCALE 1:20 @ A3

DATE 2026-10-05

REV 00 - preliminary

SPEC spec/SHOP_SPEC.json @ e1fbc1c

DRAWN Claude Code (AI), for owner review

TBC ITEMS ON THIS SHEET



- #5 Display frame height (to ceiling or stopped short)
- #6 Shelf count and pitch per bay
- #7 Base cabinet height and door type
- #8 Mesh extent on side walls
- #9 Rear wall bay width, shelf count, logo size and height
- #18 Storefront display column depth, and shelf facing (street, shop or both)
- #19 Shelf material and thickness (render board: "black metal shelf")
- #24* Side bay count, widths and upright spacing

* proposed item, not yet in spec/TBC.md
TBC items are shown in revision clouds.
Dimensions computed from SHOP_SPEC.json.
Do not scale from the render.

PRELIMINARY - NOT FOR CONSTRUCTION

MATERIALS (LOCKED)

M1 Raw textured light plaster
M2 25x25x1.6 / 20x20x1.6 MS SHS, matte black PPC
M3 ~20x40 diamond expanded mesh, black
M4 1200x600 stone-look porcelain floor
L1 Concealed 3000 K LED under shelves
Heights not listed are TBC - never scaled.

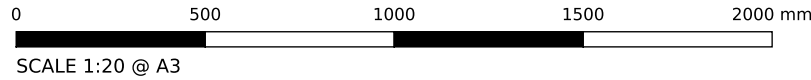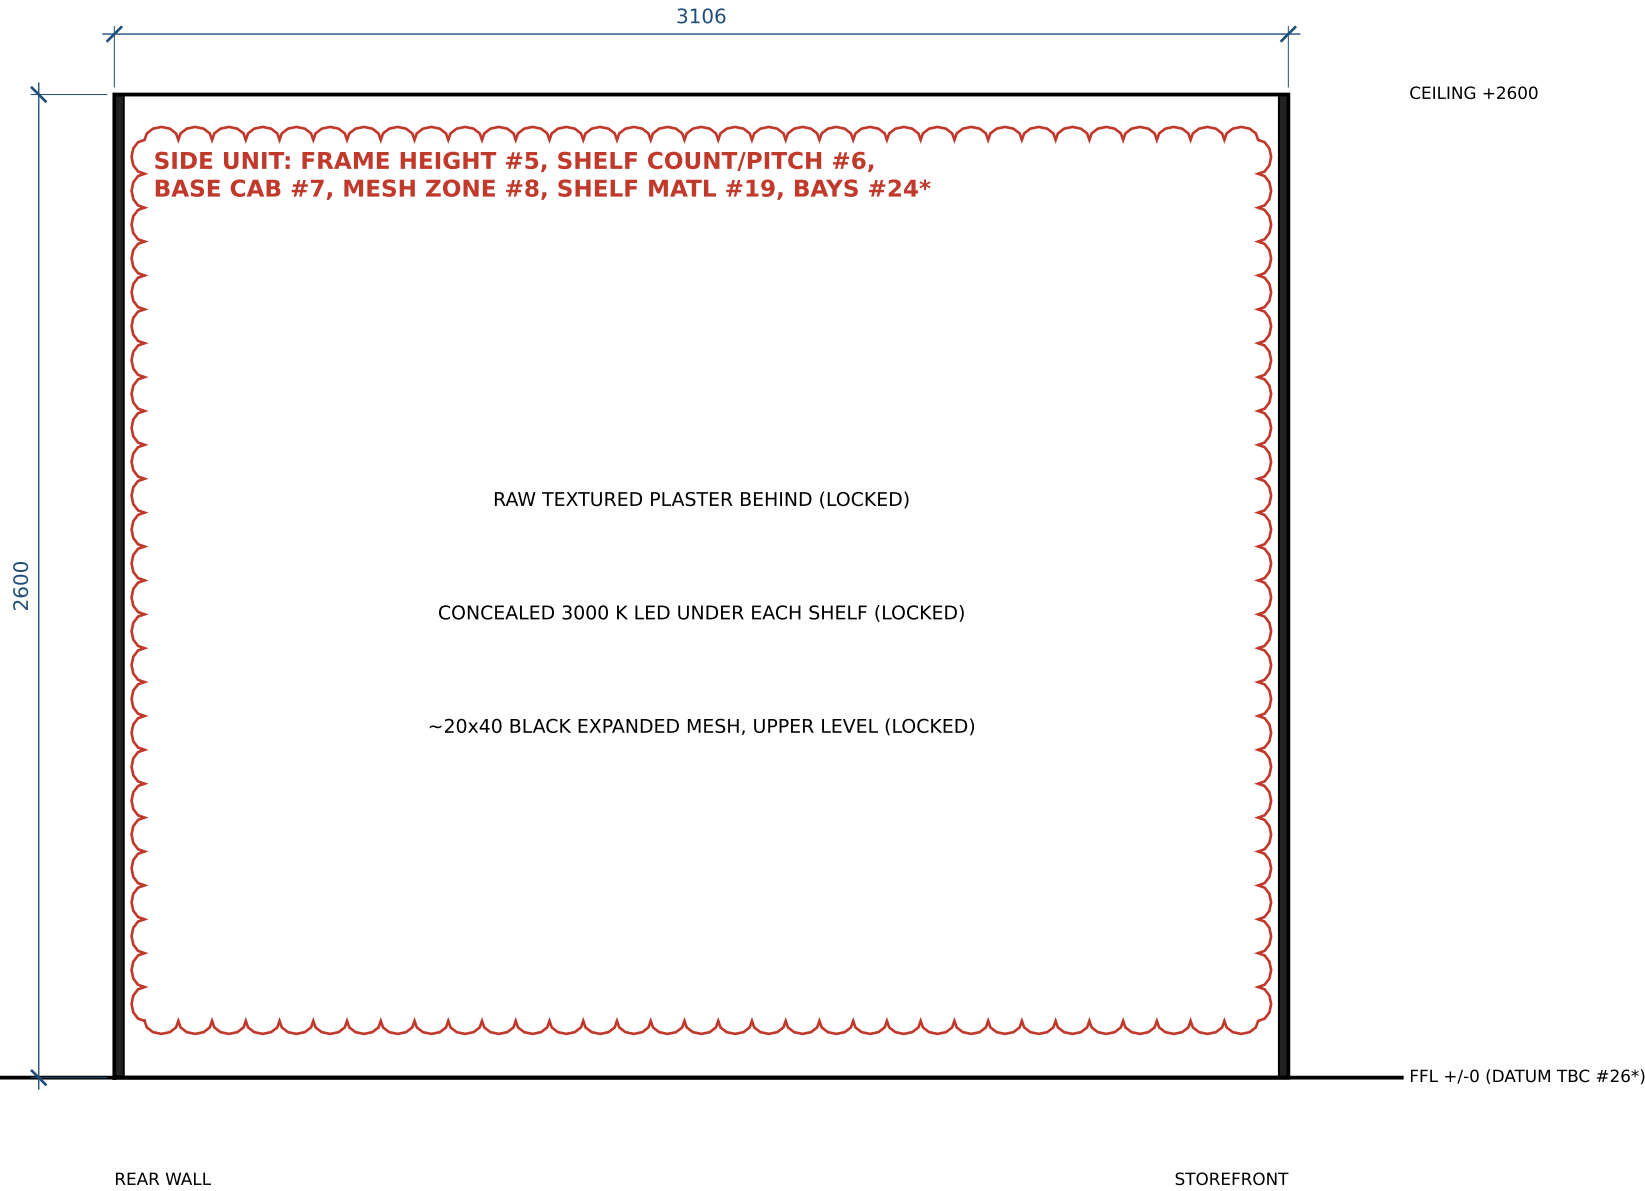

BORN FRAGRANCE

PROJECT BORN FRAGRANCE - shop fit-out

SHEET SD-08

TITLE RIGHT ELEVATION (INTERNAL)

SCALE 1:20 @ A3

DATE 2026-10-05

REV 00 - preliminary

SPEC spec/SHOP_SPEC.json @ e1fbc1c

DRAWN Claude Code (AI), for owner review

TBC ITEMS ON THIS SHEET

- #5 Display frame height (to ceiling or stopped short)
- #6 Shelf count and pitch per bay
- #7 Base cabinet height and door type
- #8 Mesh extent on side walls
- #9 Rear wall bay width, shelf count, logo size and height
- #18 Storefront display column depth, and shelf facing (street, shop or both)
- #19 Shelf material and thickness (render board: "black metal shelf")
- #24* Side bay count, widths and upright spacing

* proposed item, not yet in spec/TBC.md
TBC items are shown in revision clouds.
Dimensions computed from SHOP_SPEC.json.
Do not scale from the render.

PRELIMINARY - NOT FOR CONSTRUCTION