
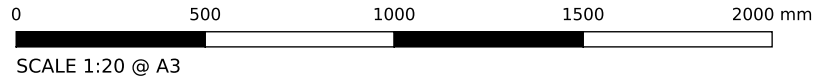


SETTING-OUT POINTS (mm, from datum)

- A x=0 y=0 datum / front-left internal corner
- B x=2400 y=0 front-right internal corner
- C x=2400 y=3106 rear-right internal corner
- D x=0 y=3106 rear-left internal corner
- E x=250 y=- left unit face line
- F x=2150 y=- right unit face line
- G x=1200 y=- shop centre line

Ceiling +2600 above FFL (locked).
Clear aisle 1900 = 2400 - 2 x 250 (derived).
Is 2400 x 3106 finished size? TBC #4.

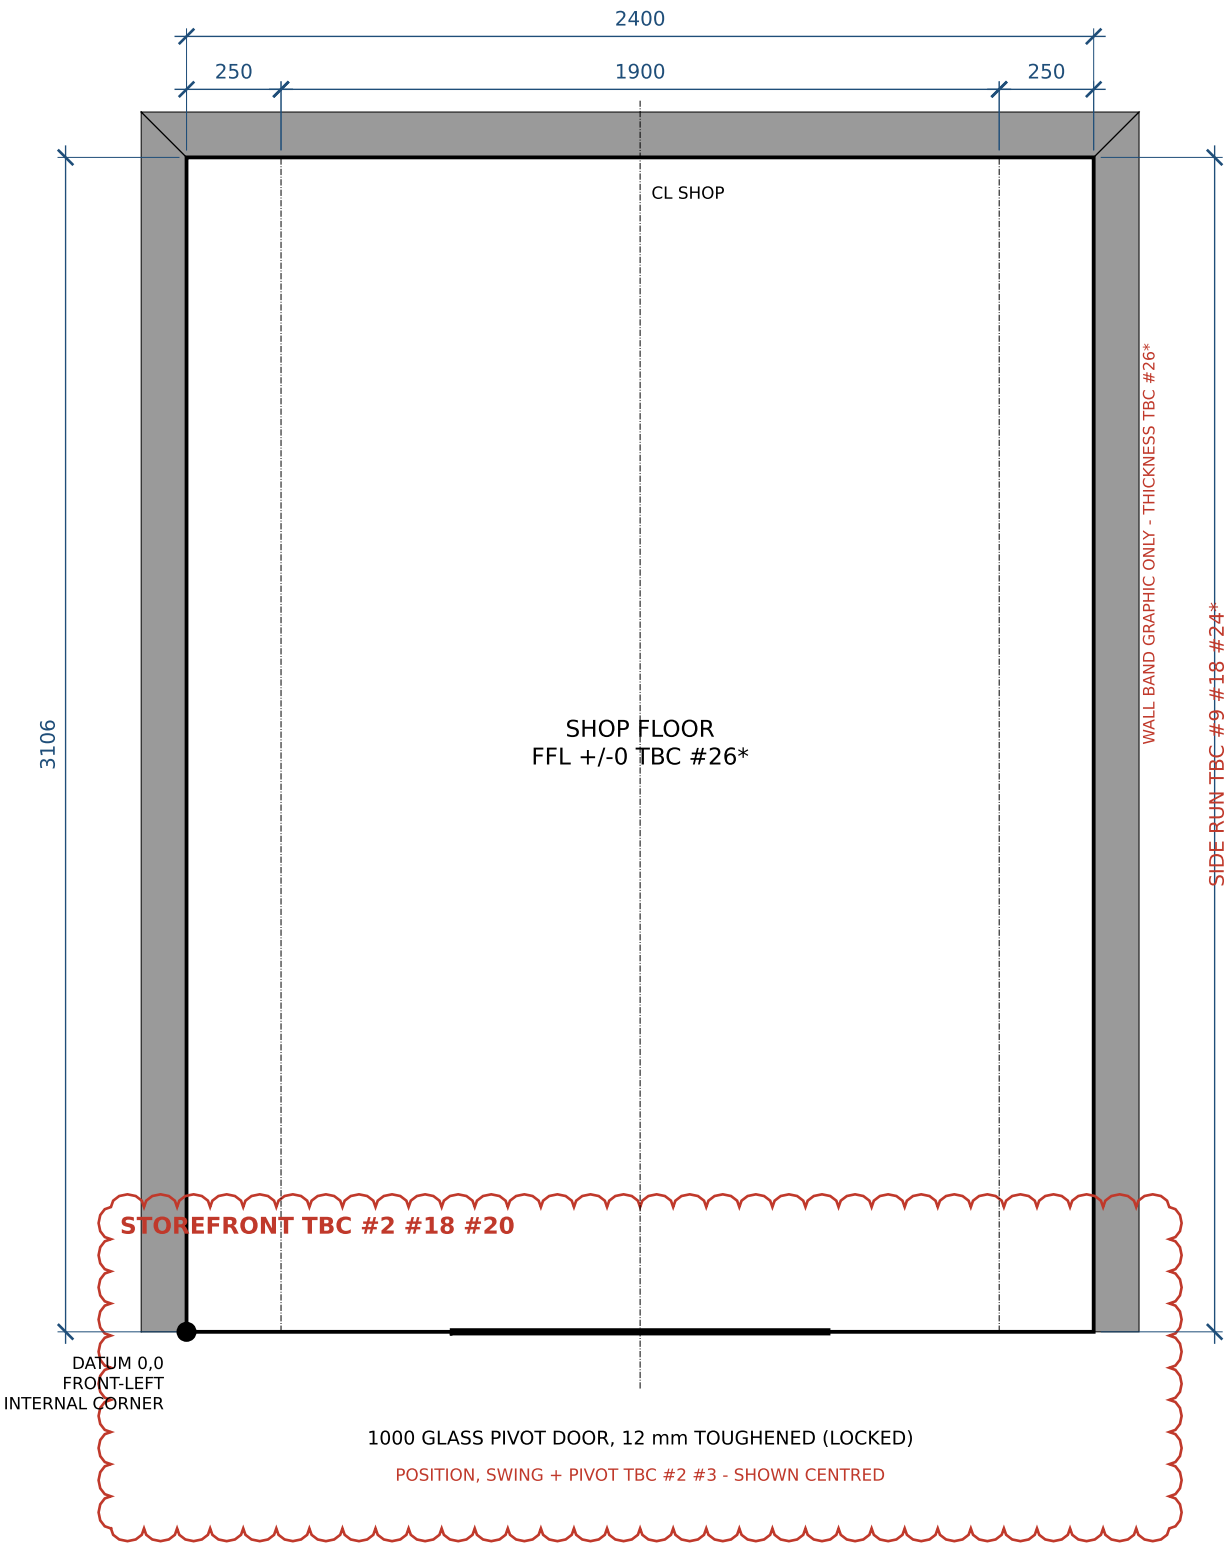

BORN FRAGRANCE

PROJECT BORN FRAGRANCE - shop fit-out

SHEET **SD-01**

TITLE **SETTING-OUT PLAN**

SCALE 1:20 @ A3

DATE 2026-10-05

REV 00 - preliminary

SPEC spec/SHOP_SPEC.json @ e1fbc1c

DRAWN Claude Code (AI), for owner review

TBC ITEMS ON THIS SHEET

- #2 Display column width, door opening width, fixed glass
- #3 Door swing direction and pivot offset
- #4 Is 2400 x 3106 the finished size (after plaster)?
- #18 Storefront display column depth, and shelf facing (street, shop or both)
- #20 Entrance threshold / step and any floor level change
- #23* North direction
- #26* Vertical datum (FFL) and wall thickness / construction
- #16 Fixings, MEP, fire and escape requirements

* proposed item, not yet in spec/TBC.md
TBC items are shown in revision clouds.
Dimensions computed from SHOP_SPEC.json.
Do not scale from the render.

PRELIMINARY - NOT FOR CONSTRUCTION