


Retail interior / coordinated design

Storefront, interior and display details · neutral material tones



STOREFRONT / DESIGN INTENT

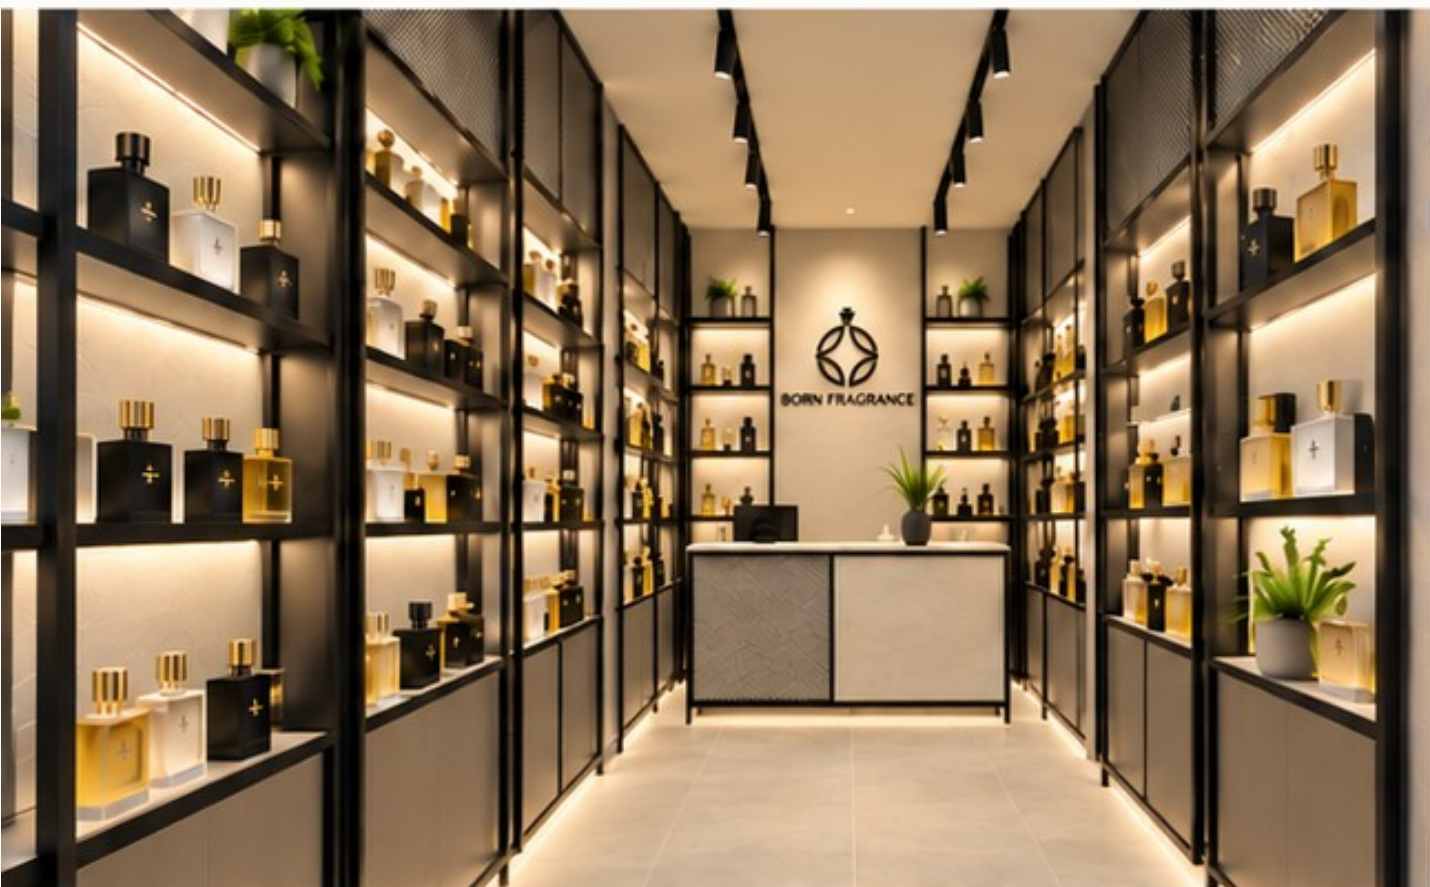

INTERIOR / DISPLAY AND COUNTER



MESH / LIGHT



DISPLAY FRAME



PLASTER / SHELF

Overall plan / setting-out

Setting-out / coordinated interfaces · 1:20 · finish-face dimensions; site verification pending

SET-OUT DATUMS

A 0 / 0
B 2400 / 0
C 2400 / 3106
D 0 / 3106

STREET-FACING DISPLAY

Dashed line: shelf above

Solid return toward interior

Wall bands graphic only
Thickness TBC #26
Envelope TBC #4

N ↓ STOREFRONT
ASSUMED #23

COUNTER FRAME
20 x 20 black steel

1000 x 450 COUNTER

PIVOT GLASS DOOR

REAR / SIDE JUNCTION

LOCAL PLAN 1:5

25 × 25 × 1.6 SHS / 250-deep units
Rear bay continues right; no overlap


DOOR EDGE / PIVOT

LOCAL PLAN 1:2

12 glass / 4 gap / 25 SHS · pivot fittings TBC #16


Ceiling / lighting coordination

Reflected ceiling plan · lighting, display footprints and dimensional coordination

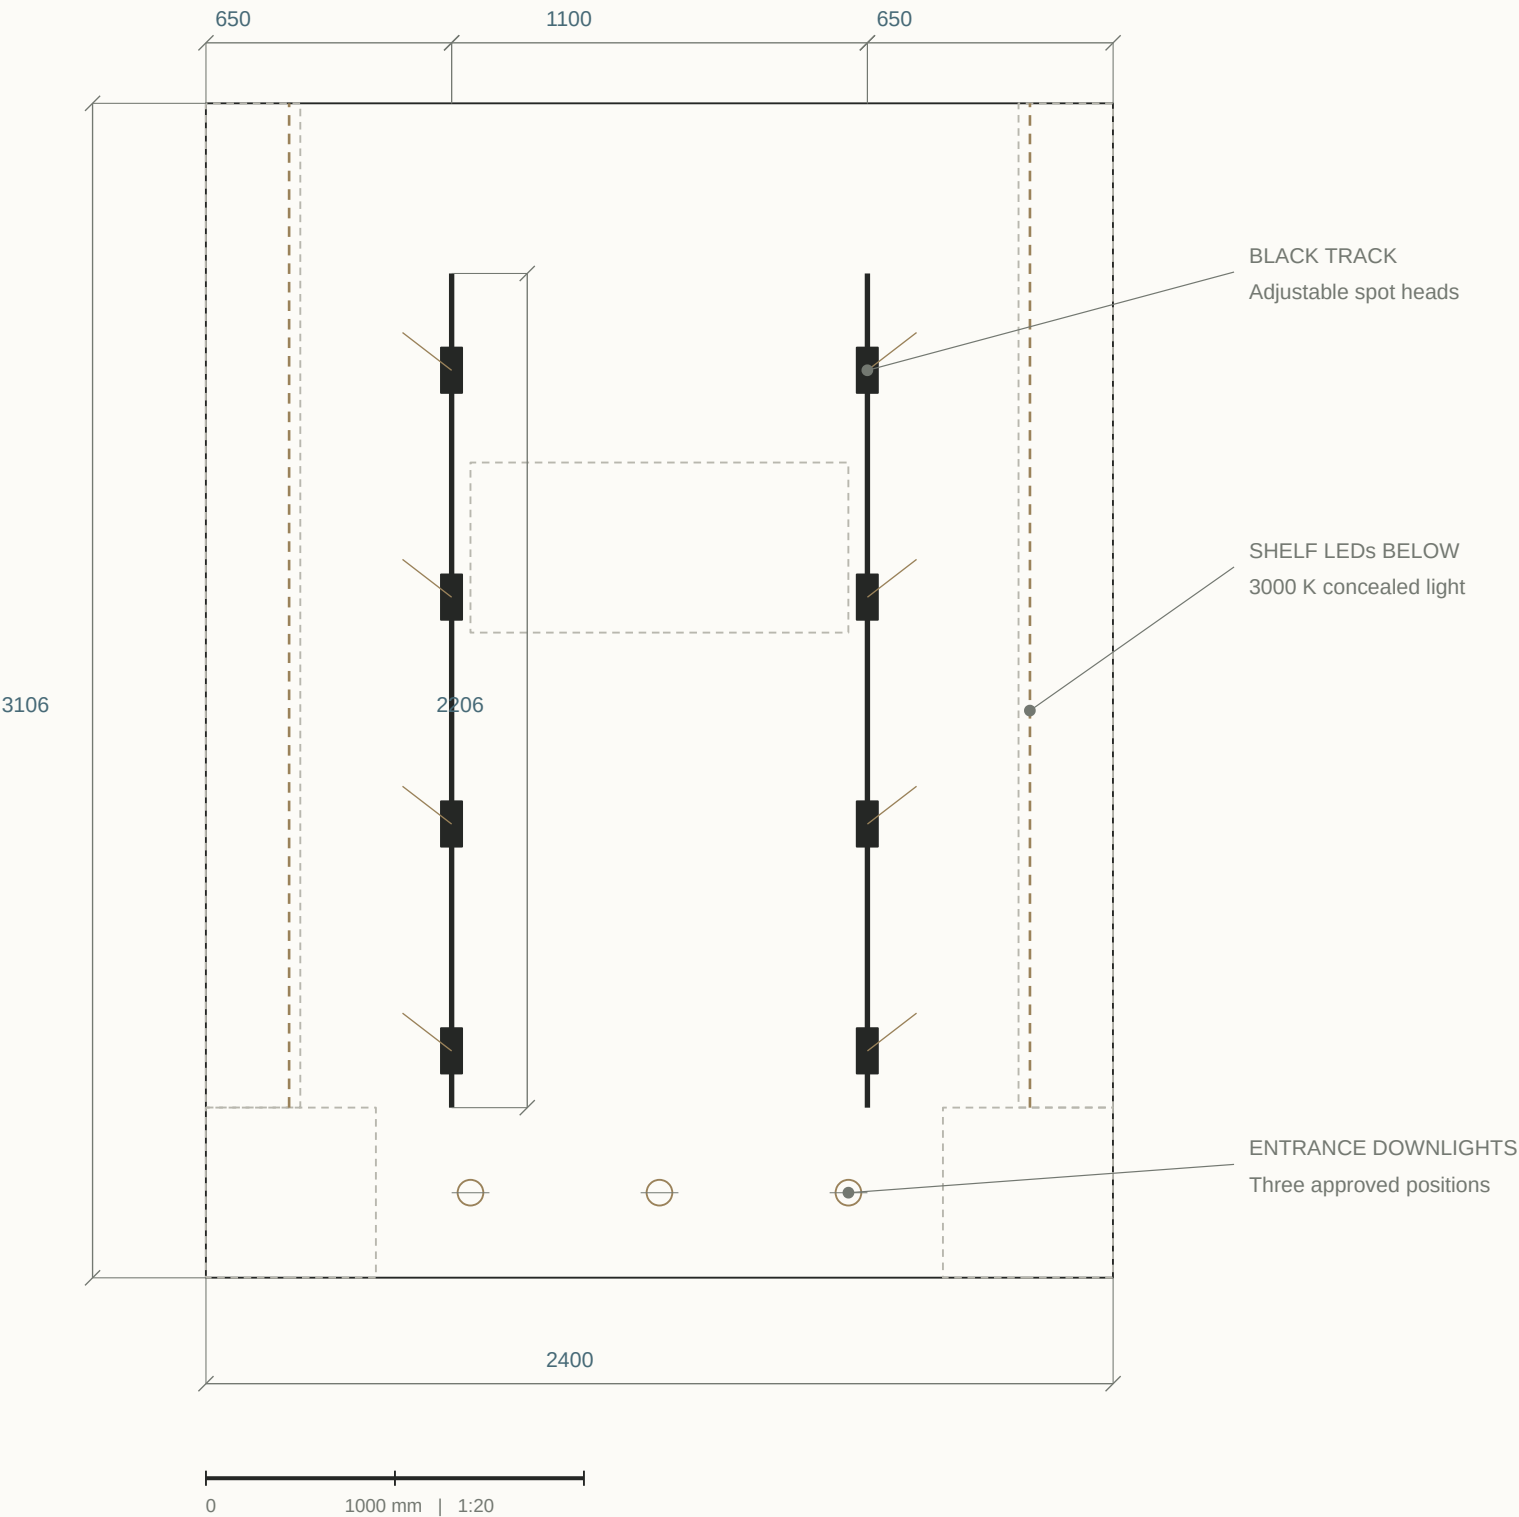

UNIT HEAD / CEILING


SECTION 1:5

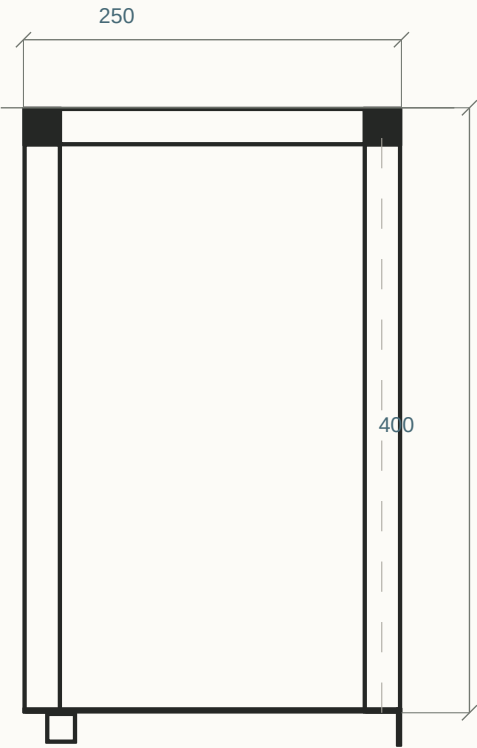

2600 ceiling / frame datum
Mesh zone 2200–2600 at front
Wall fixings TBC #16; no gypsum fixing

FOLDED TRAY / LIGHT


SECTION 1:2

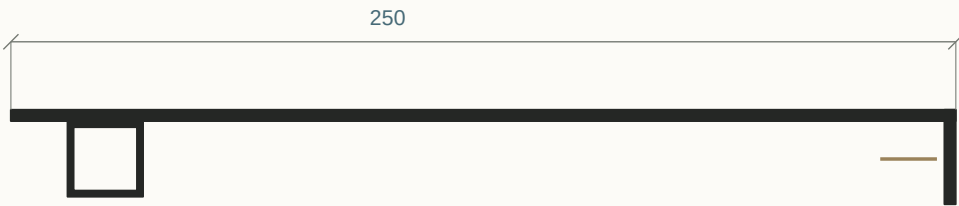

3 mm folded tray · 25 front downstand
20 × 20 × 1.6 support · LED profile TBC #16


Storefront / external elevation

Developed storefront · street-facing displays, glazed entrance and halo-lit brand

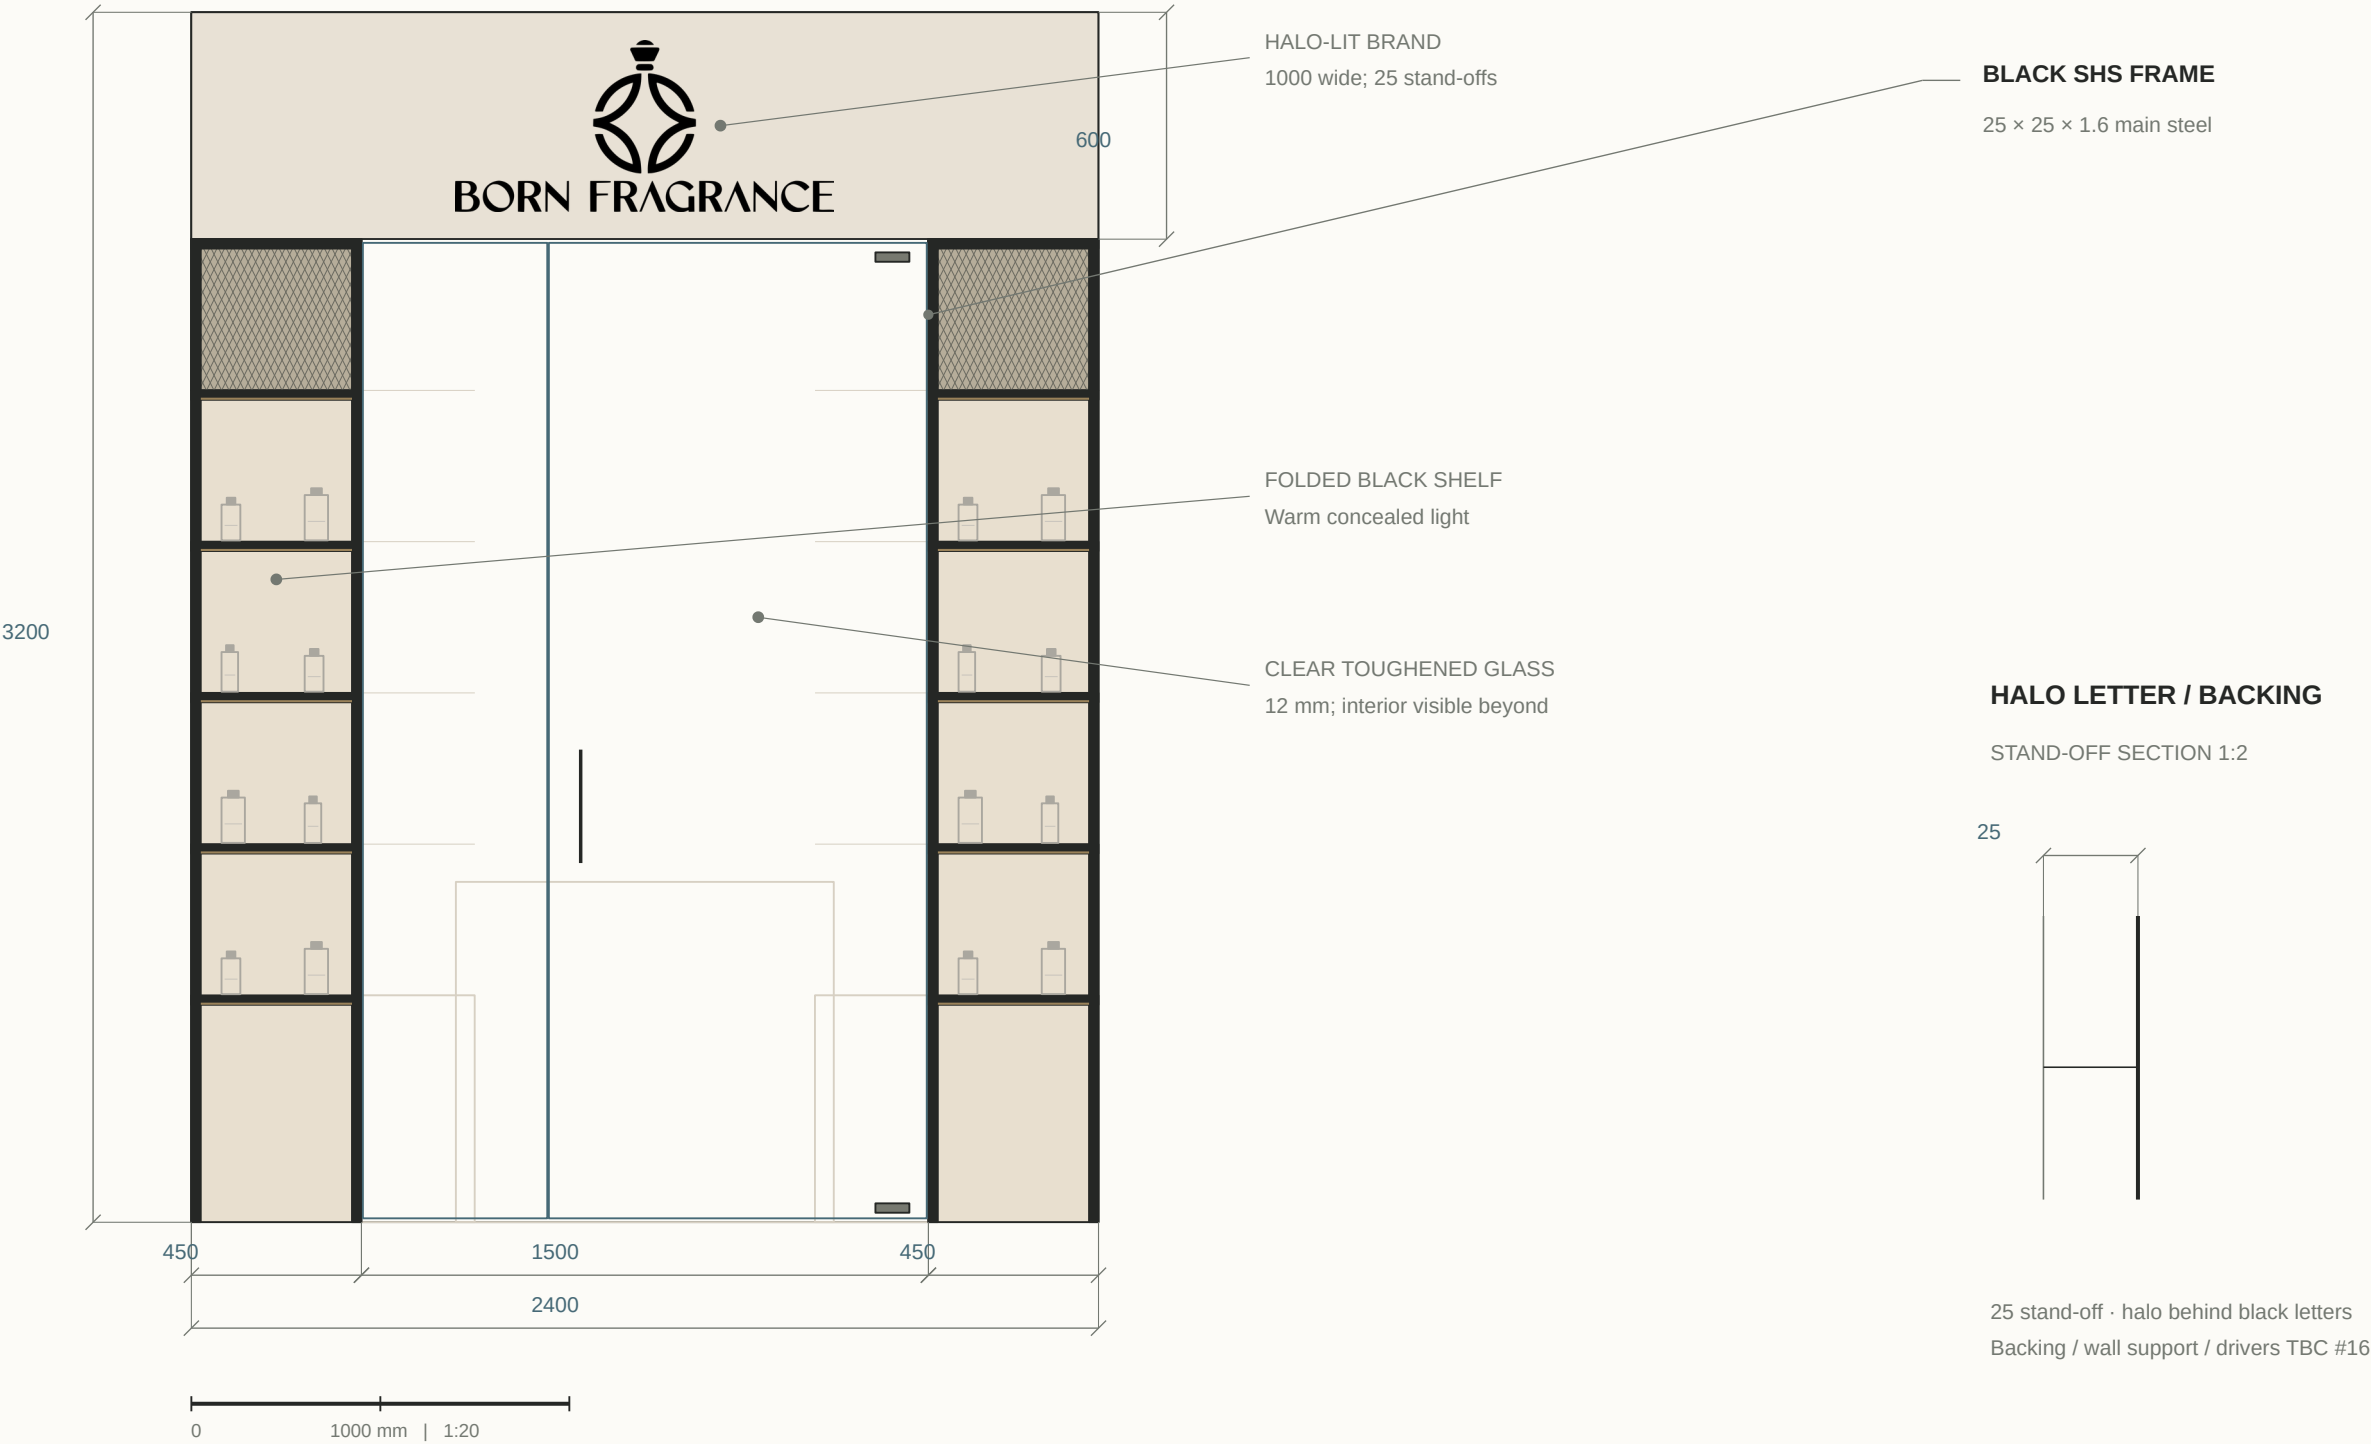


Rear focal wall / internal elevation

Rear focal wall · developed shelving + owner-directed counter front

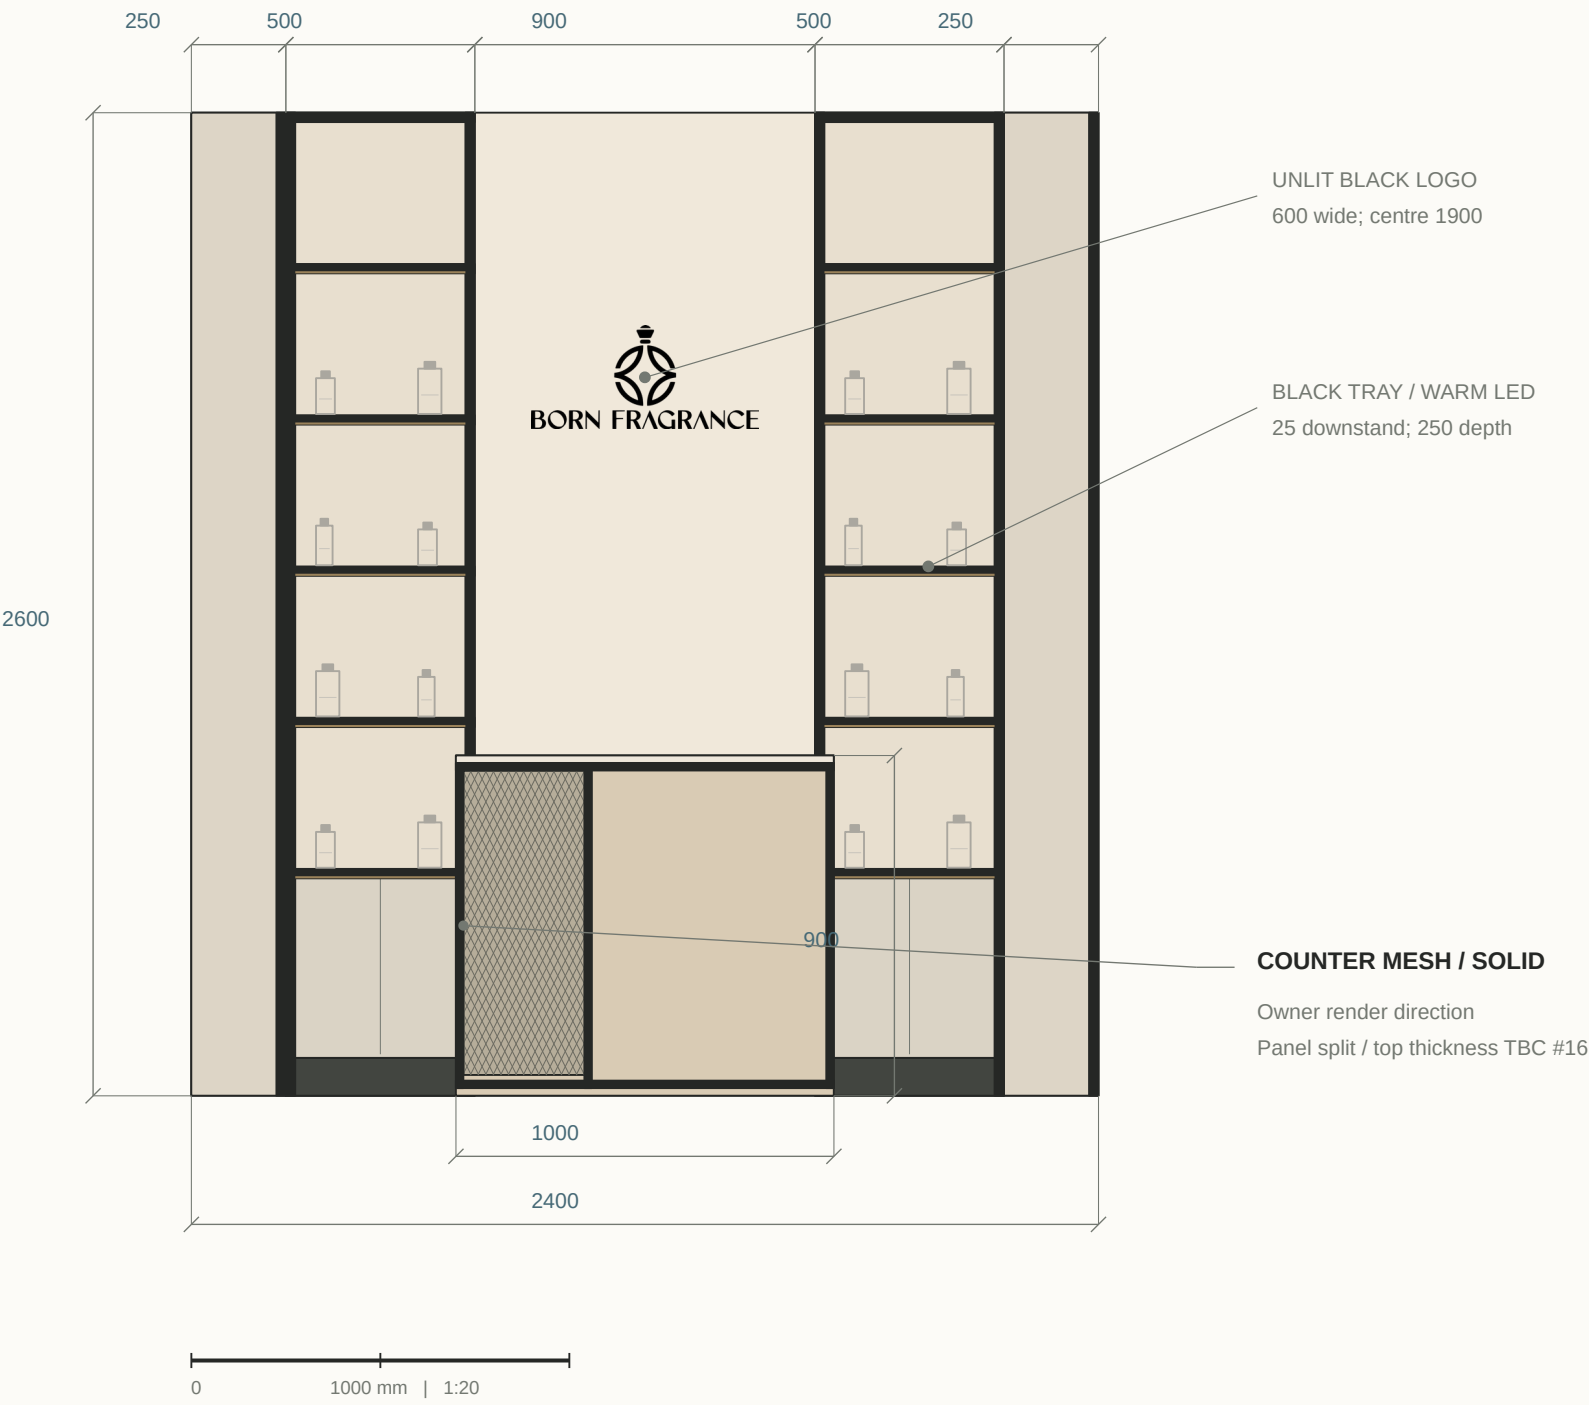


REAR SHELF / FRAME

SECTION 1:2

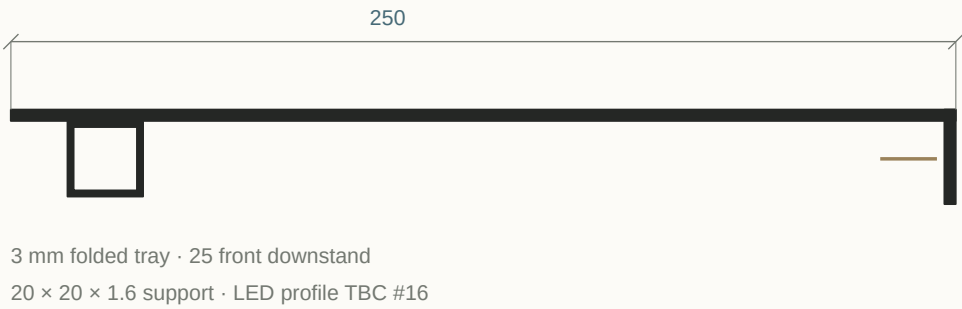

COUNTER / FOOTPRINT

PLAN 1:10

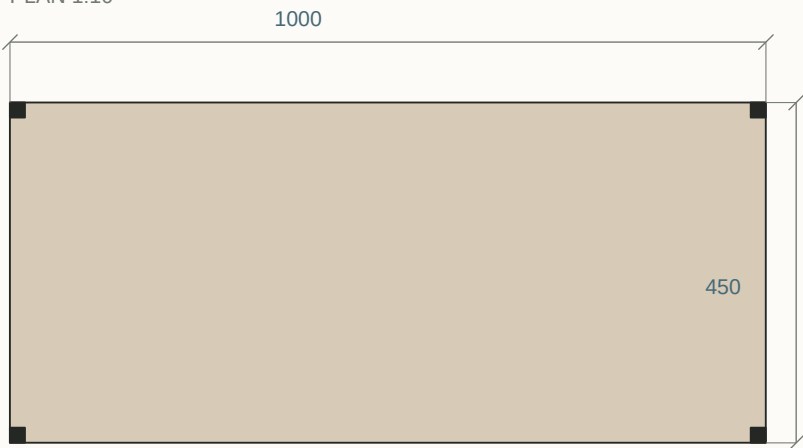


20 × 20 frame · front split TBC #16

Left display / internal elevation

Developed display elevation · interfaces + material codes · bottles indicative only

BLACK STEEL / NEUTRAL PPC / EXPANDED MESH / 3000 K LED

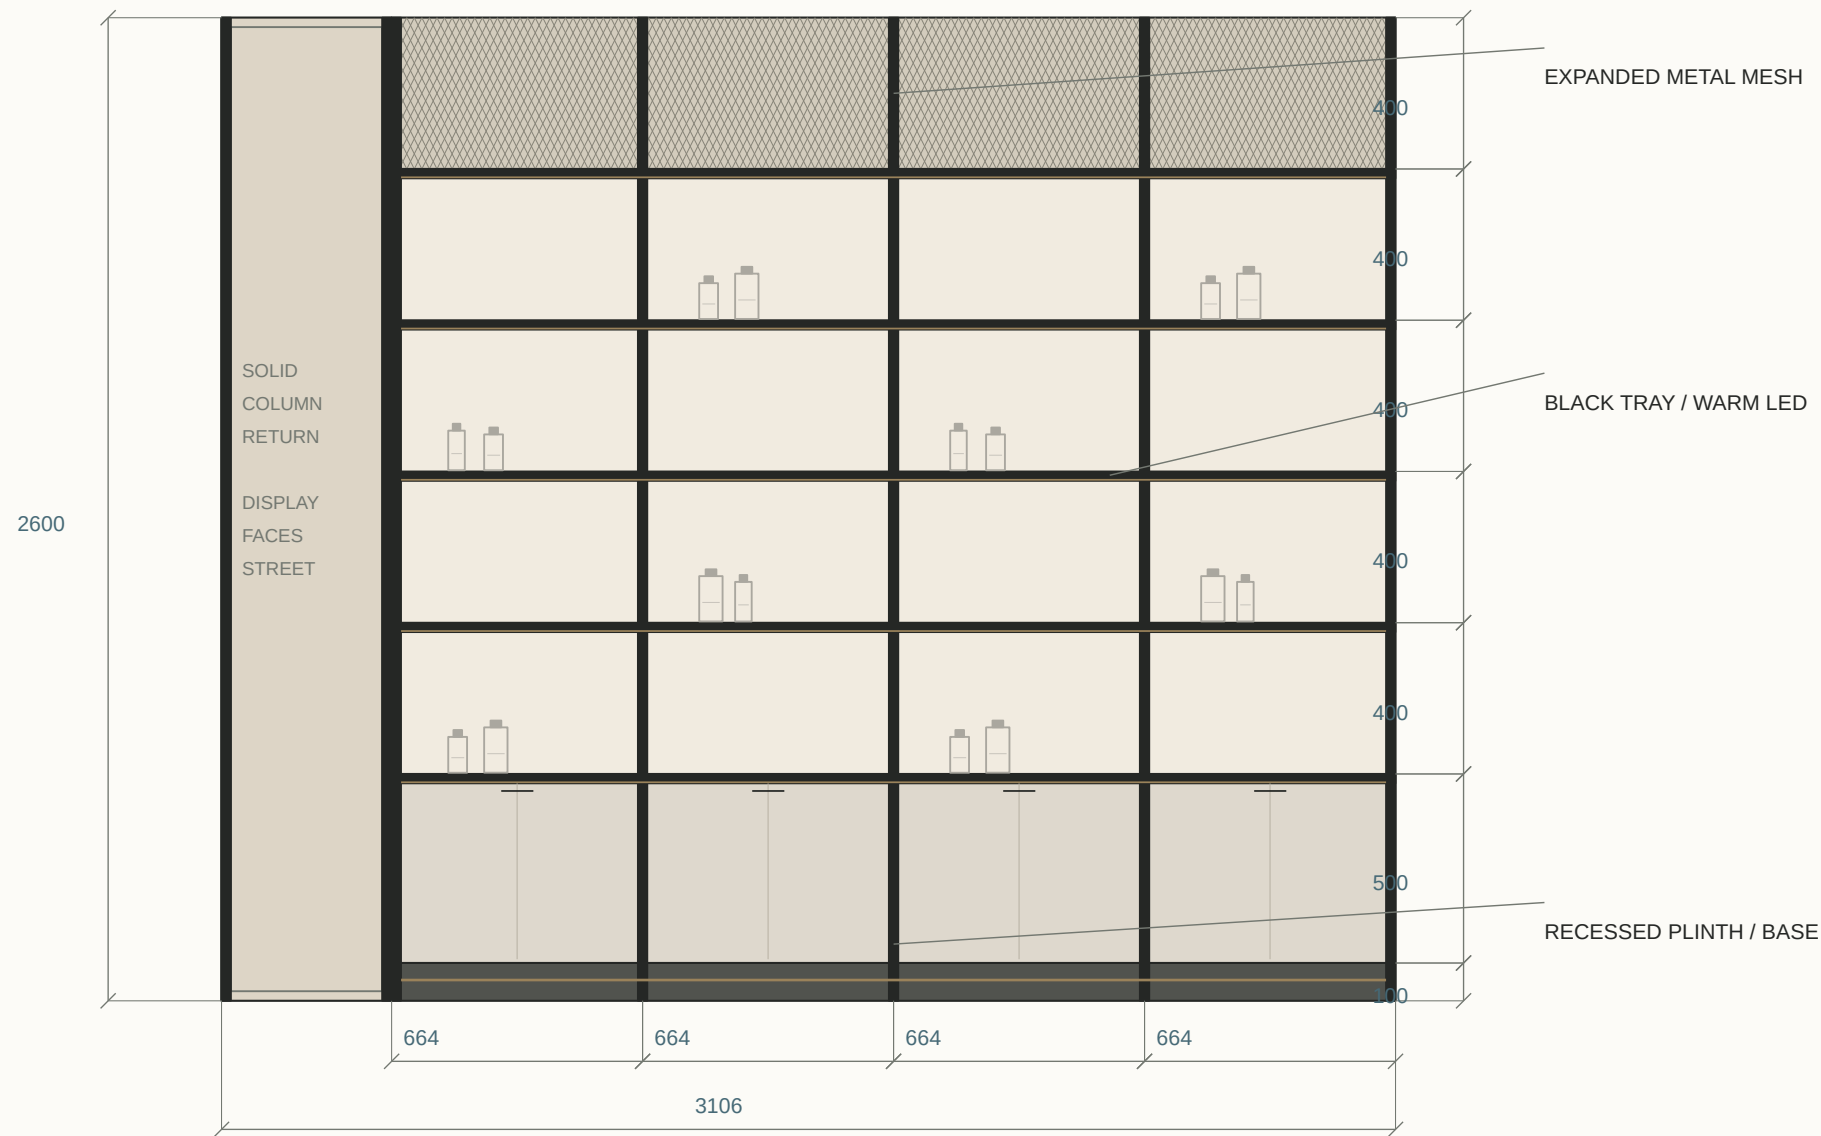


INDICATIVE BOTTLES · NOT A STOCK / CAPACITY SCHEDULE



SHELF / FRONT EDGE


SECTION 1:2

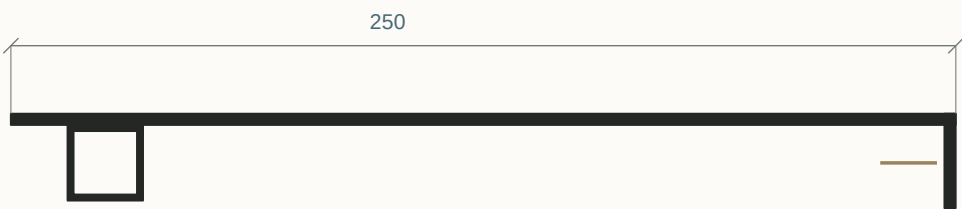

3 mm folded tray · 25 front downstand
20 × 20 × 1.6 support · LED profile TBC #16

CABINET / PLINTH

SECTION 1:5

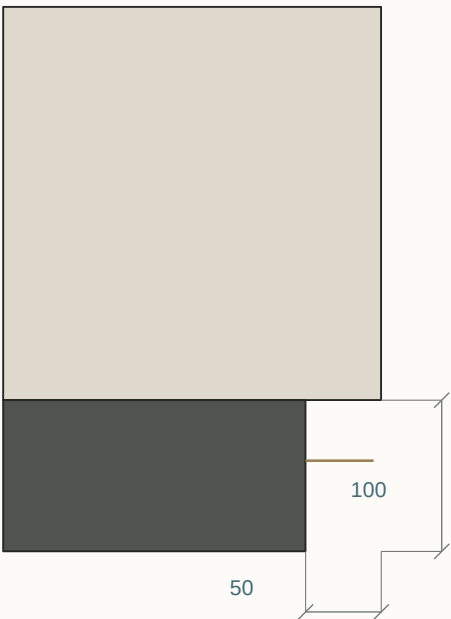


100 high · 50 recess · warm toe-kick LED


Right display / internal elevation

Developed display elevation · interfaces + material codes · bottles indicative only

BLACK STEEL / NEUTRAL PPC / EXPANDED MESH / 3000 K LED

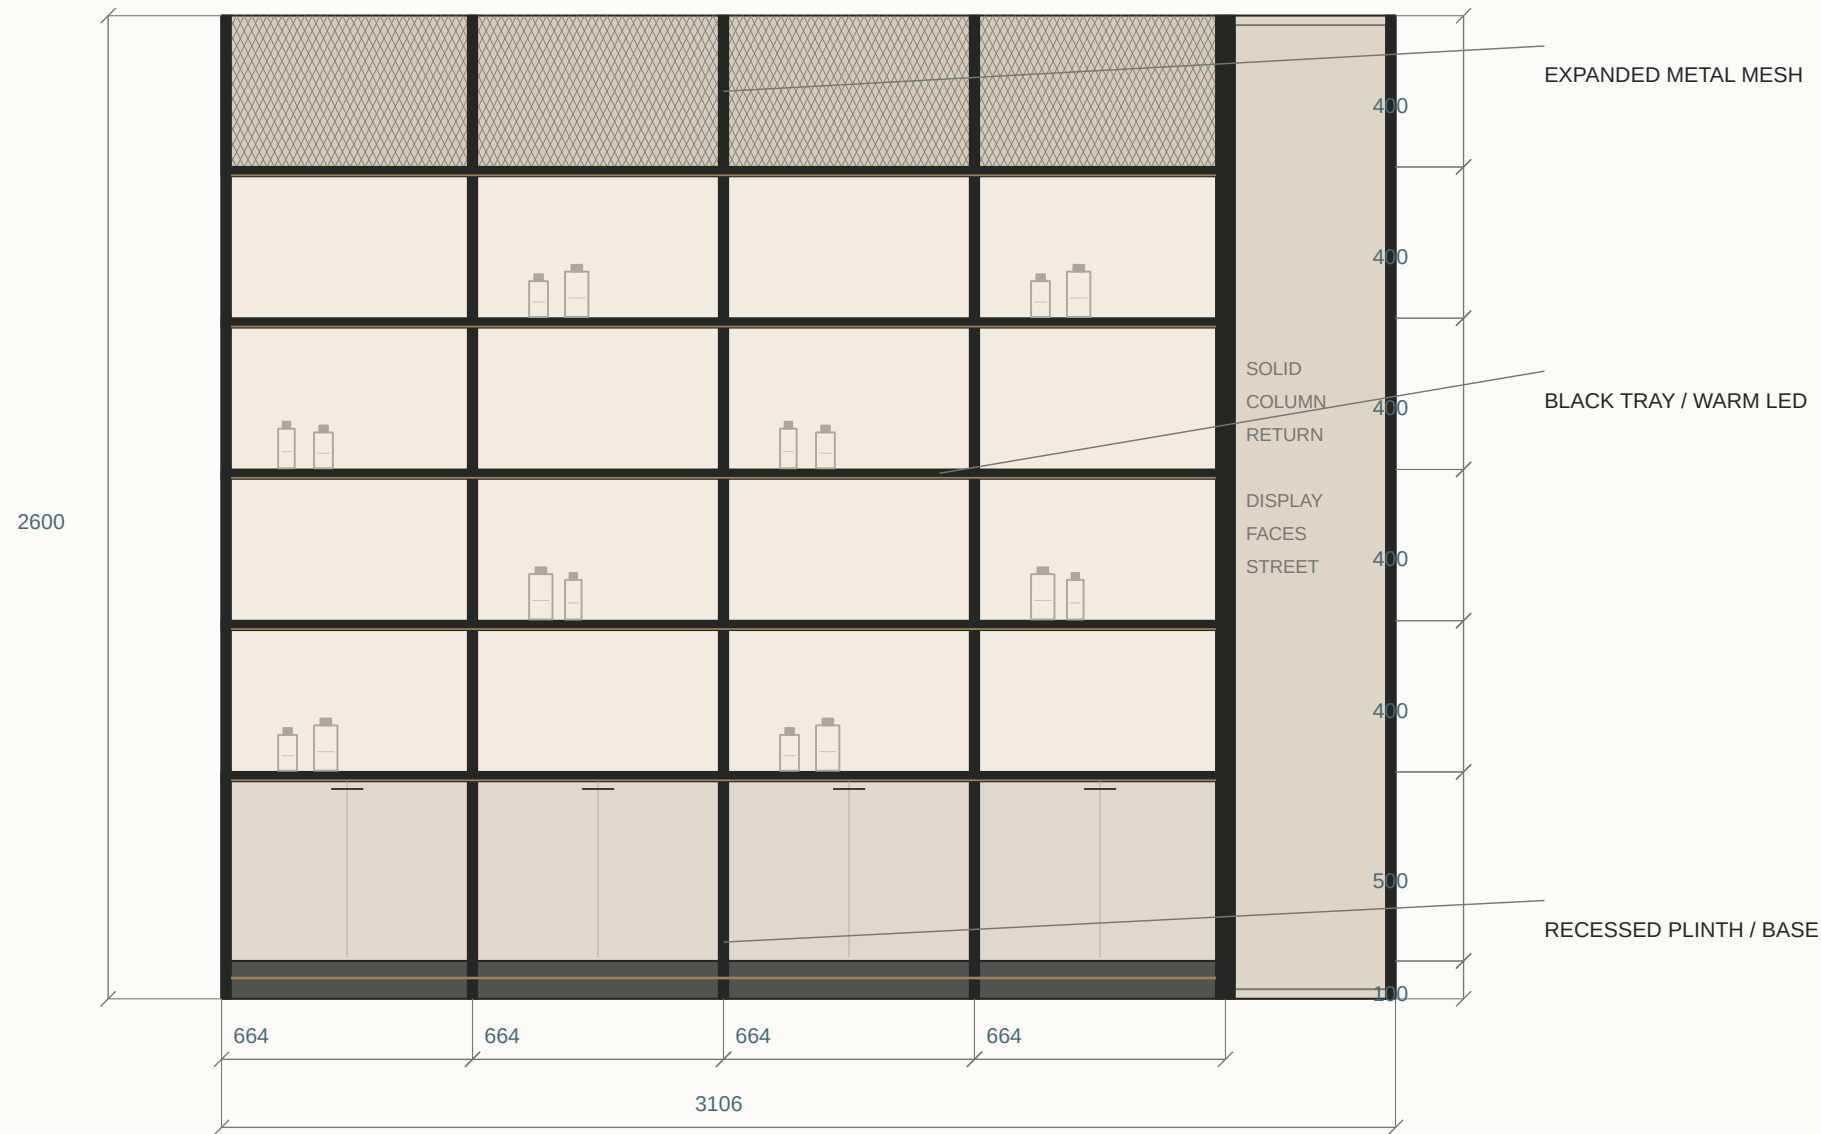


INDICATIVE BOTTLES · NOT A STOCK / CAPACITY SCHEDULE

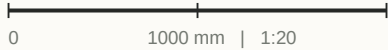

SHELF / FRONT EDGE


SECTION 1:2

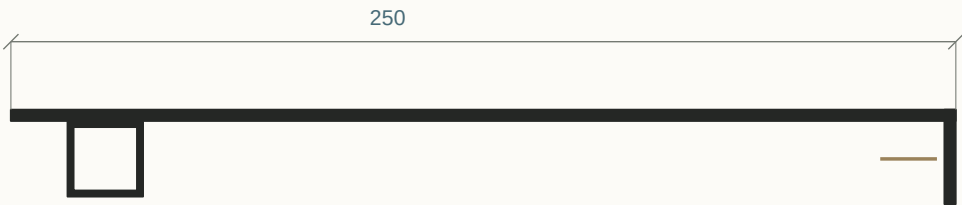

3 mm folded tray · 25 front downstand
20 × 20 × 1.6 support · LED profile TBC #16

CABINET / PLINTH

SECTION 1:5

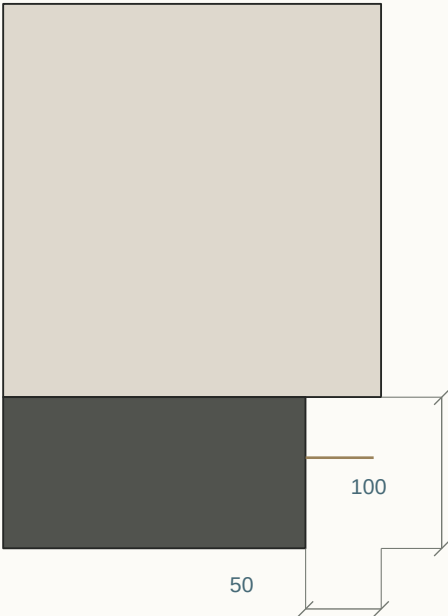

100 high · 50 recess · warm toe-kick LED

Spatial assembly / cutaway axonometric

Spatial cutaway · orthographic projection · direct material and interface annotations

EXPANDED MESH

Upper infill 2200–2600
Approx. 20 × 40 diamonds

BLACK STEEL TRAYS

250 depth · 3 mm steel
25 folded front downstand

NEUTRAL BASE DOORS

1.5 mm PPC steel
600 base incl. 100 plinth

STREET DISPLAY CUT

Upper column removed
1500 clear entrance

CEILING TRACKS

Exploded above room
Installed at 2600 · 3000 K
Two tracks / four spots each

REAR BRAND WALL

Raw light plaster
600-wide unlit native logo

COUNTER

1000 × 450 × 900
Mesh left / neutral panel right

NEAR-SIDE CUTAWAY

Upper joinery omitted at 600
Full run shown in elevations

