



LEGEND

- Display unit, 25x25x1.6 + 20x20x1.6 MS SHS, matte black powder coat, 250 deep (locked)
- Counter 1000x450x900H, 20x20 black frame, light panel + mesh insert, light top (locked)

Counter centred x 700-1700 is a PROPOSAL.
Side clearance 450 < 600: CHECK staff access.
Exclusions: no timber, brass, plants, products.



BAYS ~600, COUNT TBC #24*
BASE CAB TBC #7

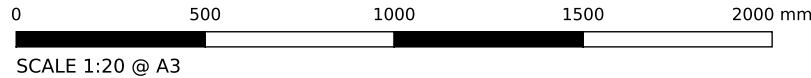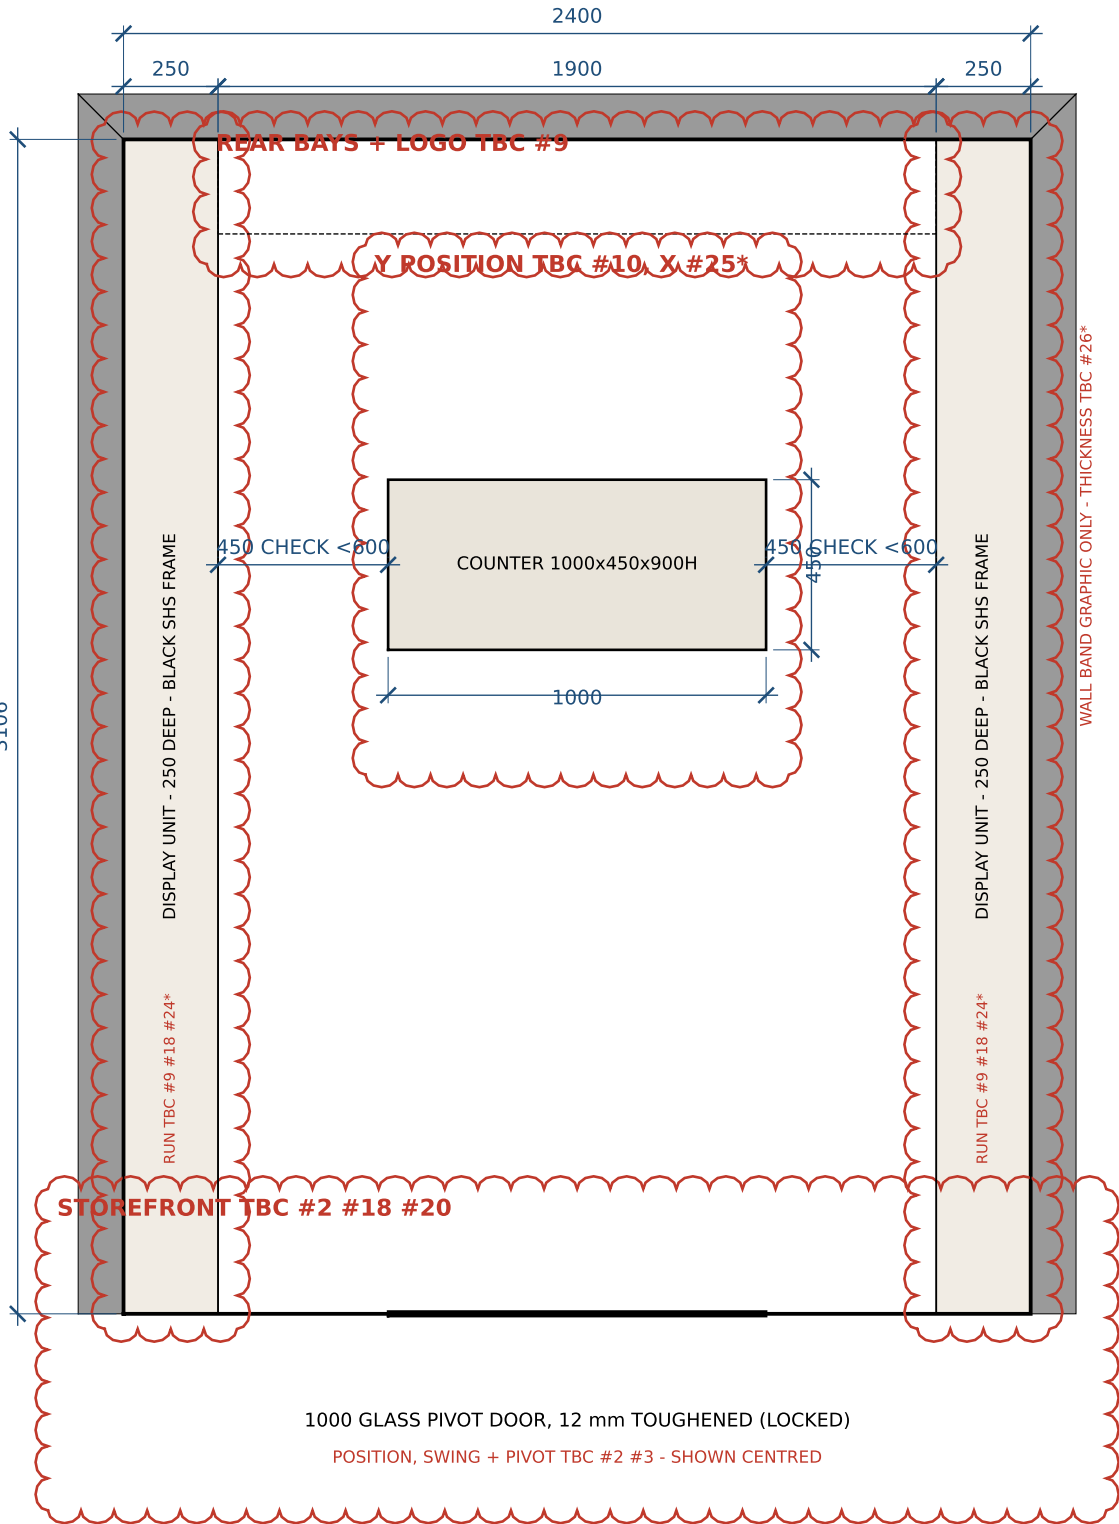

BORN FRAGRANCE

PROJECT BORN FRAGRANCE - shop fit-out

SHEET SD-02

TITLE DISPLAY / FURNITURE PLAN

SCALE 1:20 @ A3

DATE 2026-10-05

REV 00 - preliminary

SPEC spec/SHOP_SPEC.json @ e1fbc1c

DRAWN Claude Code (AI), for owner review

TBC ITEMS ON THIS SHEET

- #7 Base cabinet height and door type
- #9 Rear wall bay width, shelf count, logo size and height
- #10 Counter distance from rear wall and staff clearance
- #13 Floor-level LED strip (visible in render): keep or omit
- #18 Storefront display column depth, and shelf facing (street, shop or both)
- #24* Side bay count, widths and upright spacing
- #25* Counter lateral position (centring is a proposal)
- #4 Is 2400 x 3106 the finished size (after plaster)?

* proposed item, not yet in spec/TBC.md
TBC items are shown in revision clouds.
Dimensions computed from SHOP_SPEC.json.
Do not scale from the render.

PRELIMINARY - NOT FOR CONSTRUCTION