

FLOOR: 1200x600 RECTIFIED STONE-LOOK PORCELAIN

2 mm grout. Joints between tiles only;
perimeter/movement joint TBC #26*.

OPTION A (drawn): 1200 across




across: 0 full + 2 x 1199
depth: 4 full + 2 x 348

OPTION B: 1200 along depth

across: 2 full + 2 x 597
depth: 1 full + 2 x 951

Owner to choose A or B (TBC #22).
Threshold / level change TBC #20.

TILE UNDER
UNITS TBC #14

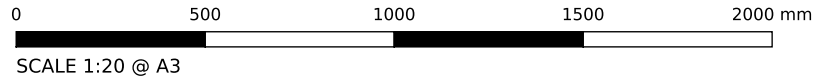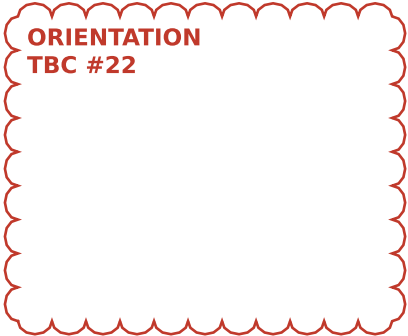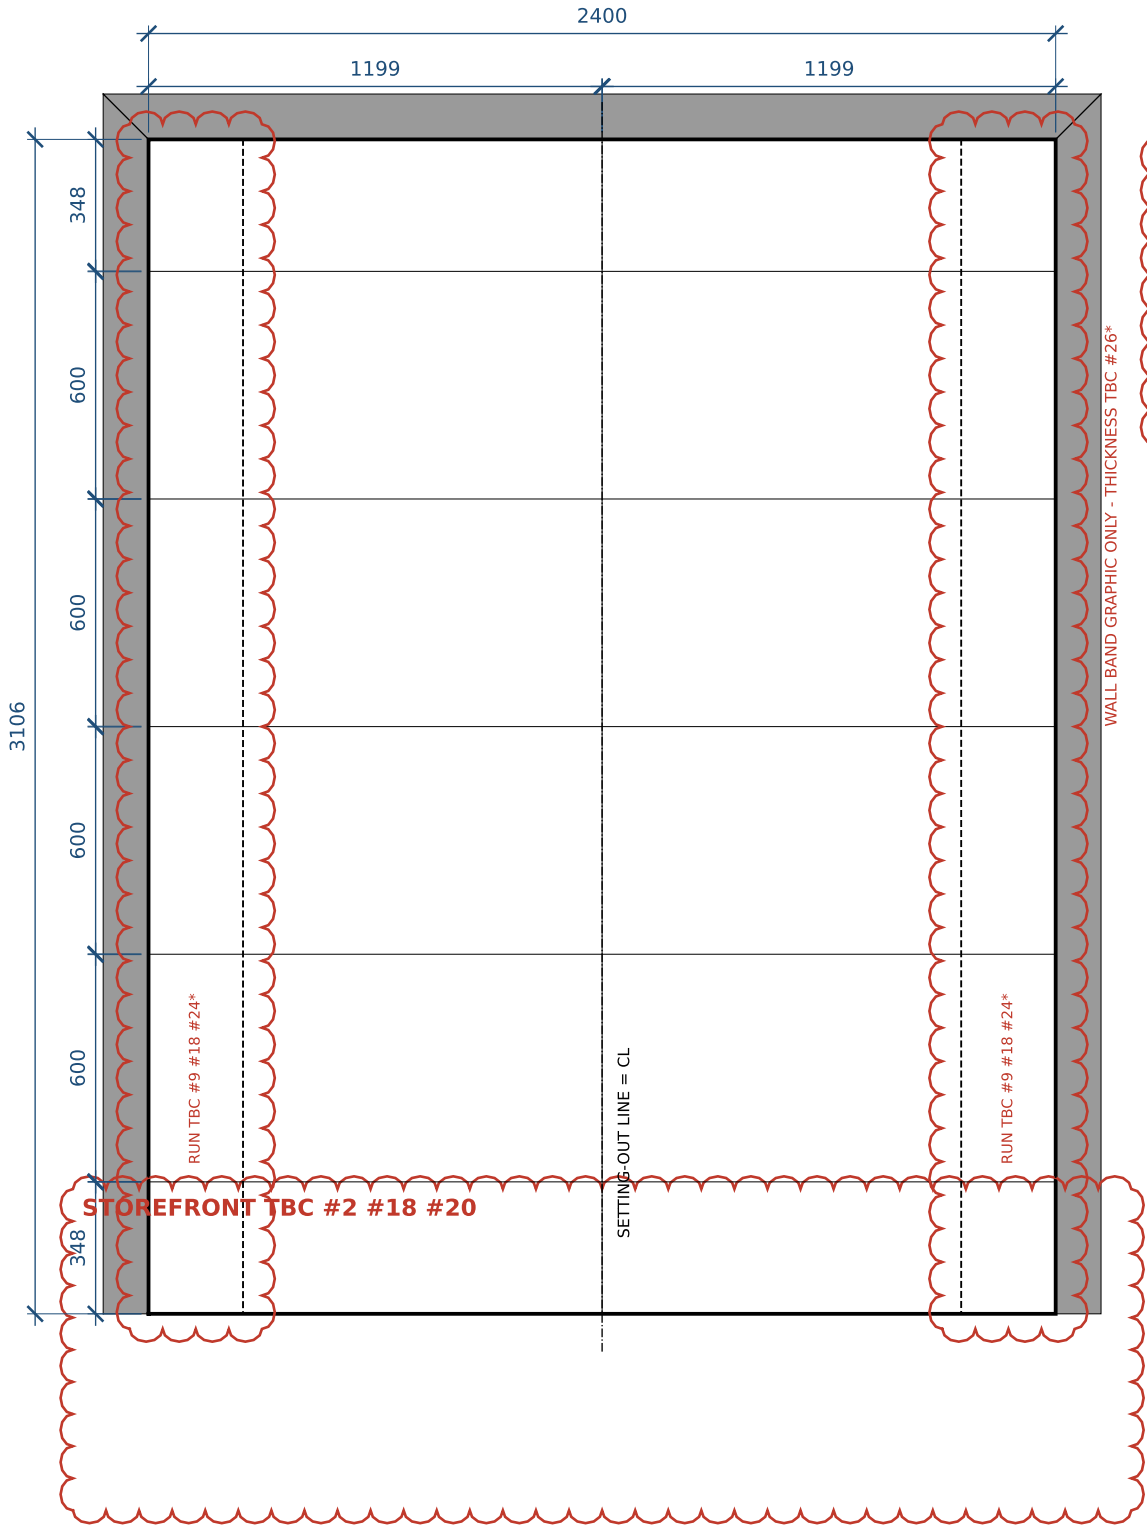

BORN FRAGRANCE

PROJECT BORN FRAGRANCE - shop fit-out

SHEET SD-03

TITLE FLOOR FINISH PLAN

SCALE 1:20 @ A3

DATE 2026-10-05

REV 00 - preliminary

SPEC spec/SHOP_SPEC.json @ e1fbc1c

DRAWN Claude Code (AI), for owner review

TBC ITEMS ON THIS SHEET

- #22 Floor tile orientation (1200 across or along), and cut sizes allowing for 2 mm grout (2 x 1200 + joint = 2402 > 2400; depth cuts approx 348, not 353)
- #14 Floor tile extent under display units
- #20 Entrance threshold / step and any floor level change
- #4 Is 2400 x 3106 the finished size (after plaster)?
- #26* Vertical datum (FFL) and wall thickness / construction

* proposed item, not yet in spec/TBC.md
TBC items are shown in revision clouds.
Dimensions computed from SHOP_SPEC.json.
Do not scale from the render.
PRELIMINARY - NOT FOR CONSTRUCTION