



Retail interior / coordinated design

Design intent, measured geometry and assembly strategies

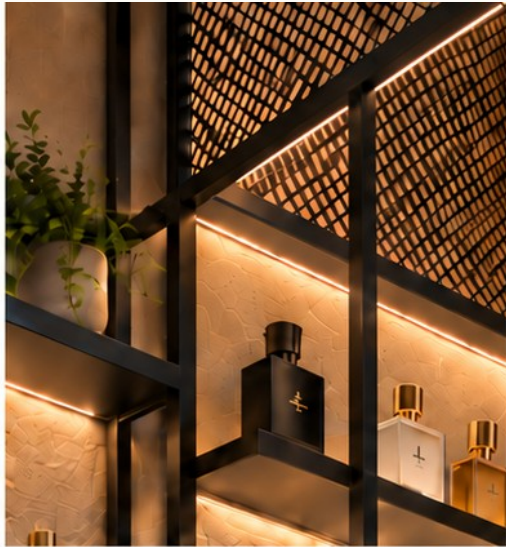


RAW PLASTER
WALL FINISH

BLACK METAL
SHELF

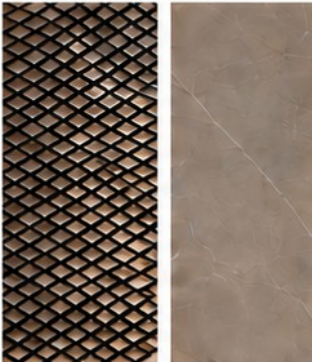

METAL MESH
PANEL

STONE LOOK
FLOOR TILE

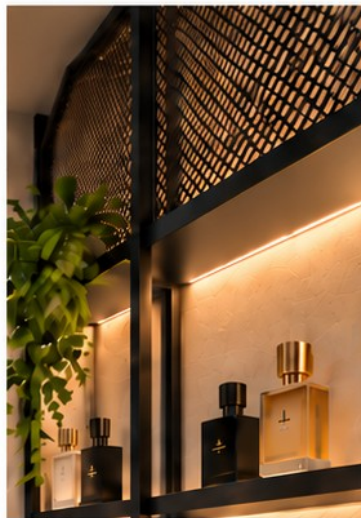

PROJECT

2400 × 3106 internal
2600 ceiling
Black steel / plaster / stone-look floor

ISSUE PURPOSE

Client review and consultant coordination. Detailed strategies are preliminary pending the stated confirmations.

DRAWING PRIORITY

Geometry follows approved Rev A. Render conveys material and lighting character only.

READING SEQUENCE

Layout → elevations → materials → assembly details → coordination decisions.

REFERENCE RENDER · NOT TO SCALE · styling props excluded from technical scope

Overall plan / setting-out


Setting-out / coordinated interfaces · 1:20 · finish-face dimensions; site verification pending

SET-OUT DATUMS

- A 0 / 0
- B 2400 / 0
- C 2400 / 3106
- D 0 / 3106

STREET-FACING DISPLAY
Dashed line: shelf above
Solid return toward interior

Wall bands graphic only
Thickness TBC #26
Envelope TBC #4

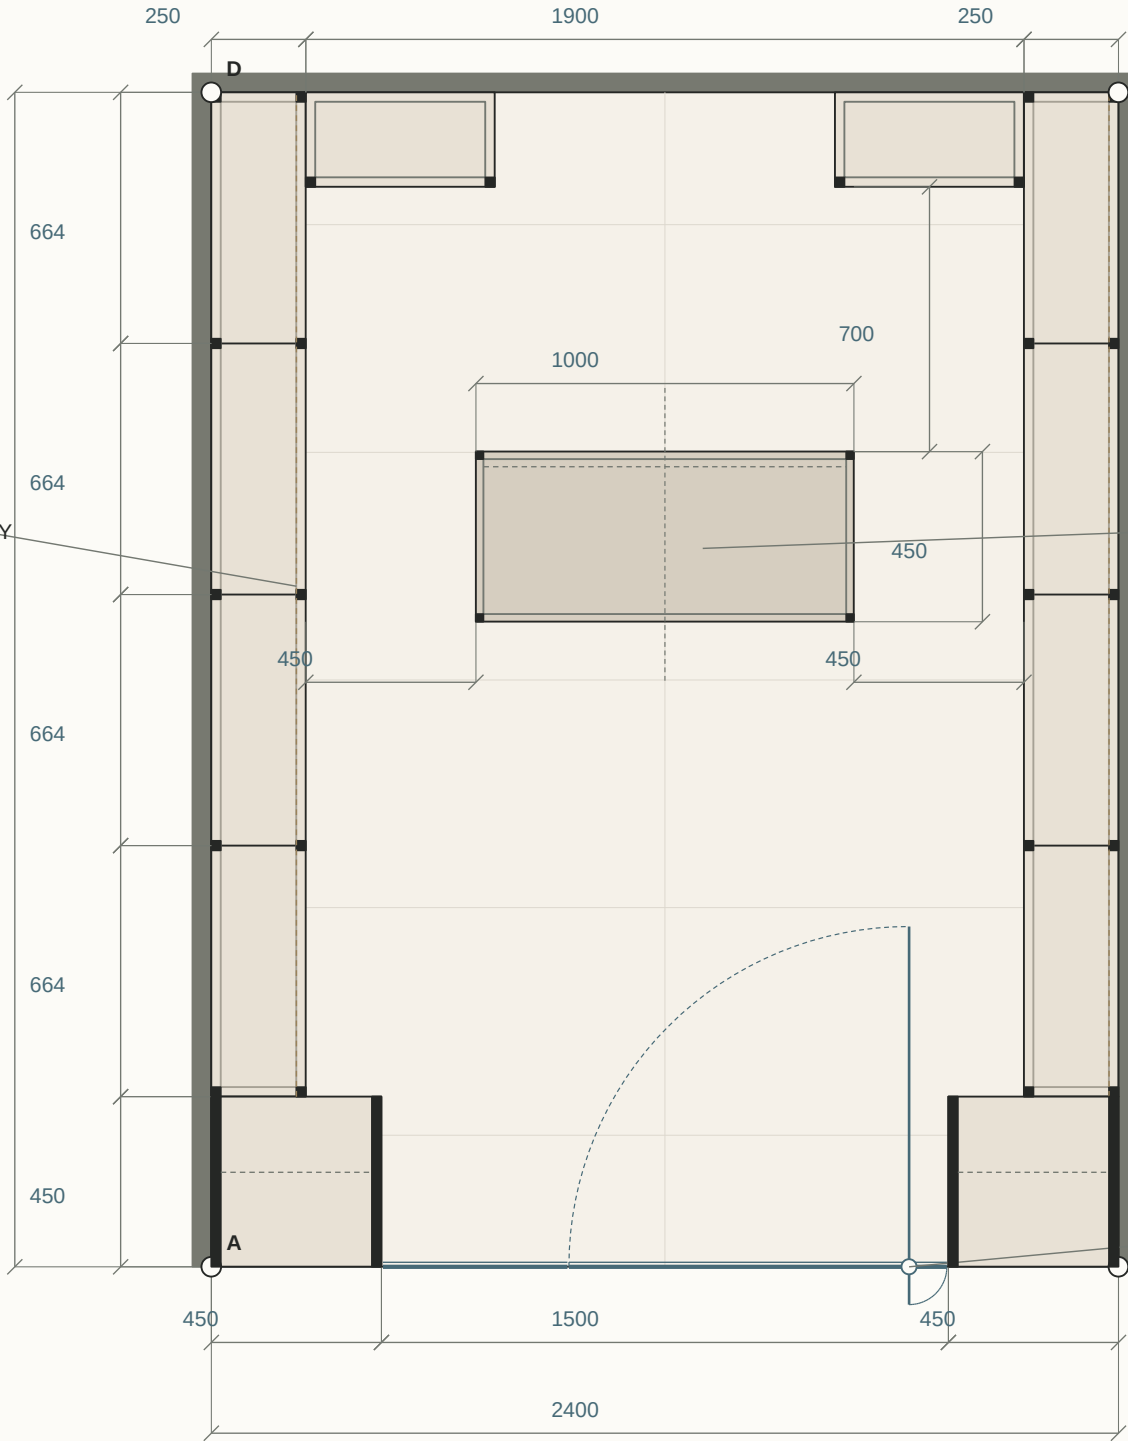

N ↓ STOREFRONT
ASSUMED #23

COUNTER FRAME
20 × 20 black steel

1000 × 450 COUNTER

#16
450 side routes
Access / escape unresolved

PIVOT GLASS DOOR

FRAME + SETTING-OUT

250 deep side units. Four 664 modules from y=450 to 3106. 25 main uprights shown; shelf/support lines distinguished.

COUNTER + REAR

1000 × 450 counter; x=700–1700, y=1706–2156. 700 to rear-unit face. Side routes remain 450 / 450.

GLAZED ENTRANCE


488 fixed pane + 1000 pivot leaf + three 4 gaps = 1500. Pivot 100 from right edge; inward sweep shown.

COORDINATION STATUS

LOD 350 development target: interfaces shown, not certified complete. Anchors, hardware, substrate and access remain TBC #16/#26.

Ceiling / lighting coordination

Reflected ceiling plan · lighting, display footprints and dimensional coordination

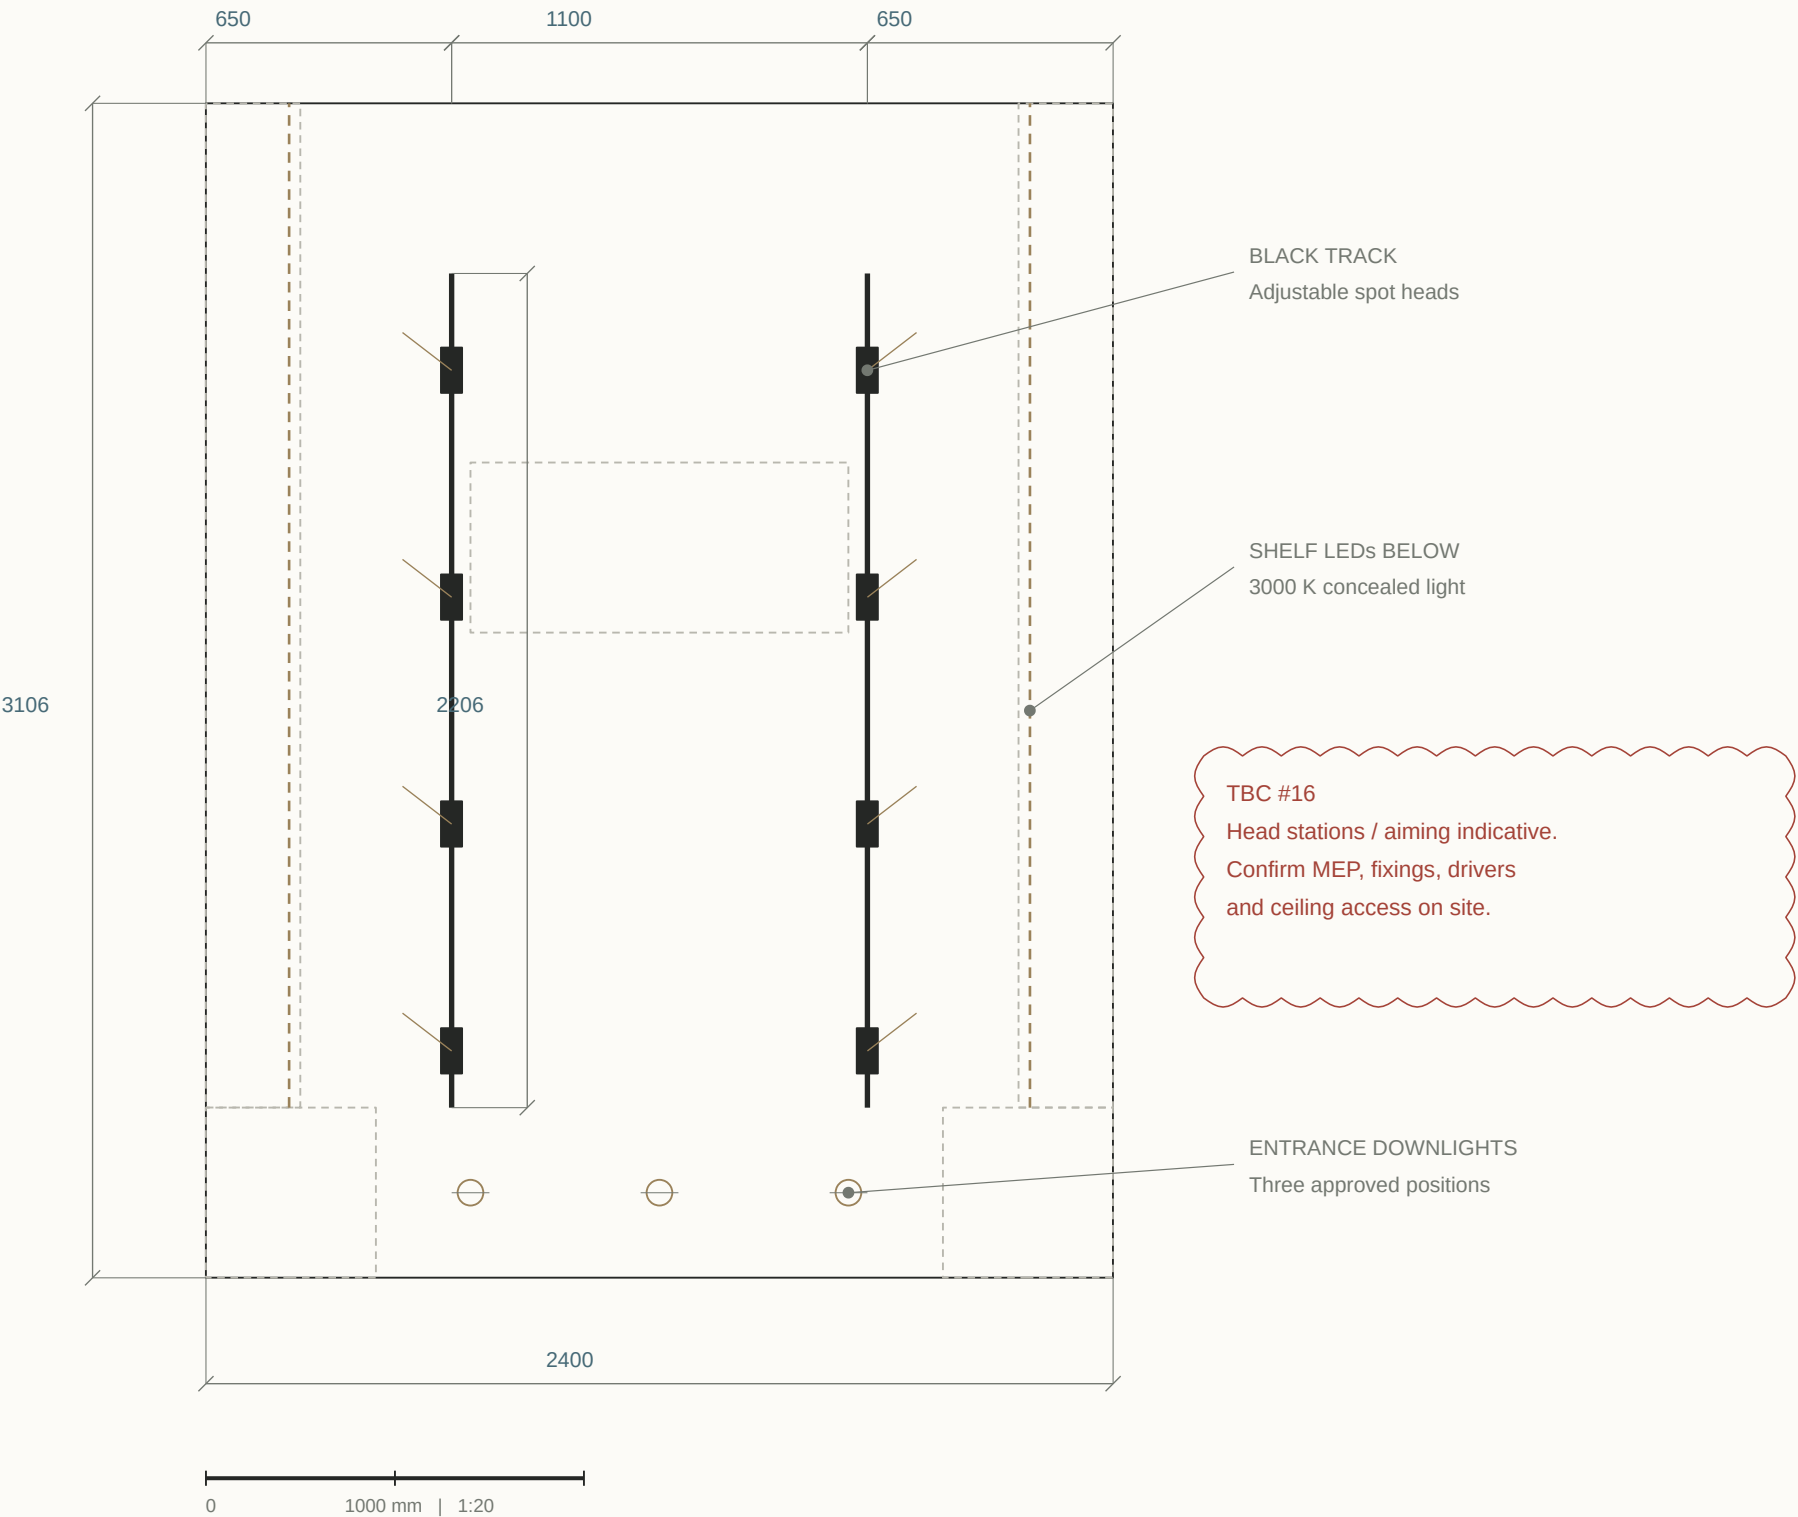

TRACK LIGHTING

Two matte-black tracks, four cylindrical adjustable heads each. 3000 K. Track coordinates dimensioned directly.

ENTRANCE DOWNLIGHTS

Three downlights at x=700 / 1200 / 1700; y=225. Symbol sizes indicative, not cut-out sizes.

DISPLAY LIGHTING


Concealed LEDs beneath shelves, and two 2656-long plinth runs. Dashed joinery footprint coordinates the ceiling with displays below.

CEILING / SERVICES

Warm off-white gypsum at 2600. No invented fire devices, wiring circuits or access panels. Consultant to coordinate under TBC #16.

Storefront / external elevation

Developed storefront · street-facing displays, glazed entrance and halo-lit brand

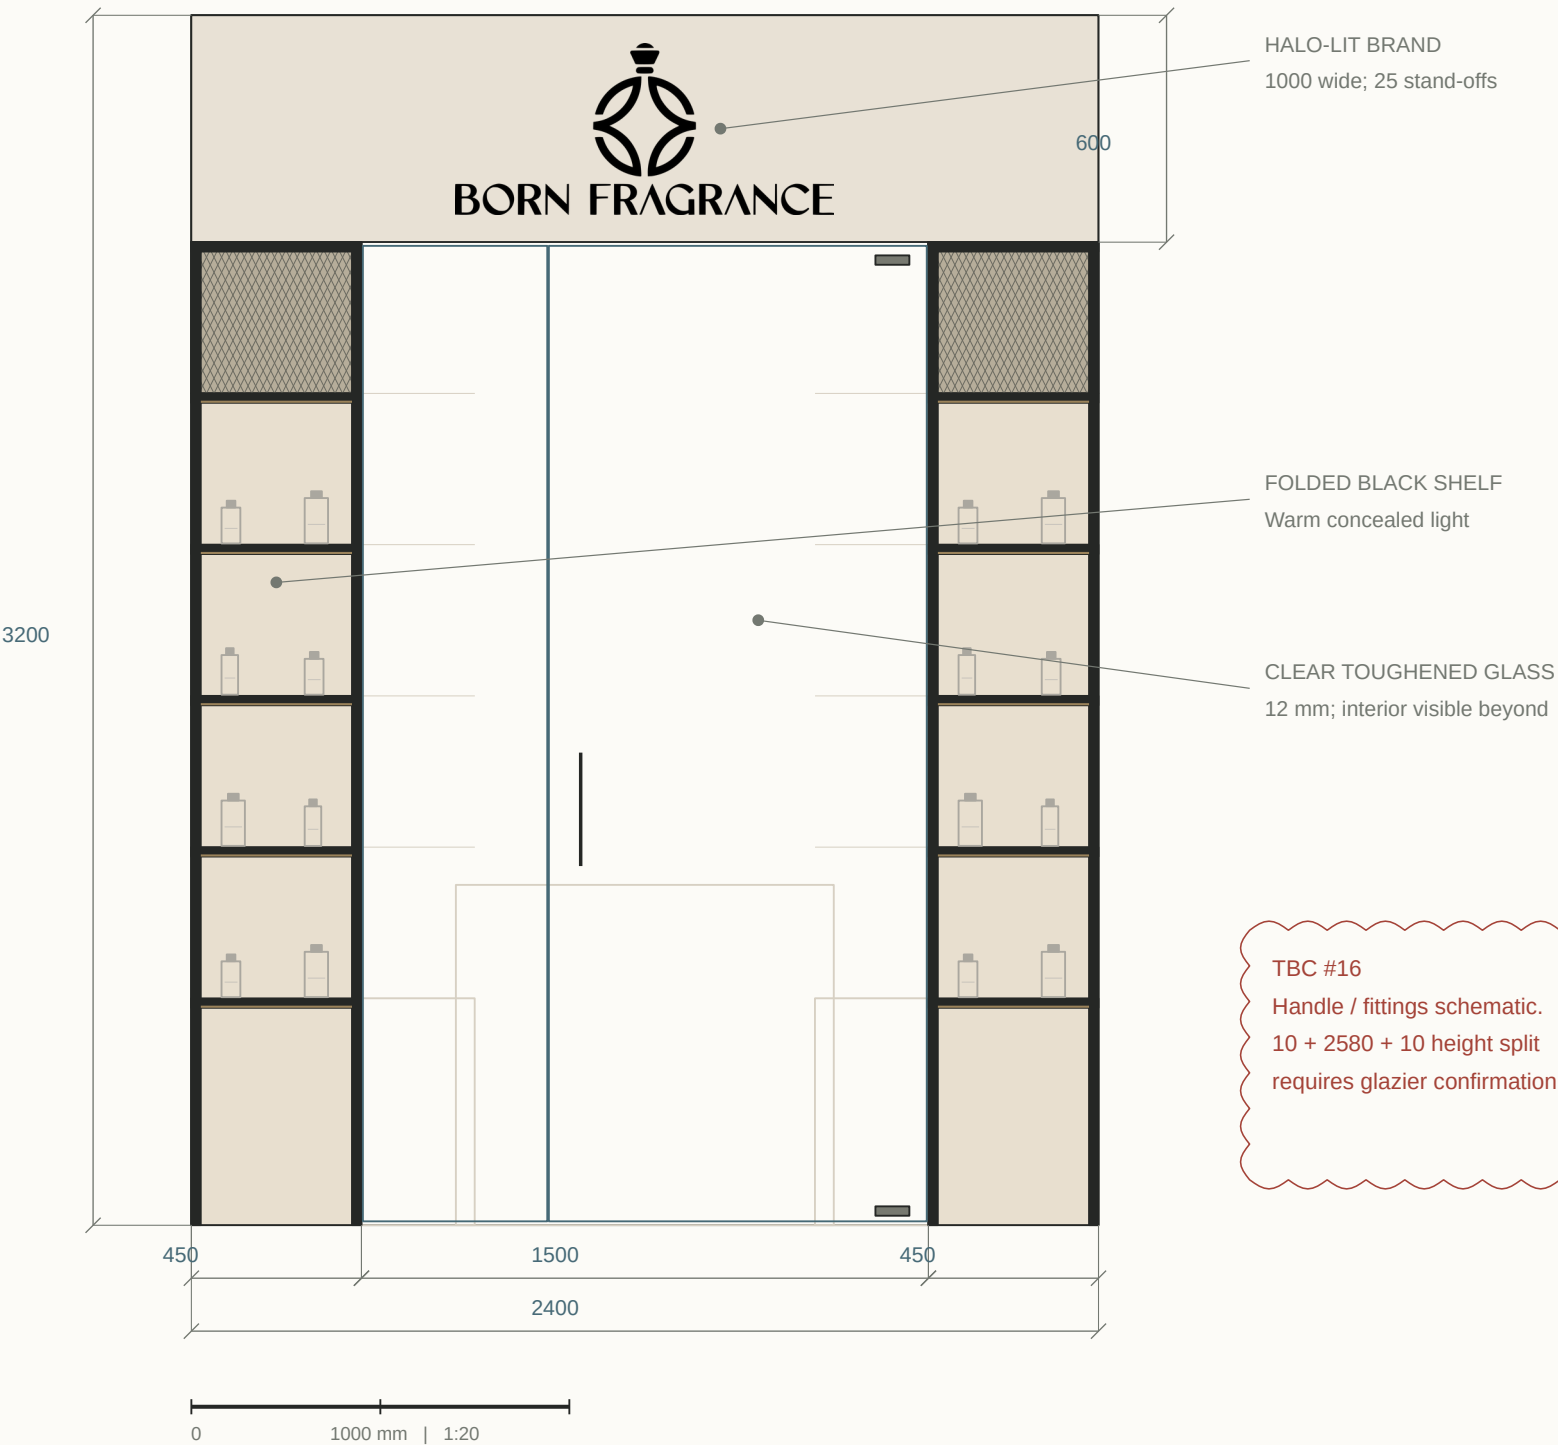

DISPLAY COLUMNS

450 wide, 450 deep; shelf depth 250. Black frame and folded trays; warm concealed LEDs. Bottles indicate use only.

CLEAR GLASS ENTRANCE

488 fixed pane, 1000 pivot leaf; 12 toughened glass. Faint rear joinery is visible through glass, not applied to it.

BRANDING / FINISH


600-high plaster fascia. 1000-wide native logo; black halo-lit letters on 25 stand-offs. Supports remain TBC #16.

GLAZING COORDINATION

Door fittings are indicative only. Handle, pivots, patch fittings, structural support and glass procurement require supplier confirmation.

Rear focal wall / internal elevation

Rear focal wall · developed shelving + owner-directed counter front

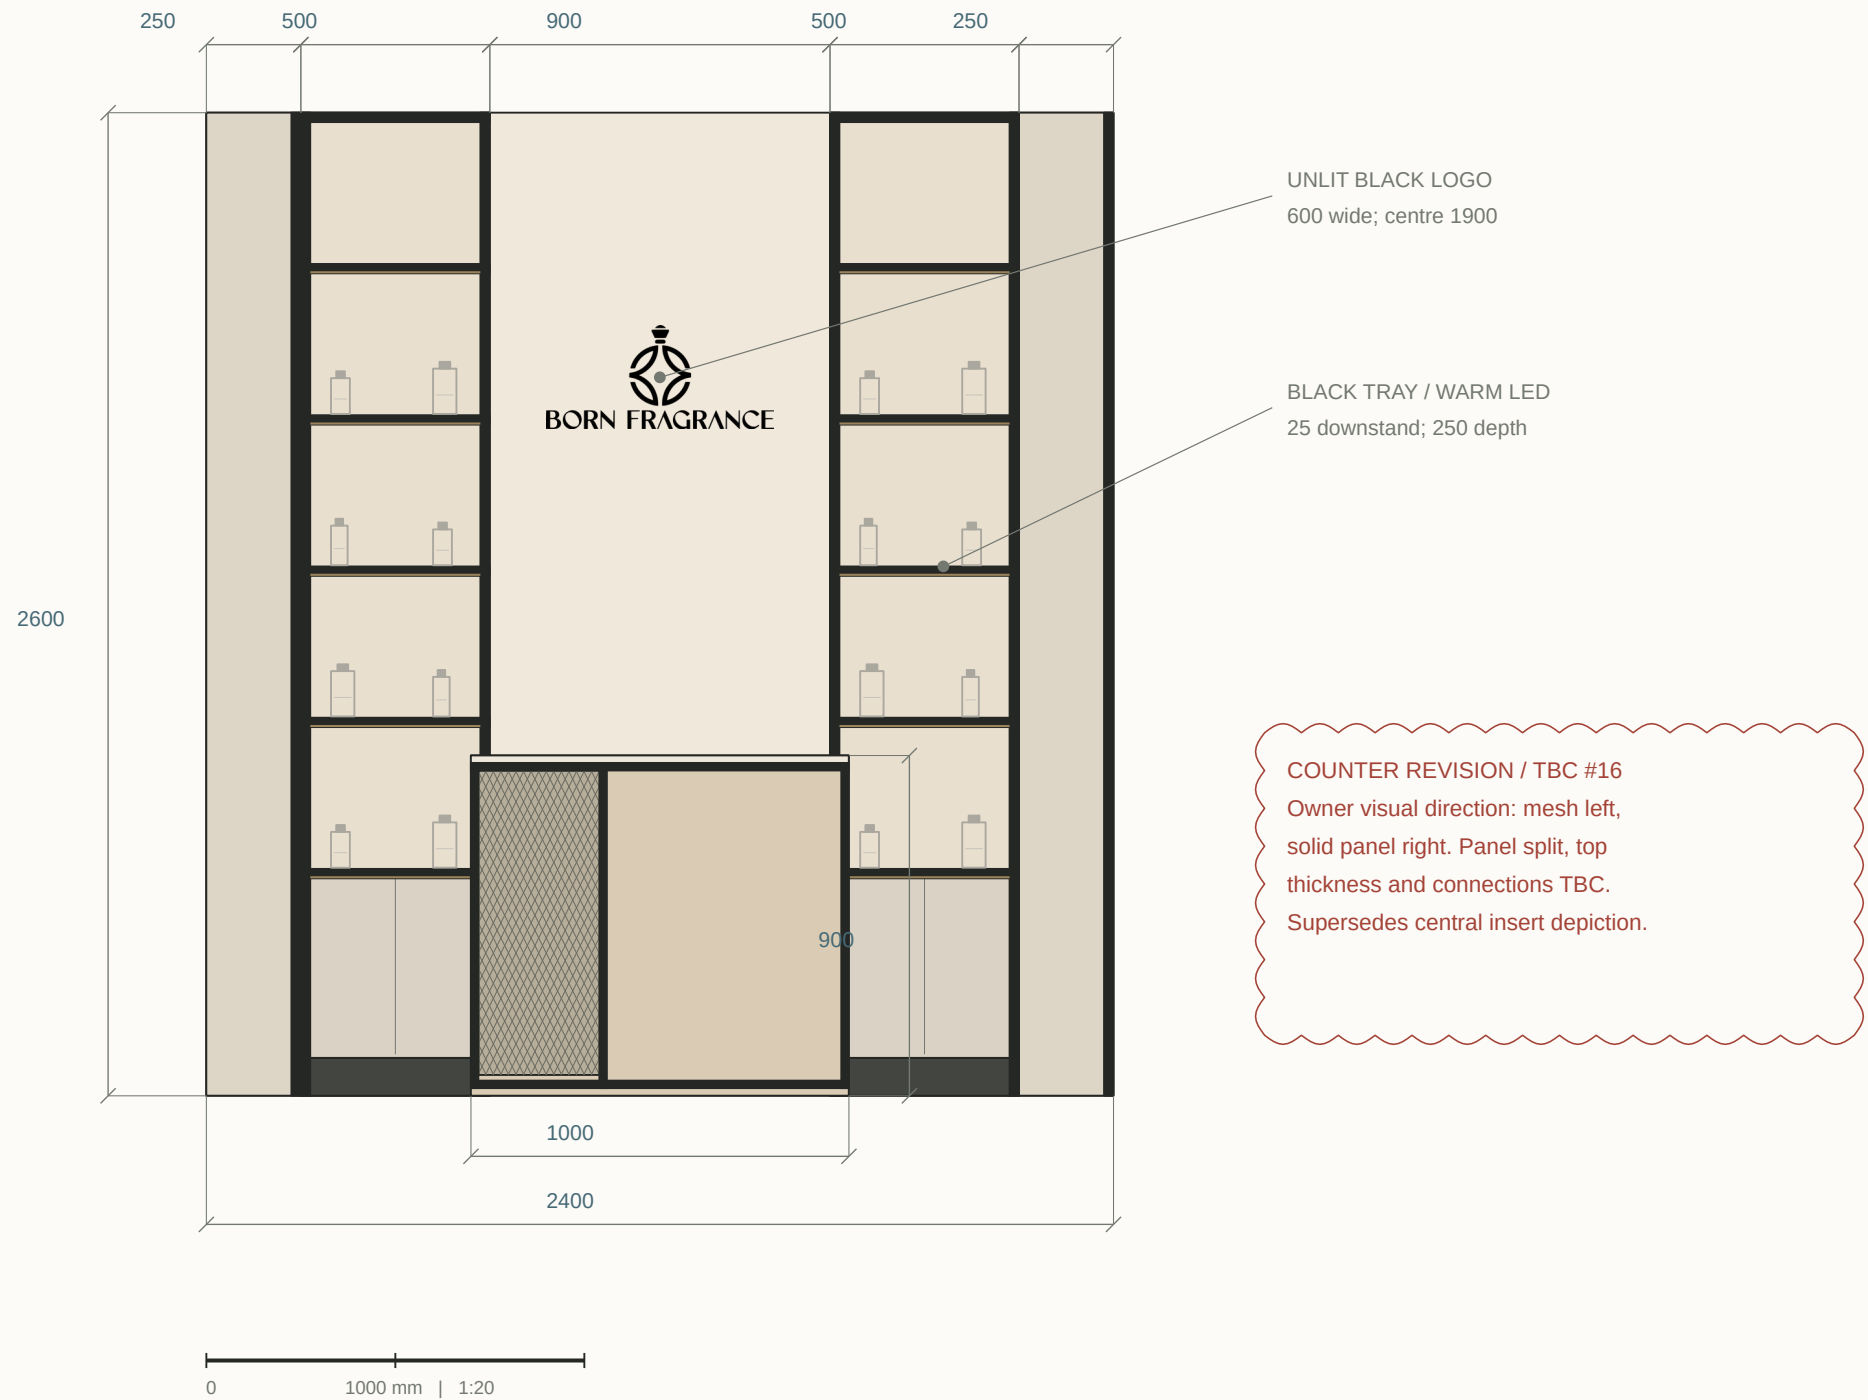

REAR DISPLAY

500 / 900 / 500 zones between side units. 25 main posts, 3 mm folded trays, 25 downstands and warm concealed LEDs. No rear mesh.

COUNTER / RENDER DIRECTION

Left mesh panel, larger light-neutral right panel, light top and black perimeter frame. Replaces the small central mesh graphic at owner request.

DIMENSIONS RETAINED

Counter 1000 × 450 × 900 high, 20 × 20 black frame. Location and 450 side gaps unchanged. Revised front panel split is not a cutting schedule.


BRAND / FINISH

600-wide native black logo, centre 1900 AFFL, unlit. Raw light plaster backdrop. Product silhouettes indicative only.

Left display / internal elevation

Developed display elevation · interfaces + material codes · bottles indicative only

BLACK STEEL / NEUTRAL PPC / EXPANDED MESH / 3000 K LED

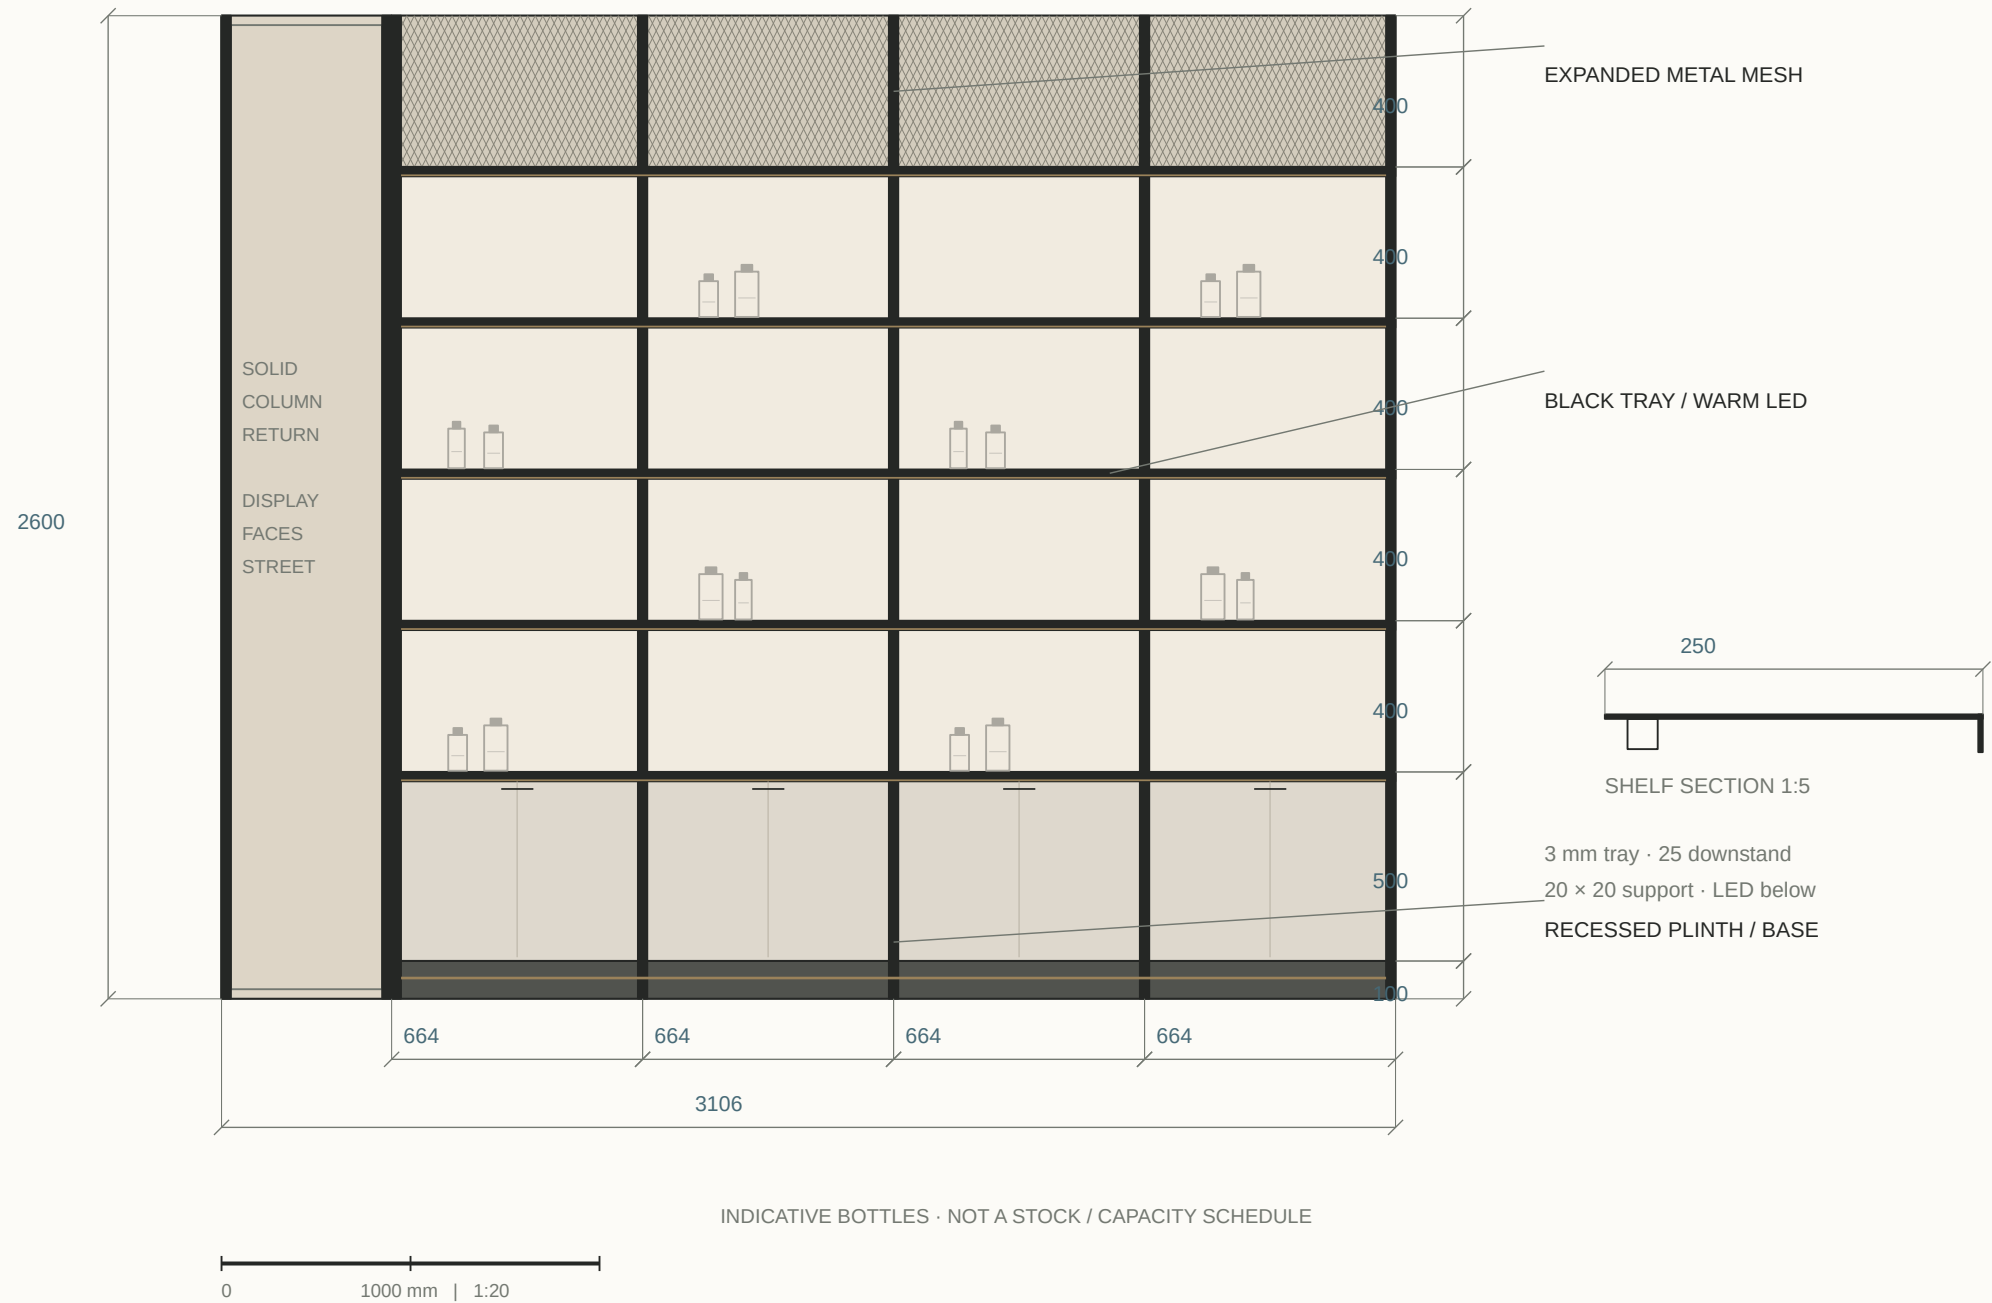

STEEL FRAME

25 × 25 × 1.6 main SHS; 20 × 20 × 1.6 secondary supports.
664 module is not a fabrication cut size.

SHELF + LIGHT

3 mm tray / 25 downstand / 250 depth. Concealed 3000 K LED
behind front edge; see section inset.

BASE + MESH

600 base includes 100 recessed plinth. 1.5 PPC doors. Mesh
at 2200–2600; approximate 20 × 40 diamonds.


INDICATIVE CONTENT

Fragrance silhouettes show scale and use. Fixings and cable
routing #16 remain open. The solid column return has street-
facing displays around the corner.

Right display / internal elevation

Developed display elevation · interfaces + material codes · bottles indicative only

BLACK STEEL / NEUTRAL PPC / EXPANDED MESH / 3000 K LED

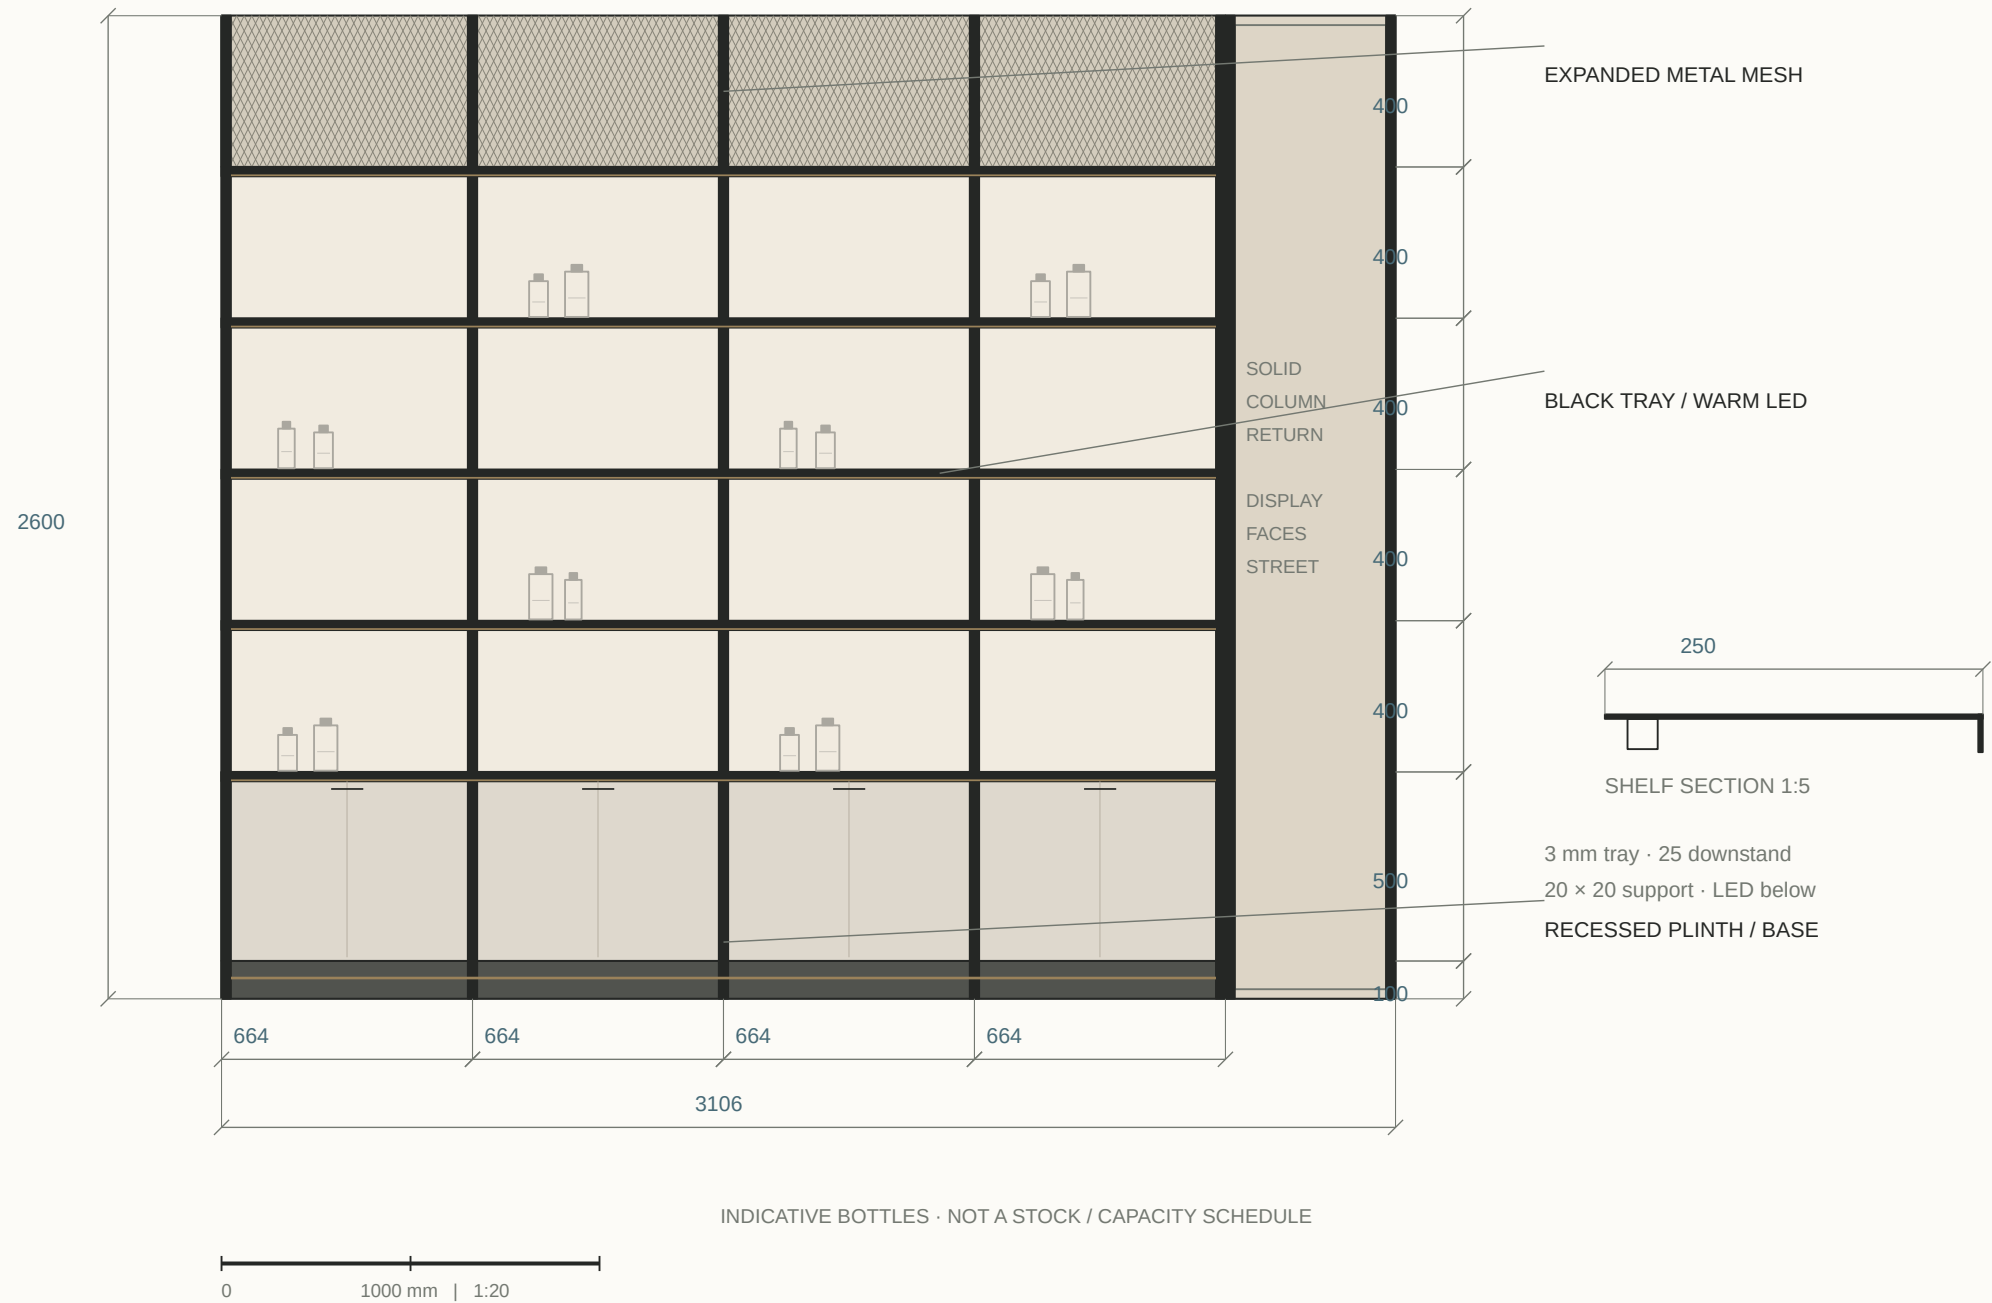

STEEL FRAME

25 × 25 × 1.6 main SHS; 20 × 20 × 1.6 secondary supports.
664 module is not a fabrication cut size.

SHELF + LIGHT

3 mm tray / 25 downstand / 250 depth. Concealed 3000 K LED
behind front edge; see section inset.

BASE + MESH


600 base includes 100 recessed plinth. 1.5 PPC doors. Mesh
at 2200–2600; approximate 20 × 40 diamonds.

INDICATIVE CONTENT

Fragrance silhouettes show scale and use. Fixings and cable
routing #16 remain open. The solid column return has street-
facing displays around the corner.

Spatial assembly / cutaway axonometric

Shaded cutaway / approved geometry + render material language · near wall and ceiling removed

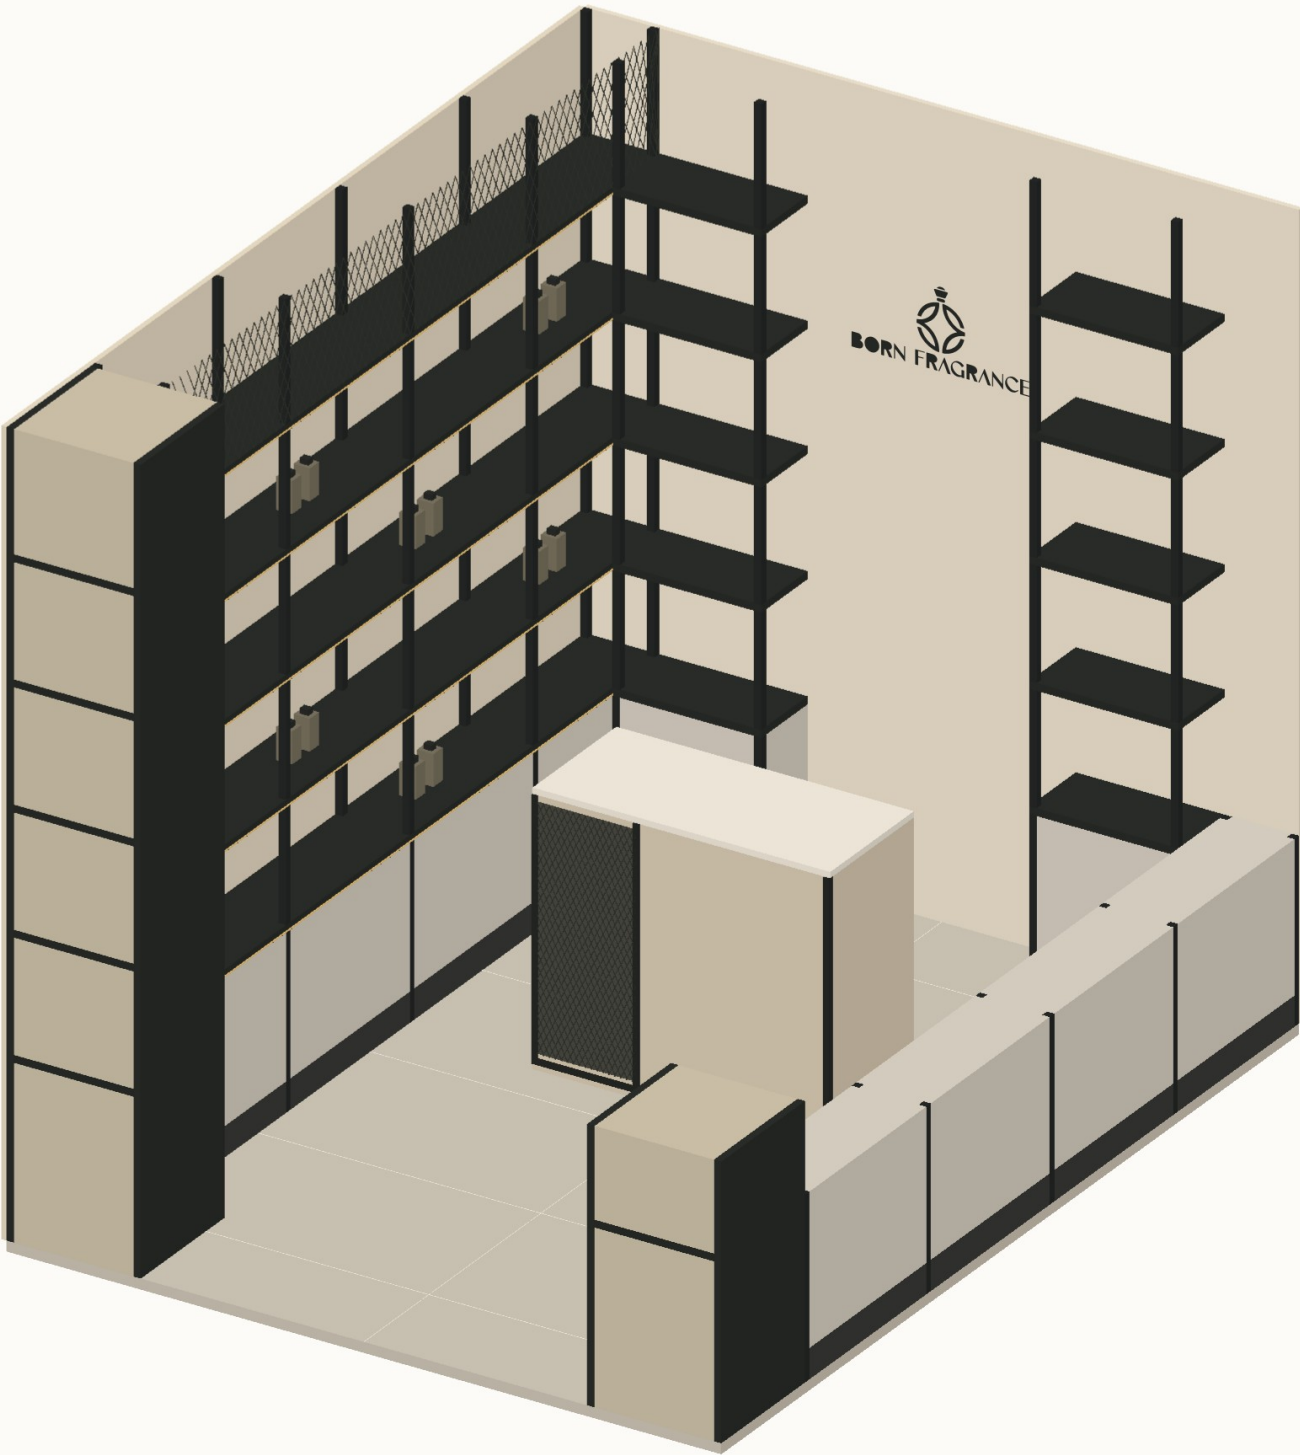

CUTAWAY AXONOMETRIC · NTS · ceiling and near-side upper joinery omitted

SPATIAL CHARACTER

Warm plaster, black frames, mesh, neutral cabinetry and warm shelf lighting follow the reference render.

GEOMETRIC BASIS

2400 × 3106 × 2600 envelope. Four 664 modules; centred 1000 × 450 counter; 500 / 900 / 500 rear zones.

CUTAWAY

Near-side upper units and ceiling removed to expose the room. Their full extent remains on the plans and elevations.

ACCURACY LIMIT

Visual fidelity target, not a measurable 80% certification. Approved dimensions override the render. Bottles are indicative; hardware and fixings remain TBC.


Material palette / visible finishes

AP-11 · sample-led specification; colours are indicative




BLACK STEEL

25 × 25 × 1.6 main SHS
20 × 20 × 1.6 secondary SHS
Matte black powder coat

 

CABINET STEEL

1.5 mm PPC doors
Light-neutral finish
Flush, handleless

 


PLASTER

Raw light textured plaster
Approve physical sample
Substrate / buildup #26



PORCELAIN

1200 × 600 rectified
2 grout / 5 perimeter joint
Stone-look, sample approval

 

CLEAR GLASS

12 mm toughened door
Hardware / gaps #16
Fixed pane specification TBC



EXPANDED MESH

Approx. 20 × 40 diamond
Black finish / framed edges
Gauge and fixing #16