


Retail interior / coordinated design

Design intent, measured geometry and assembly strategies

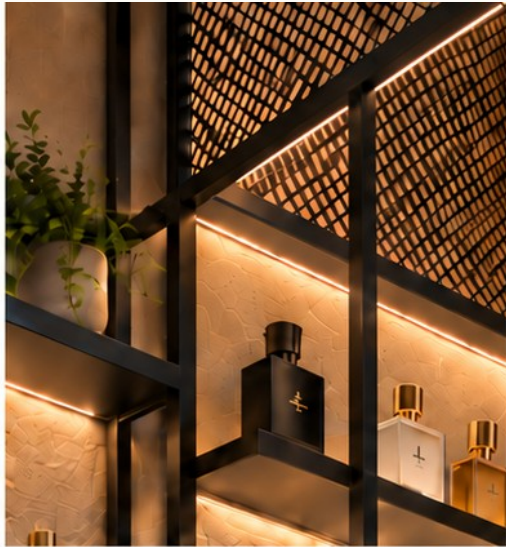


RAW PLASTER
WALL FINISH

BLACK METAL
SHELF



METAL MESH
PANEL

STONE LOOK
FLOOR TILE

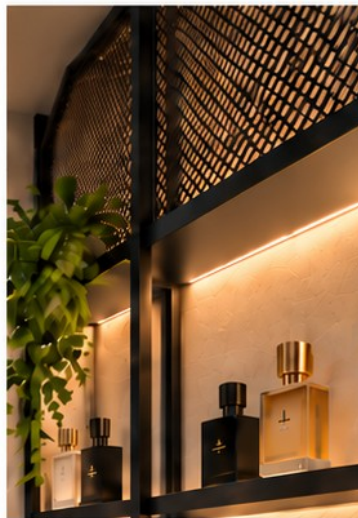

REFERENCE RENDER · NOT TO SCALE · styling props excluded from technical scope

PROJECT

2400 × 3106 internal
2600 ceiling
Black steel / plaster / stone-look floor

ISSUE PURPOSE

Client review and consultant coordination. Detailed strategies are preliminary pending the stated confirmations.

DRAWING PRIORITY

Geometry follows approved Rev A. Render conveys material and lighting character only.

READING SEQUENCE


Layout → elevations → materials → assembly details → coordination decisions.

Overall plan / setting-out

Setting-out / coordinated interfaces · 1:20 · finish-face dimensions; site verification pending

SET-OUT DATUMS

- A 0 / 0
- B 2400 / 0
- C 2400 / 3106
- D 0 / 3106

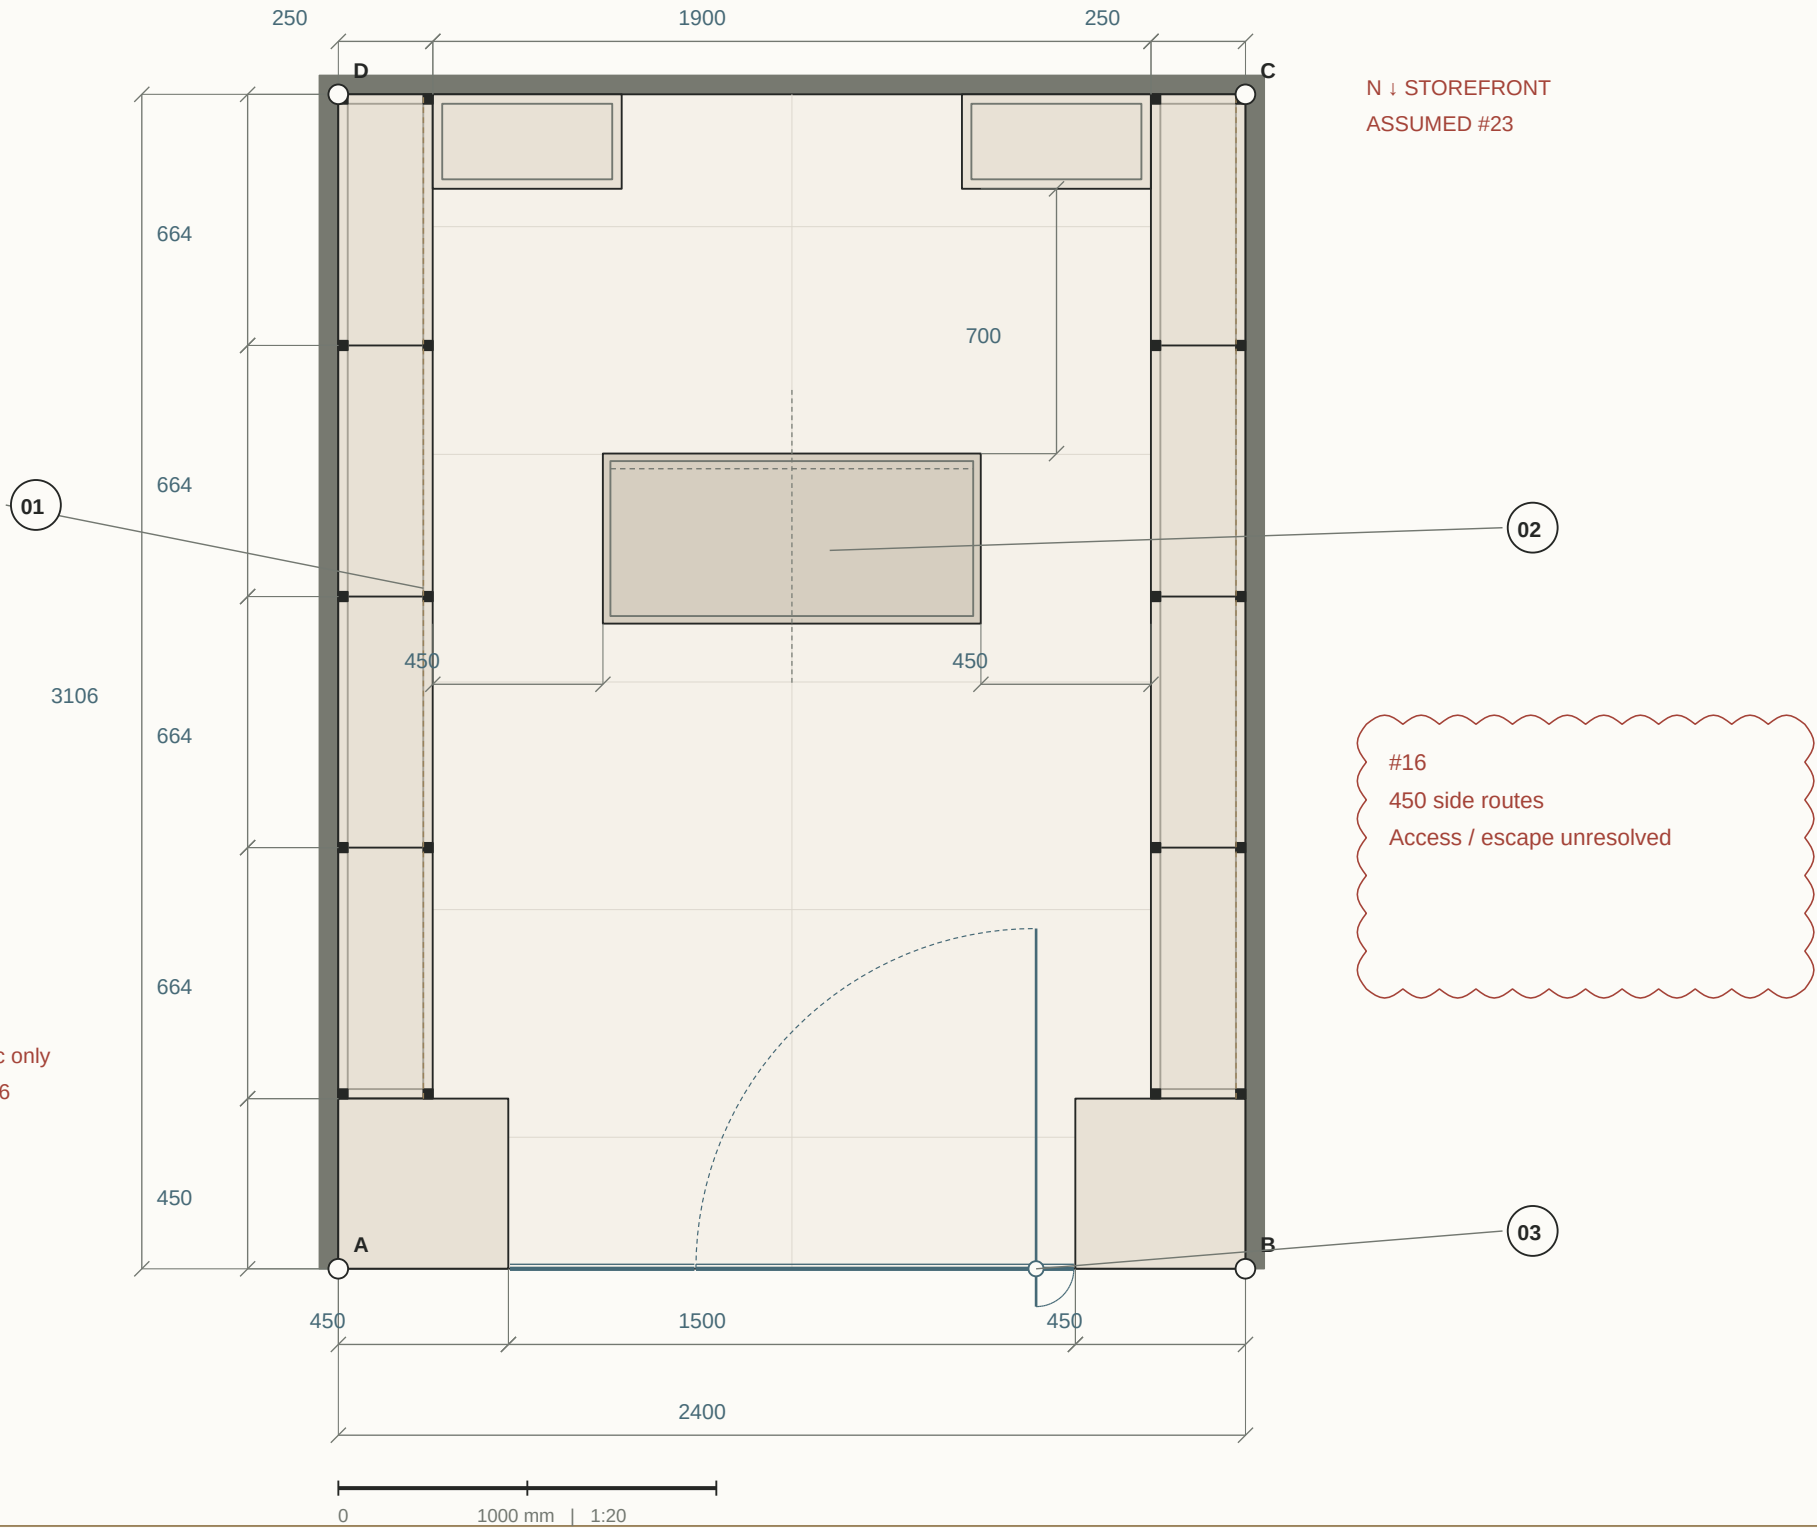

01 / FRAME + SETTING-OUT

250 deep side units. Four 664 modules from y=450 to 3106. 25 main uprights shown; shelf/support lines distinguished.

02 / COUNTER + REAR

1000 × 450 counter; x=700–1700, y=1706–2156. 700 to rear-unit face. Side routes remain 450 / 450.

03 / GLAZED ENTRANCE


488 fixed pane + 1000 pivot leaf + three 4 gaps = 1500. Pivot 100 from right edge; inward sweep shown.

04 / COORDINATION STATUS

LOD 350 development target: interfaces shown, not certified complete. Anchors, hardware, substrate and access remain TBC #16/#26.

Floor finish / module setting-out

AP-04 · porcelain extent includes floor beneath units

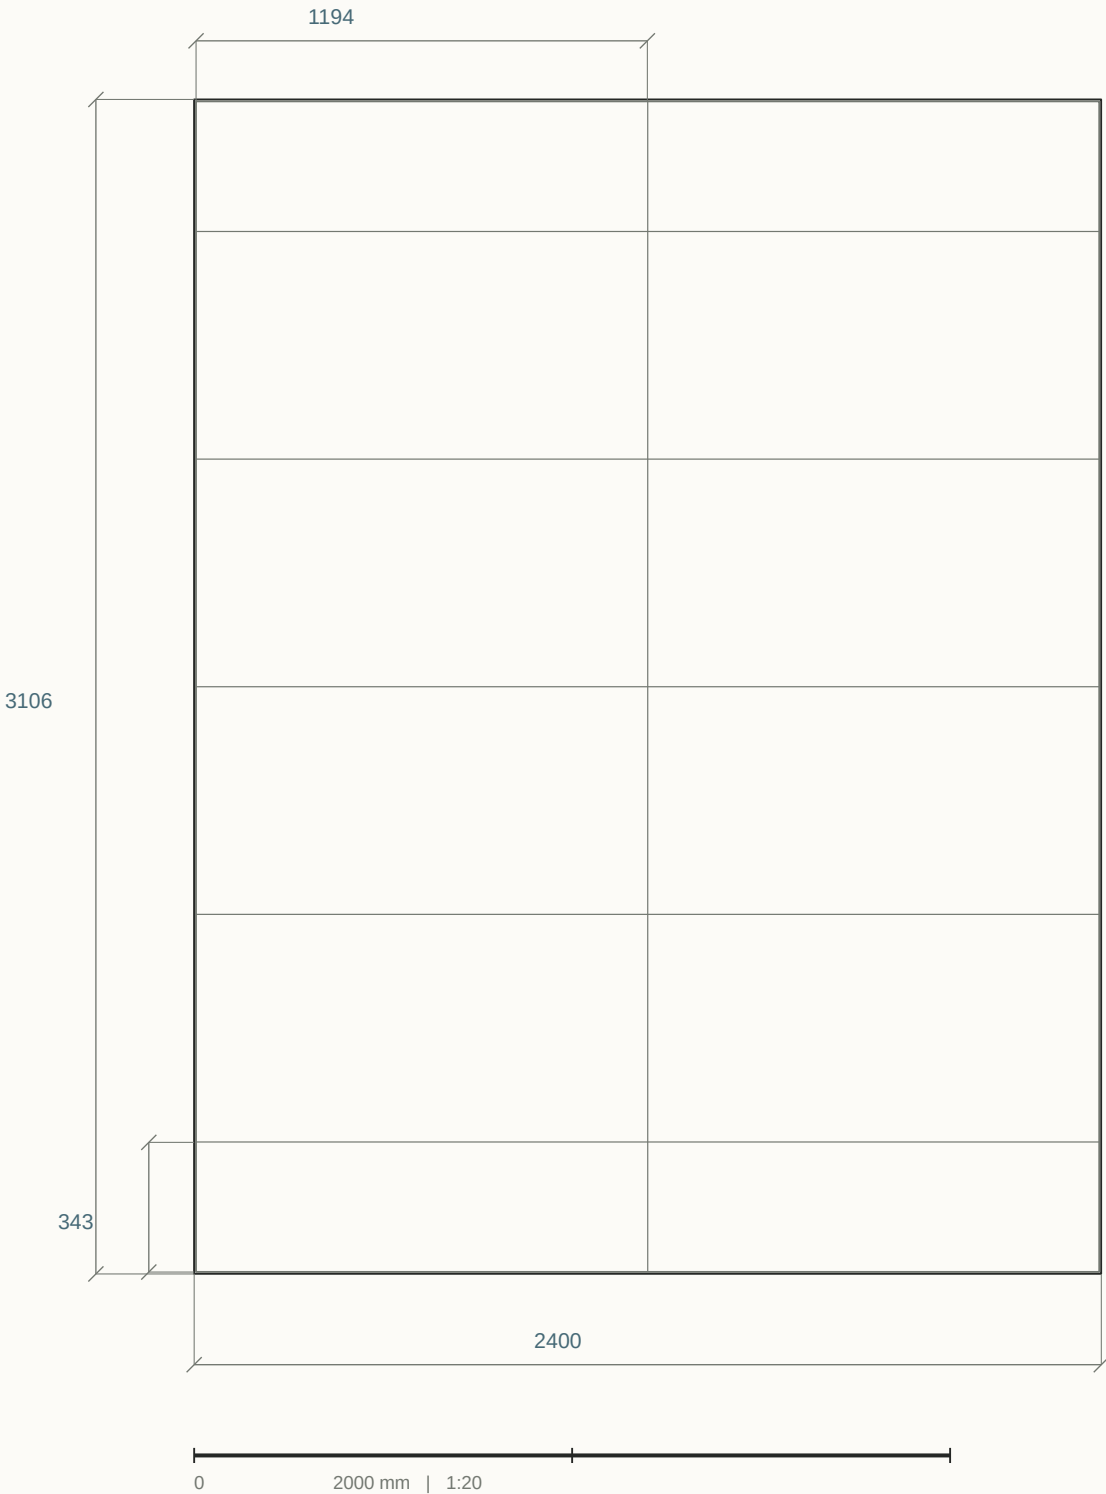

#4 / #26
Survey before tile ordering.
Cuts exclude fabrication tolerances.

M04 / PORCELAIN

1200 × 600 rectified stone-look porcelain. Option A: long side across shop. Joint = 2; perimeter = 5.

WIDTH CHAIN

$$5 + 1194 + 2 + 1194 + 5 = 2400$$

DEPTH CHAIN


$$5 + 343 + (4 \times 600) + (5 \times 2) + 343 + 5 = 3106$$

FLOOR BUILD-UP

Tile, adhesive and substrate thicknesses TBC #26. Flush threshold detail on AP-17; no step introduced.

Ceiling / lighting coordination

AP-05 · lighting positions follow confirmed Rev A

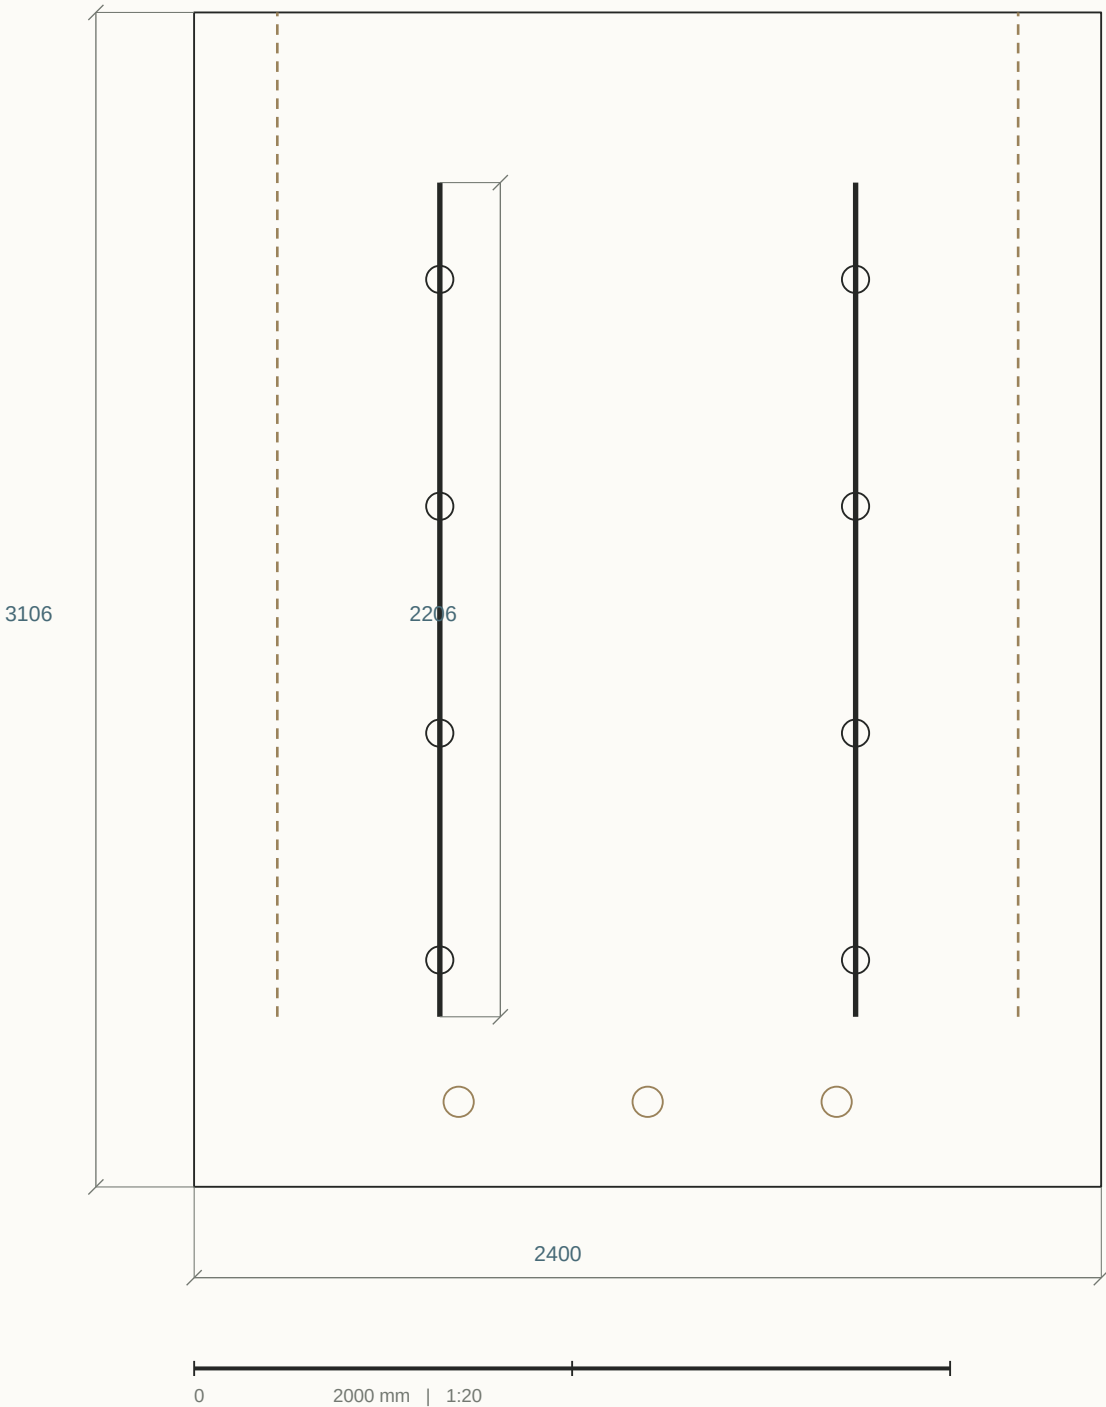

L01 / TRACKS

Two black tracks: x=650 / 1750, y=450–2656. Four adjustable cylindrical spots per track. All lighting 3000 K.

L02 / DOWNLIGHTS

Three fittings at x=700 / 1200 / 1700; y=225. Spacing retained from approved design.

L03 / SHELF + PLINTH


Concealed under-shelf LEDs; toe-kick LEDs 2 × 2656. Access and wiring strategy AP-14.

CEILING / MEP

Smooth gypsum, warm off-white. Ceiling support, fire/MEP devices and driver ventilation require consultant coordination #16.

Storefront / external elevation

AP-06 · glazed entrance and halo-lit fascia

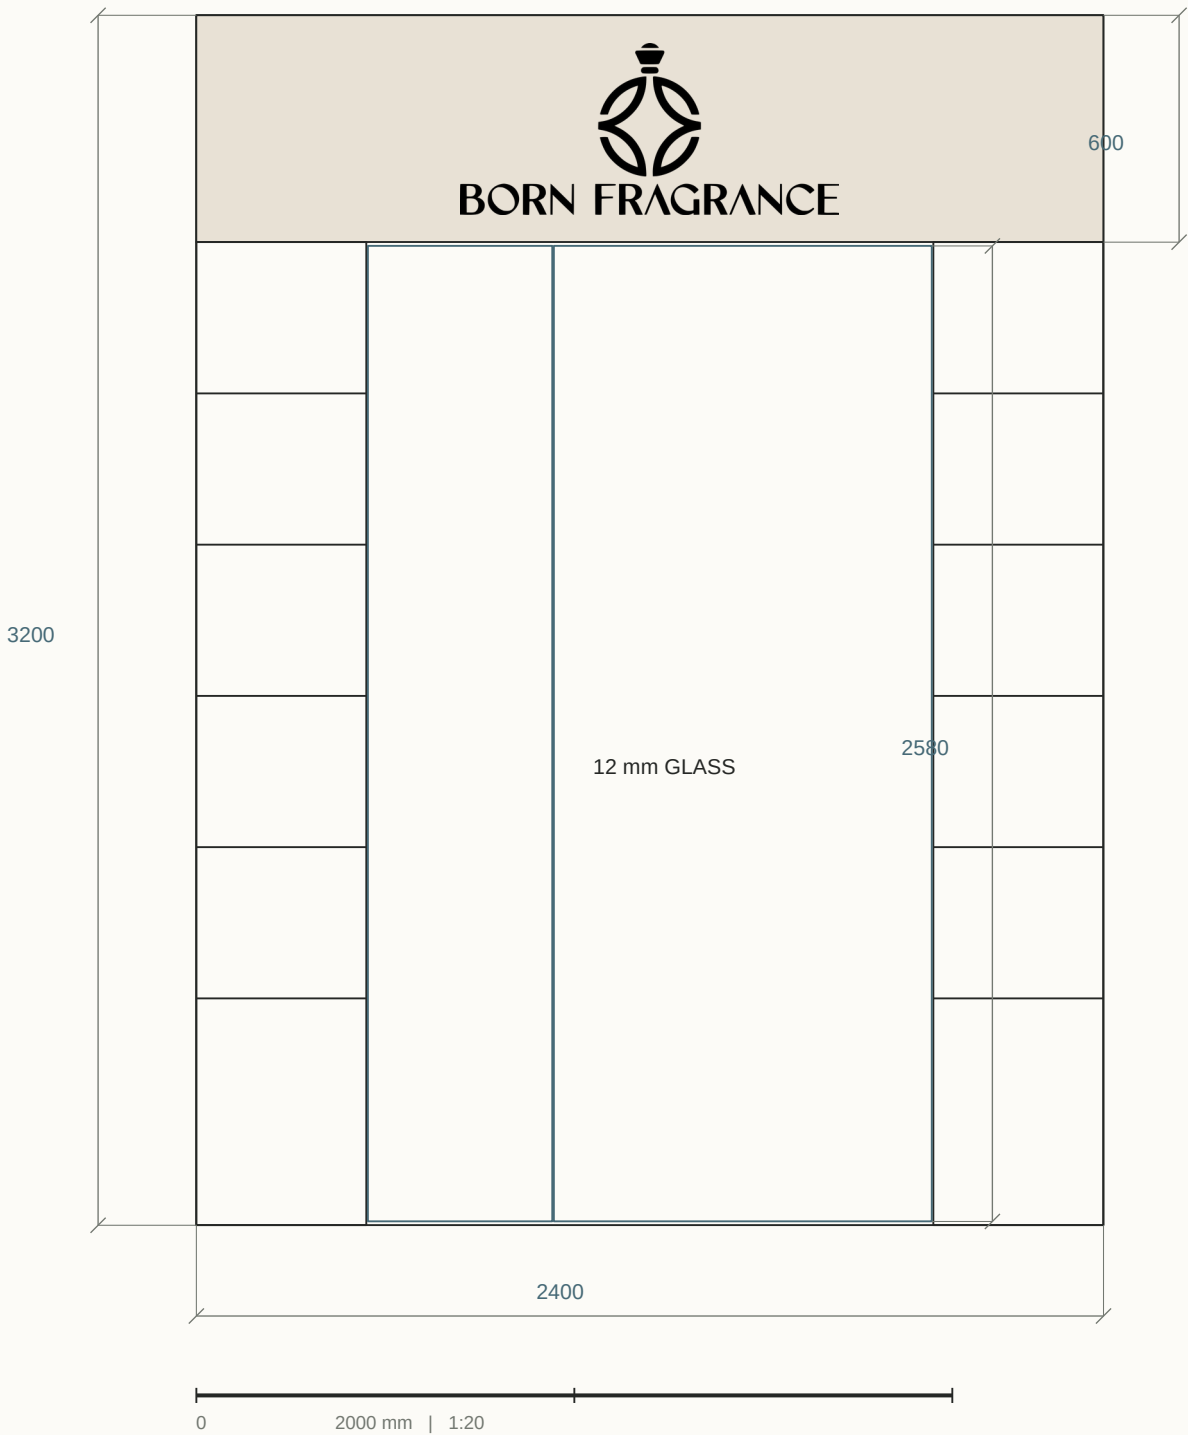

#16 — top/bottom clearance
10 + 2580 + 10 = 2600
PROPOSED split; glazier to confirm

FRONTAGE

450 + 1500 + 450 = 2400. The 450 × 450 display columns face the street; shelf depth remains 250.

G01 / GLAZING

Door 1000 × 2580 × 12 toughened glass. Fixed pane 488 W. Three nominal 4 gaps: 488 + 1000 + 12 = 1500.

SIGN BAND


600 high above 2600 ceiling datum; total storefront height 3200. Exterior logo 1000 W, uniformly scaled.

DETAIL REFERENCES

- Head AP-15
- Jamb / pivot AP-16
- Flush threshold AP-17
- Sign backing AP-18

Rear focal wall / internal elevation

AP-07 · wall-mounted non-illuminated brand mark

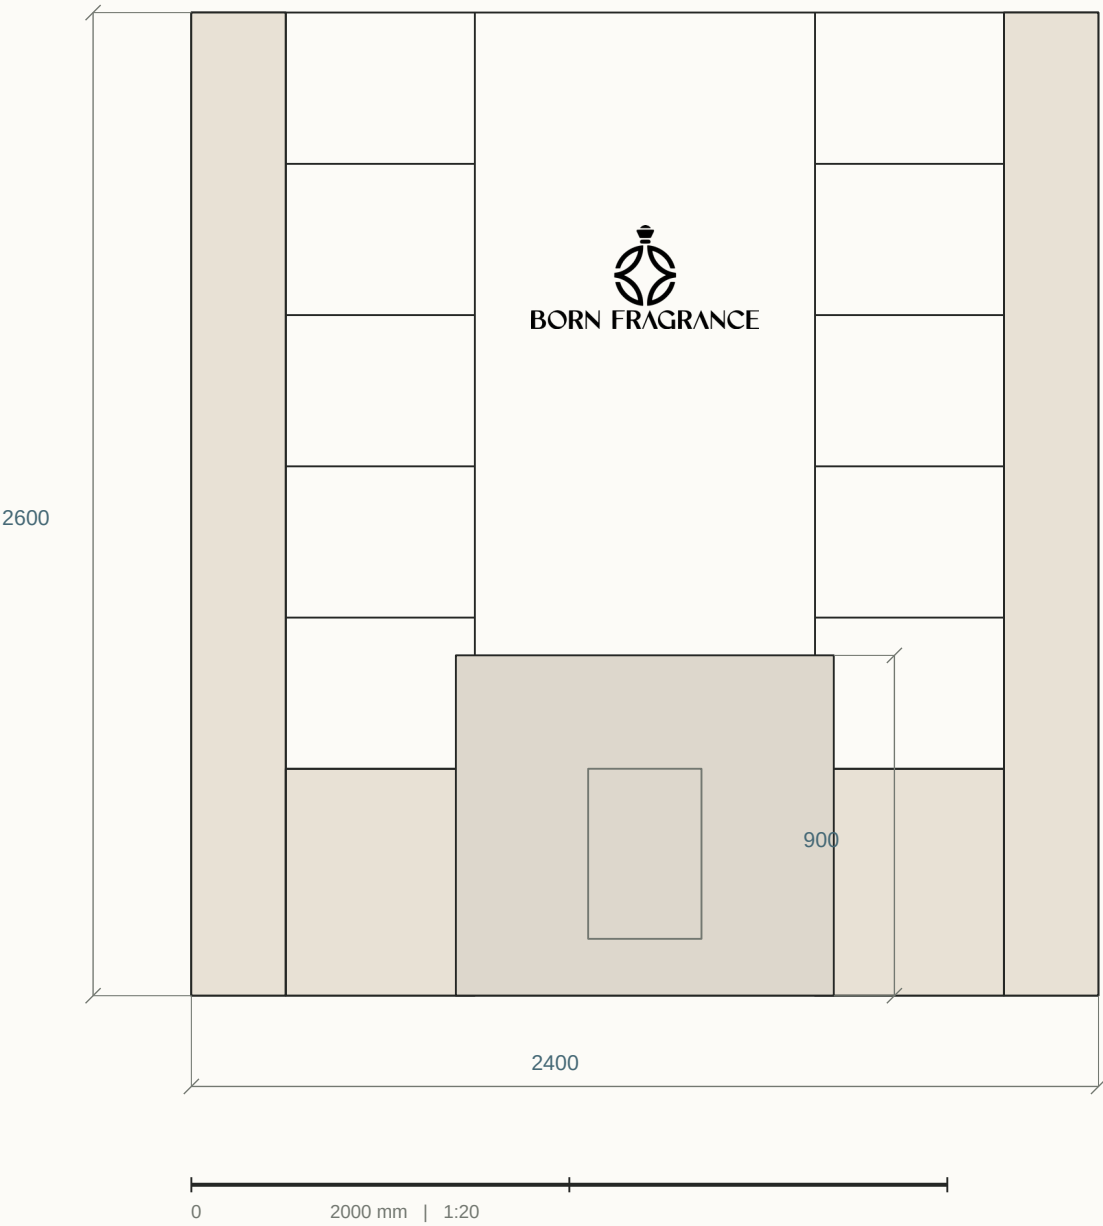

REAR MODULES

250 side + 500 display + 900 logo zone + 500 display + 250 side = 2400. Rear display depth 250.

BRAND

600 W logo at centre z=1900. Native asset ratio retained; approximately 271.8 H. No illumination or rear mesh.

DISPLAY LEVELS

600 / 1000 / 1400 / 1800 / 2200 AFFL. Frame 2600; top mesh is confined to side units.


ASSEMBLY

Removable central back panel and wall fixing strategy AP-19. Rear shelf LEDs return into accessible service routes.

Left display / internal elevation

Developed display elevation · interfaces + material codes · bottles indicative only

M01 / BLACK STEEL M02 / NEUTRAL PPC M05 / MESH L03 / 3000 K LED

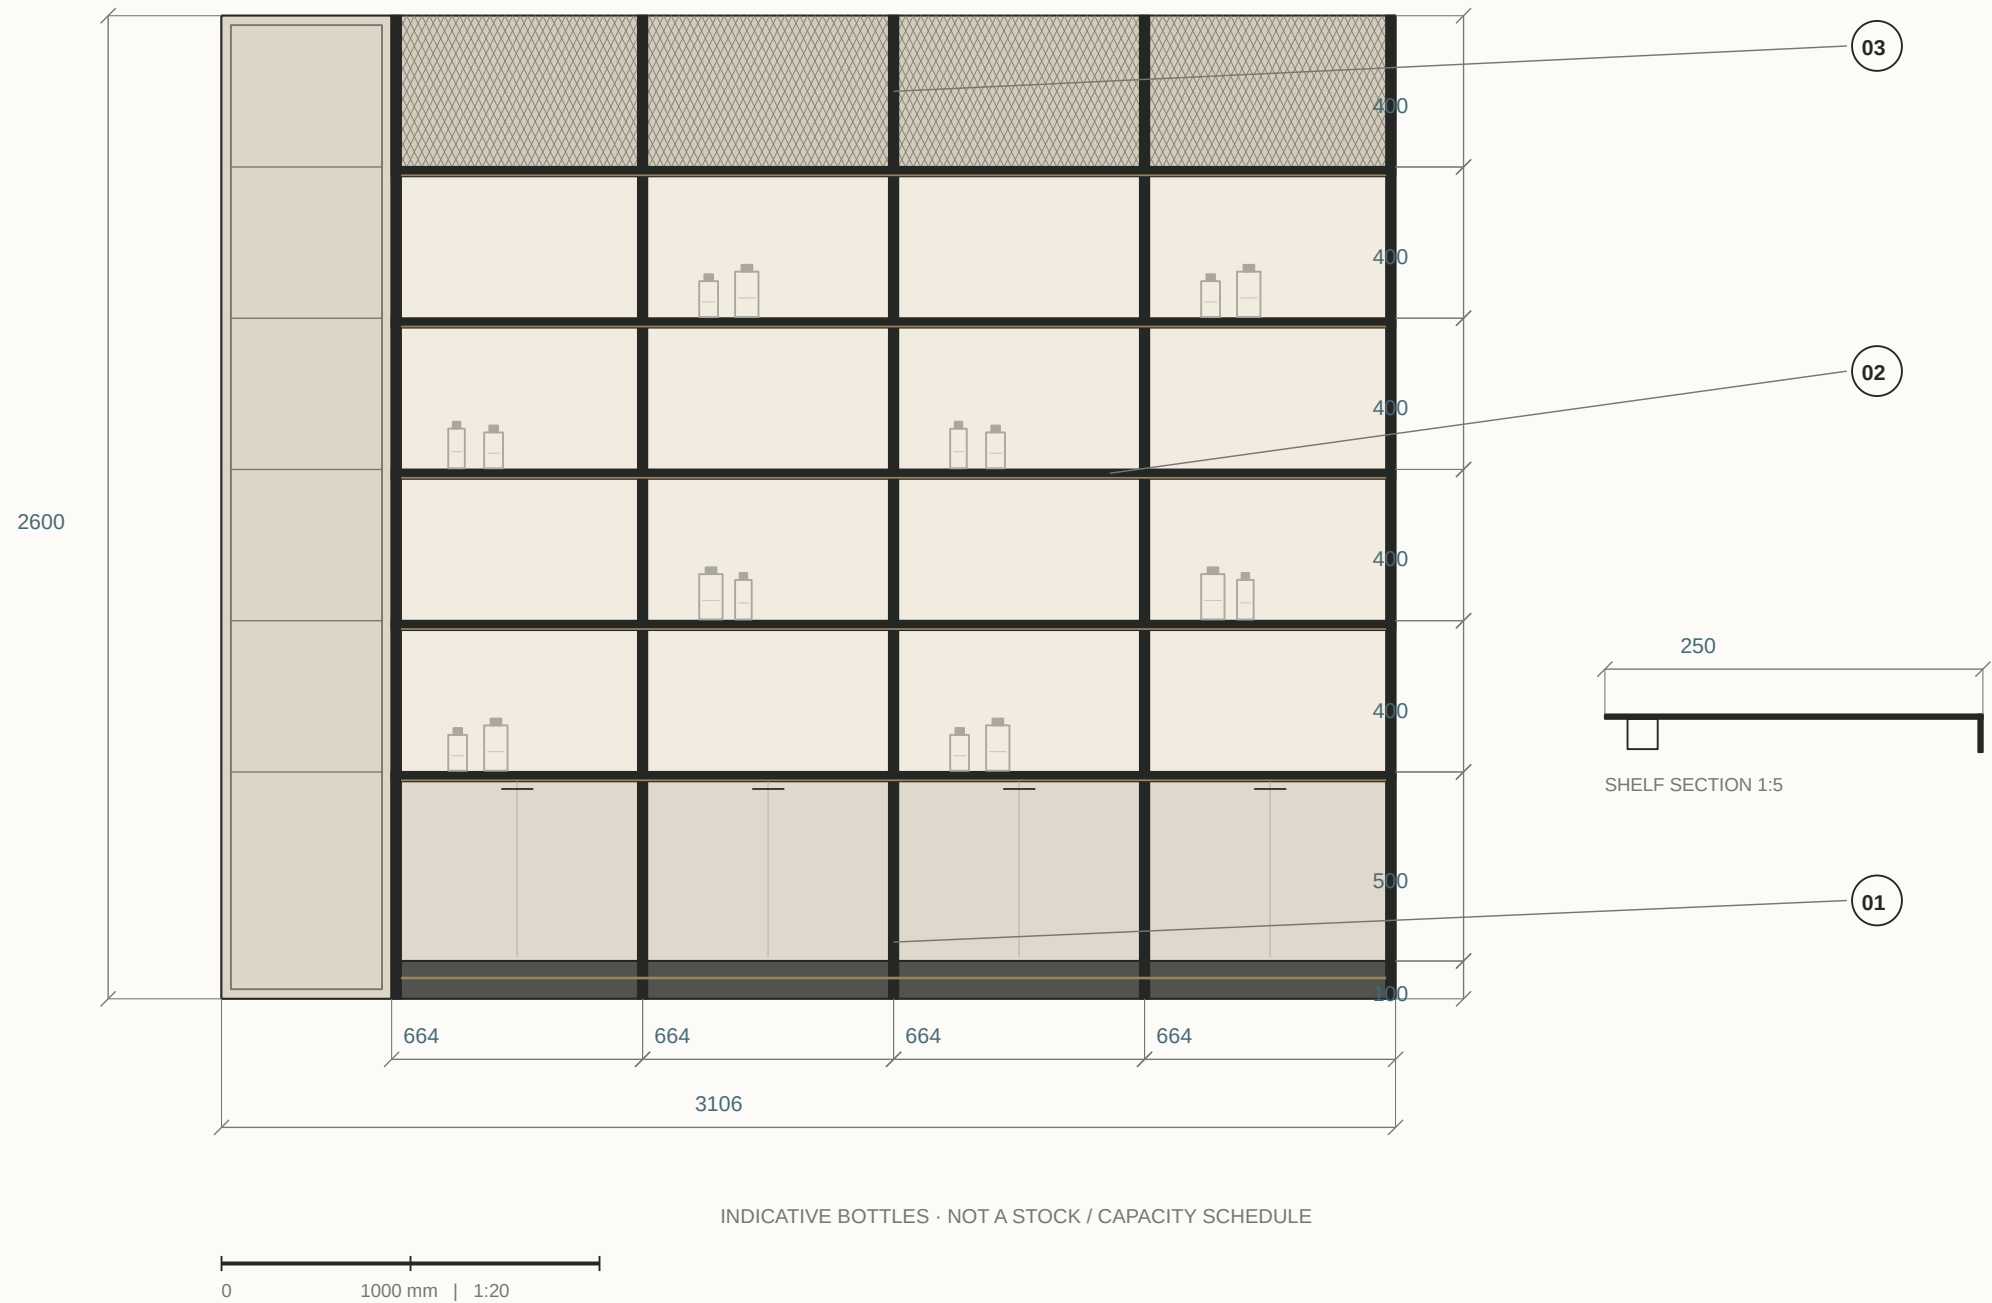

01 / STEEL FRAME

25 × 25 × 1.6 main SHS; 20 × 20 × 1.6 secondary supports.
664 module is not a fabrication cut size.

02 / SHELF + LIGHT

3 mm tray / 25 downstand / 250 depth. Concealed 3000 K LED
behind front edge; see section inset.

03 / BASE + MESH

600 base includes 100 recessed plinth. 1.5 PPC doors. Mesh
at 2200–2600; approximate 20 × 40 diamonds.


04 / INDICATIVE CONTENT

Sparse fragrance bottles added at owner request for visual
scale only. Excluded from dimensions and schedules. Fixings
and cable routing #16 remain open.

Right display / internal elevation

Developed display elevation · interfaces + material codes · bottles indicative only

M01 / BLACK STEEL M02 / NEUTRAL PPC M05 / MESH L03 / 3000 K LED

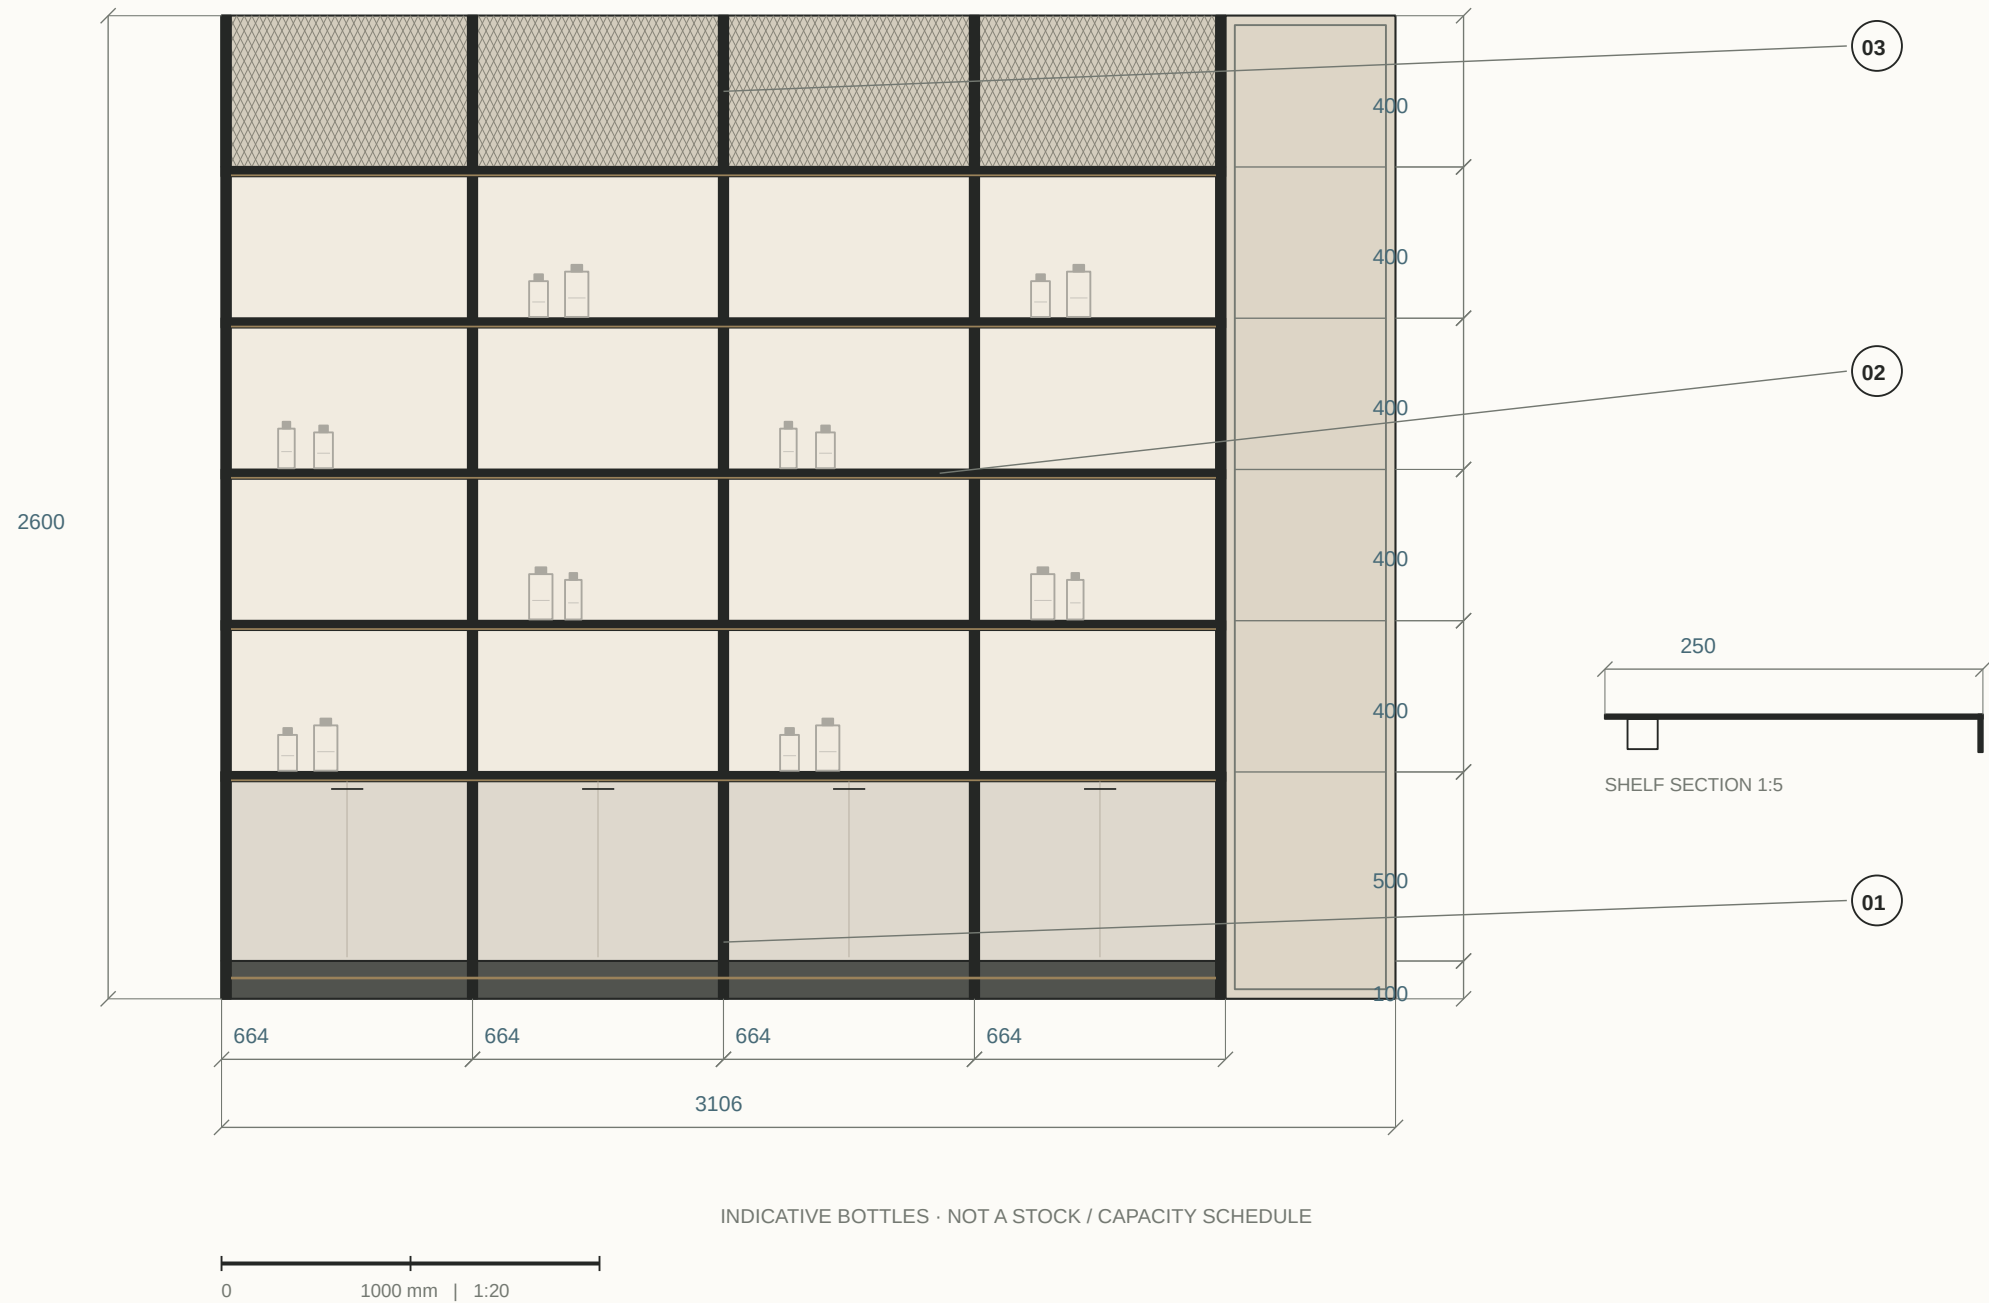

01 / STEEL FRAME

25 × 25 × 1.6 main SHS; 20 × 20 × 1.6 secondary supports.
664 module is not a fabrication cut size.

02 / SHELF + LIGHT

3 mm tray / 25 downstand / 250 depth. Concealed 3000 K LED
behind front edge; see section inset.

03 / BASE + MESH


600 base includes 100 recessed plinth. 1.5 PPC doors. Mesh
at 2200–2600; approximate 20 × 40 diamonds.

04 / INDICATIVE CONTENT

Sparse fragrance bottles added at owner request for visual
scale only. Excluded from dimensions and schedules. Fixings
and cable routing #16 remain open.

Spatial assembly / cutaway axonometric

Shaded cutaway / approved geometry + render material language · near wall and ceiling removed

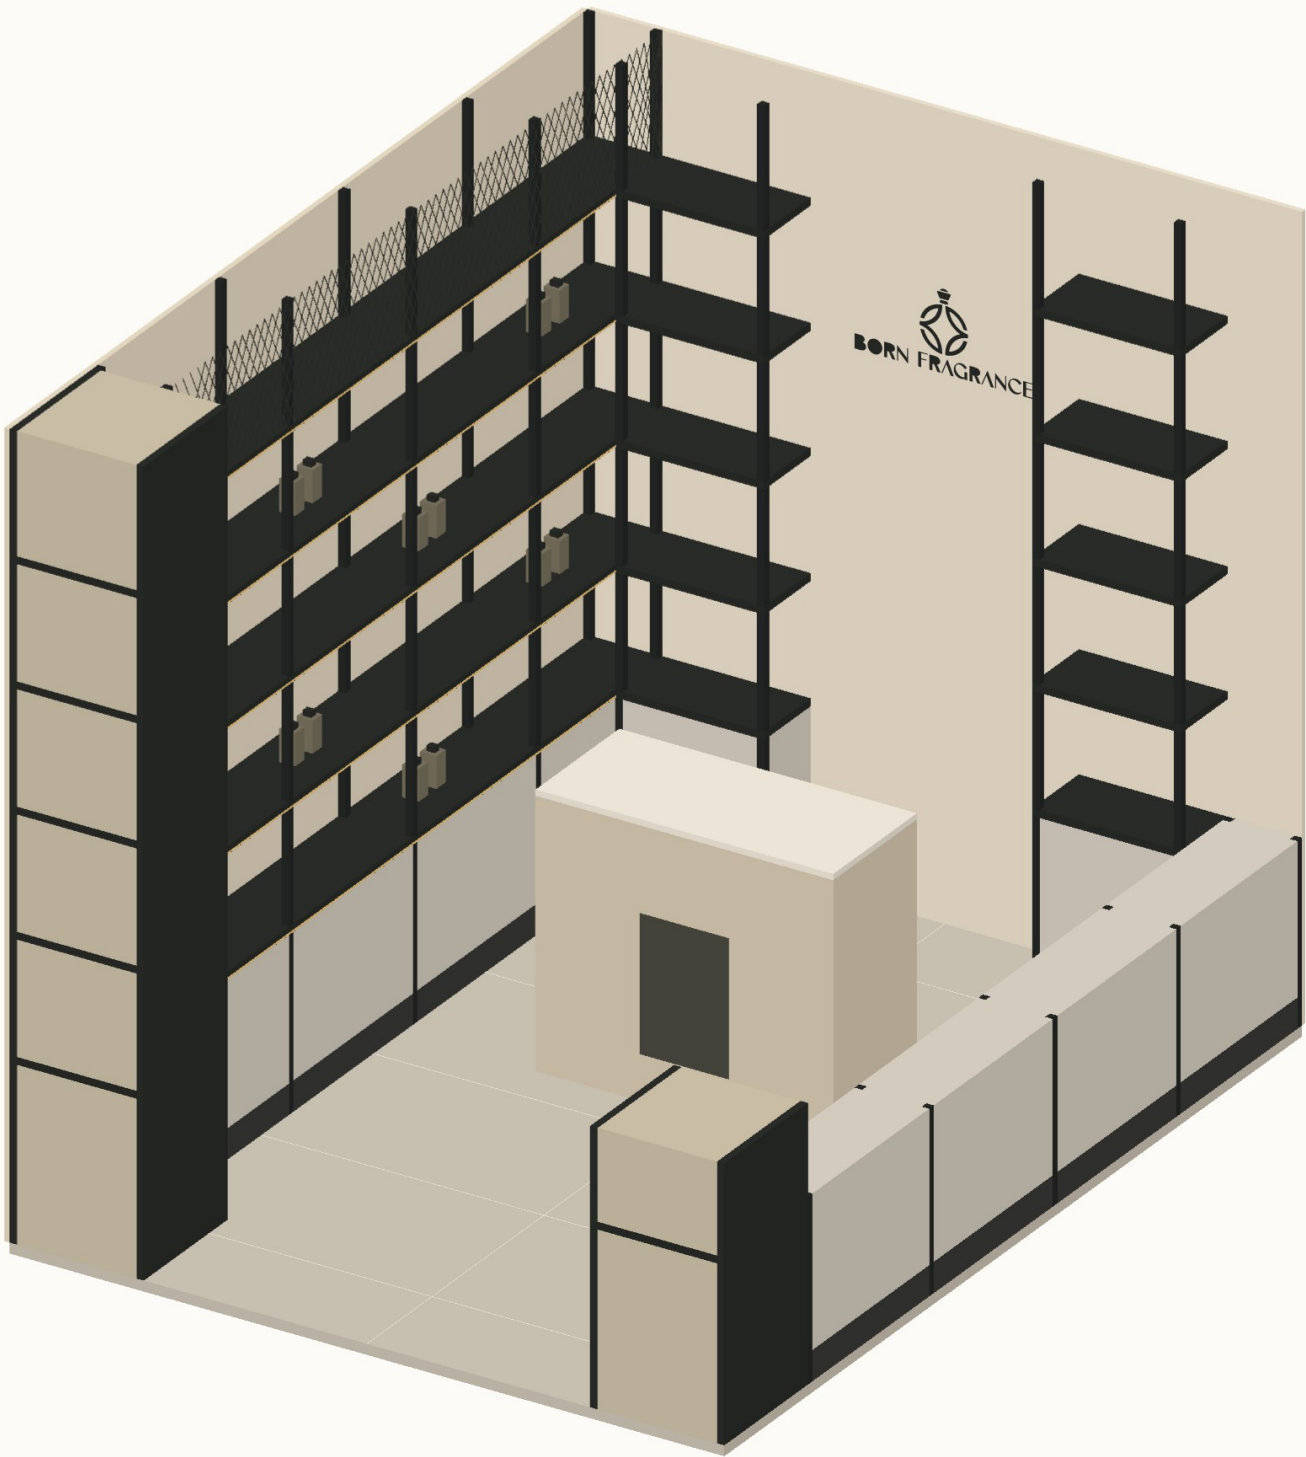

CUTAWAY AXONOMETRIC · NTS · ceiling and near-side upper joinery omitted

01 / SPATIAL CHARACTER

Warm plaster, black frames, mesh, neutral cabinetry and warm shelf lighting follow the reference render.

02 / GEOMETRIC BASIS

2400 × 3106 × 2600 envelope. Four 664 modules; centred 1000 × 450 counter; 500 / 900 / 500 rear zones.

03 / CUTAWAY

Near-side upper units and ceiling removed to expose the room. Their full extent remains on the plans and elevations.

04 / ACCURACY LIMIT

Visual fidelity target, not a measurable 80% certification. Approved dimensions override the render. Bottles are indicative; hardware and fixings remain TBC.


Material palette / visible finishes

AP-11 · sample-led specification; colours are indicative




M01 / BLACK STEEL

25 × 25 × 1.6 main SHS
20 × 20 × 1.6 secondary SHS
Matte black powder coat

 

M02 / CABINET STEEL

1.5 mm PPC doors
Light-neutral finish
Flush, handleless

 


M03 / PLASTER

Raw light textured plaster
Approve physical sample
Substrate / buildup #26



M04 / PORCELAIN

1200 × 600 rectified
2 grout / 5 perimeter joint
Stone-look, sample approval

 

G01 / CLEAR GLASS

12 mm toughened door
Hardware / gaps #16
Fixed pane specification TBC



M05 / EXPANDED MESH

Approx. 20 × 40 diamond
Black finish / framed edges
Gauge and fixing #16