

RETAIL INTERIOR / COORDINATED DESIGN



Storefront, interior and display details · neutral material tones



STOREFRONT / DESIGN INTENT



INTERIOR / DISPLAY AND COUNTER



MESH / LIGHT



DISPLAY FRAME



PLASTER / SHELF

OVERALL PLAN / SETTING-OUT


Setting-out / coordinated interfaces · 1:20 · finish-face dimensions; site verification pending

SET-OUT DATUMS

- A 0 / 0
- B 2400 / 0
- C 2400 / 3106
- D 0 / 3106

STREET-FACING DISPLAY
Dashed line: shelf above
Solid return toward interior

Wall bands graphic only
Thickness TBC #26
Envelope TBC #4

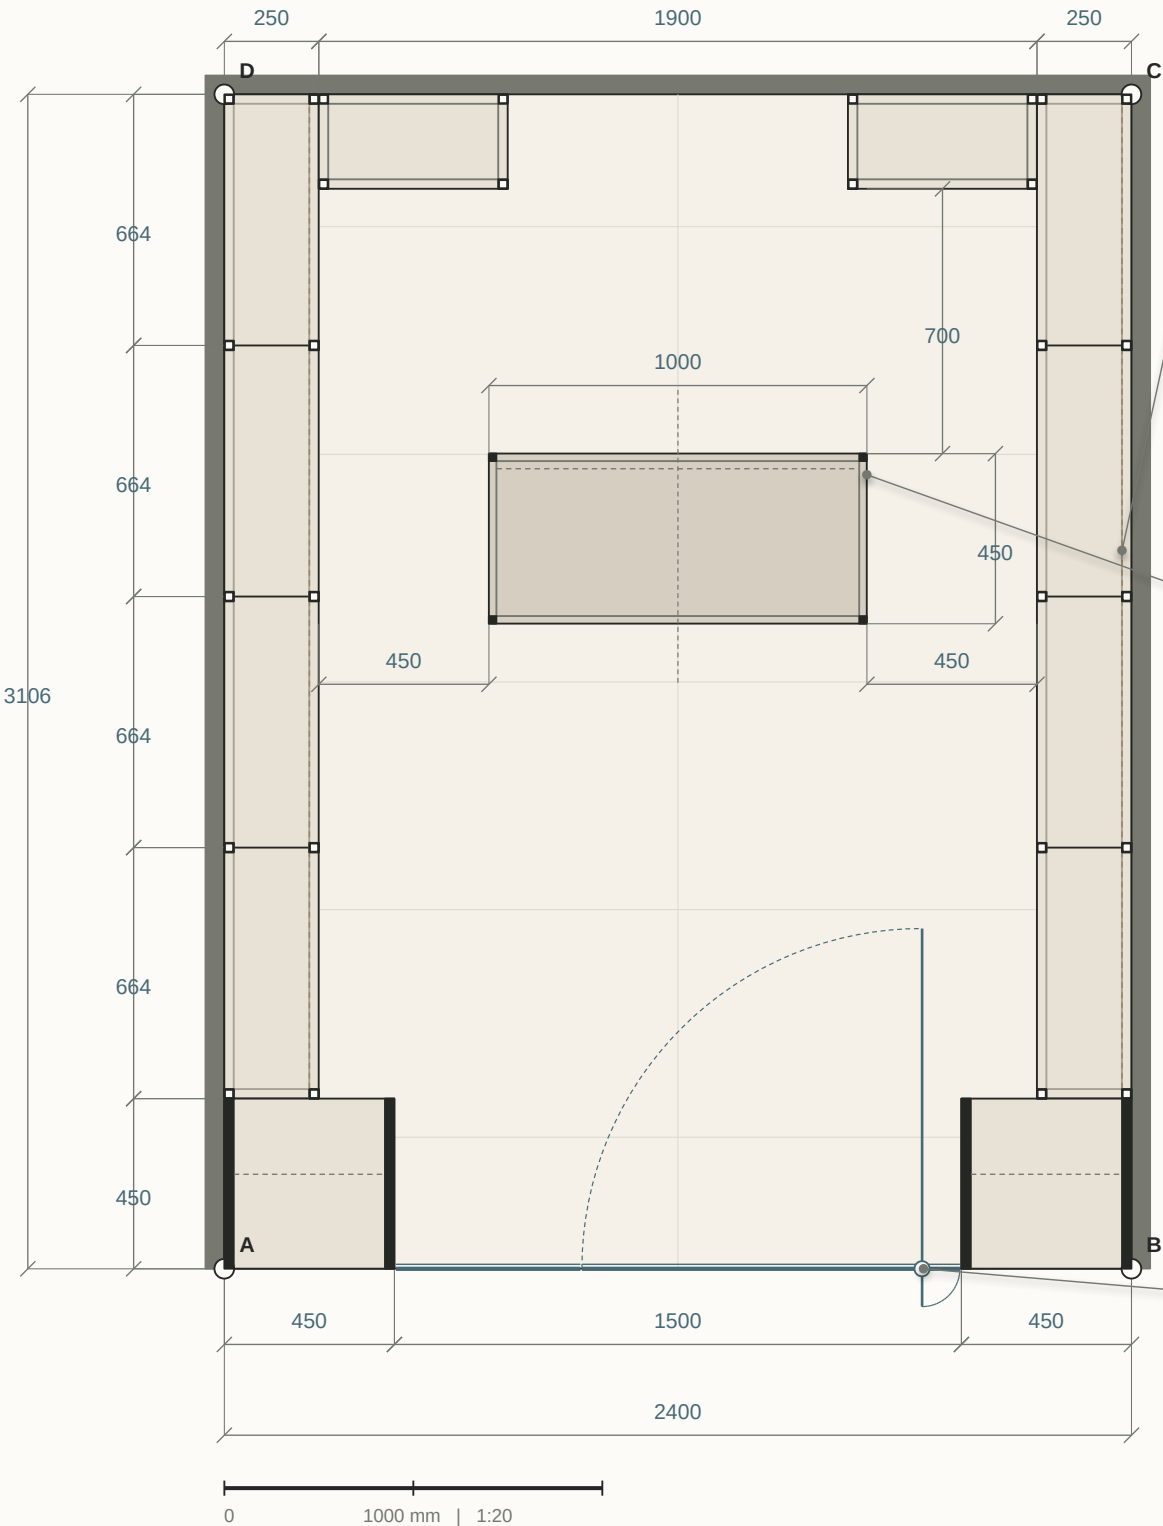

N ↓ STOREFRONT
ASSUMED #23


SIDE DISPLAY
250 deep shelving
25 × 25 main steel frame

COUNTER / STEEL FRAME
1000 × 450 footprint
20 × 20 black steel

PIVOT GLASS DOOR
1000-wide leaf · 12 glass
Inward opening


REAR / SIDE JUNCTION

LOCAL PLAN 1:5

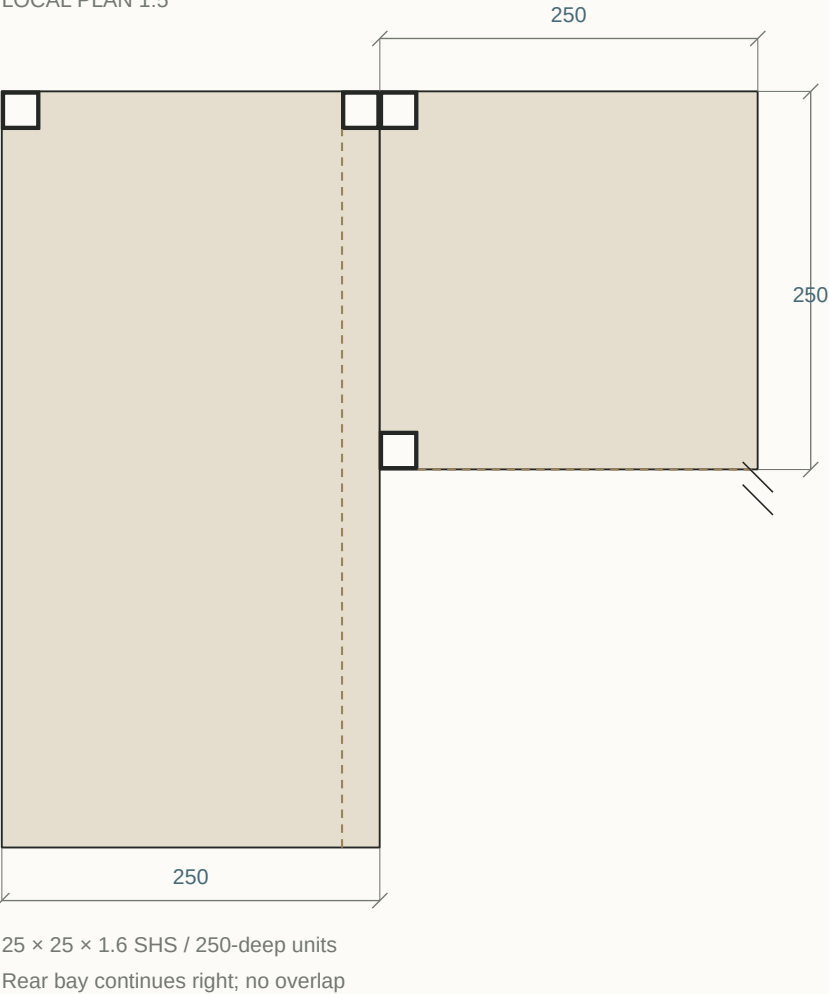

DOOR EDGE / PIVOT

LOCAL PLAN 1:2

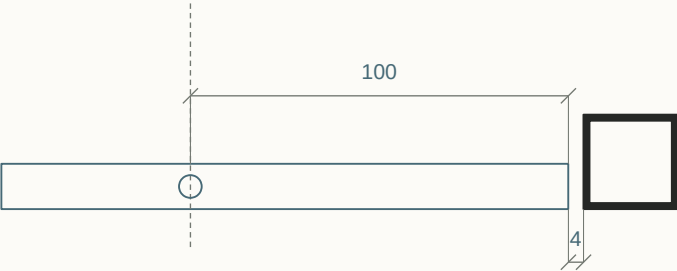


12 glass / 4 gap / 25 SHS · pivot fittings TBC #16

CEILING / LIGHTING COORDINATION




Reflected ceiling plan · lighting, display footprints and dimensional coordination

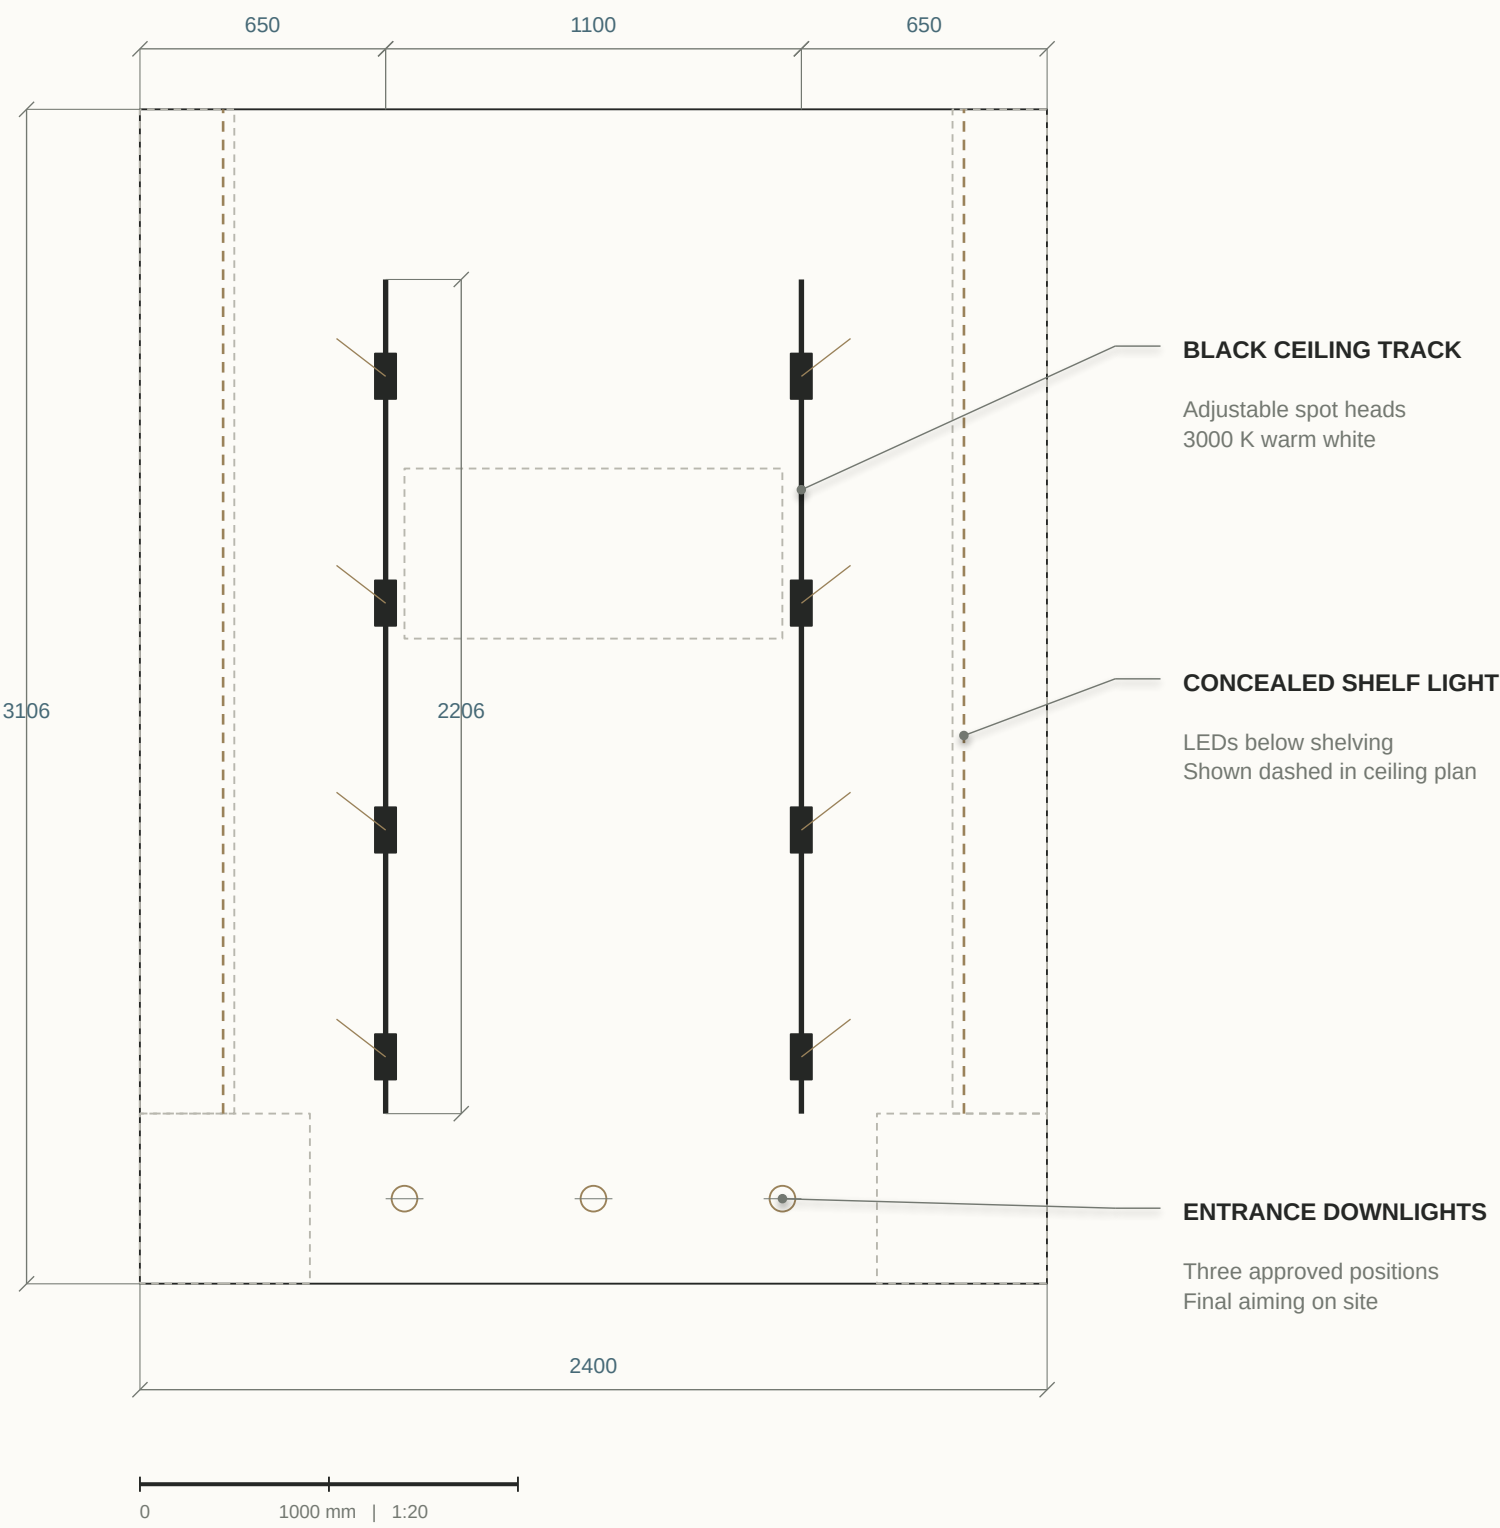

UNIT HEAD / CEILING


SECTION 1:5

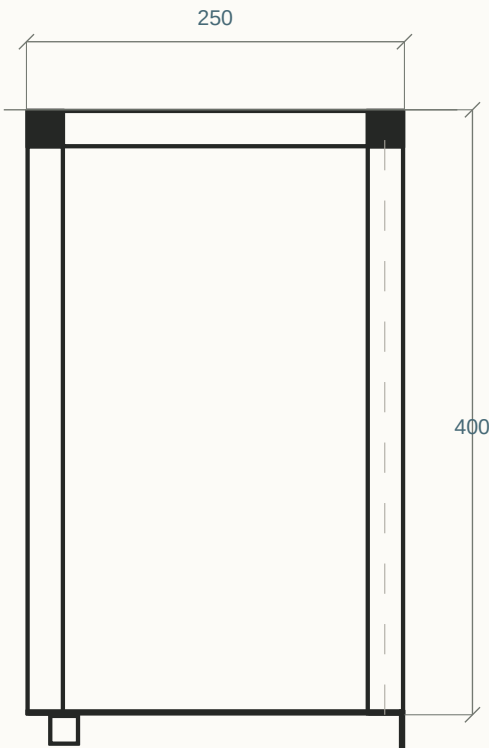

2600 ceiling / frame datum
Mesh zone 2200–2600 at front
Wall fixings TBC #16; no gypsum fixing

FOLDED TRAY / LIGHT

SECTION 1:2

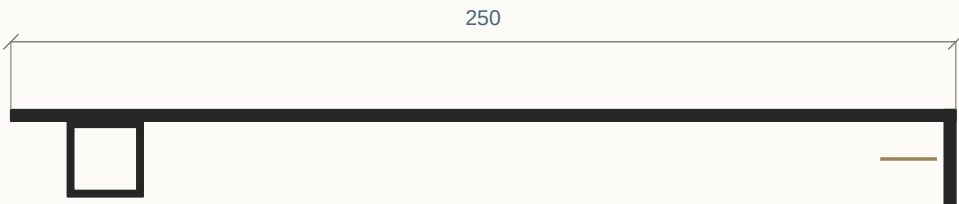


3 mm folded tray · 25 front downstand
20 × 20 × 1.6 support · LED profile TBC #16

STOREFRONT / EXTERNAL ELEVATION



Developed storefront · street-facing displays, glazed entrance and halo-lit brand

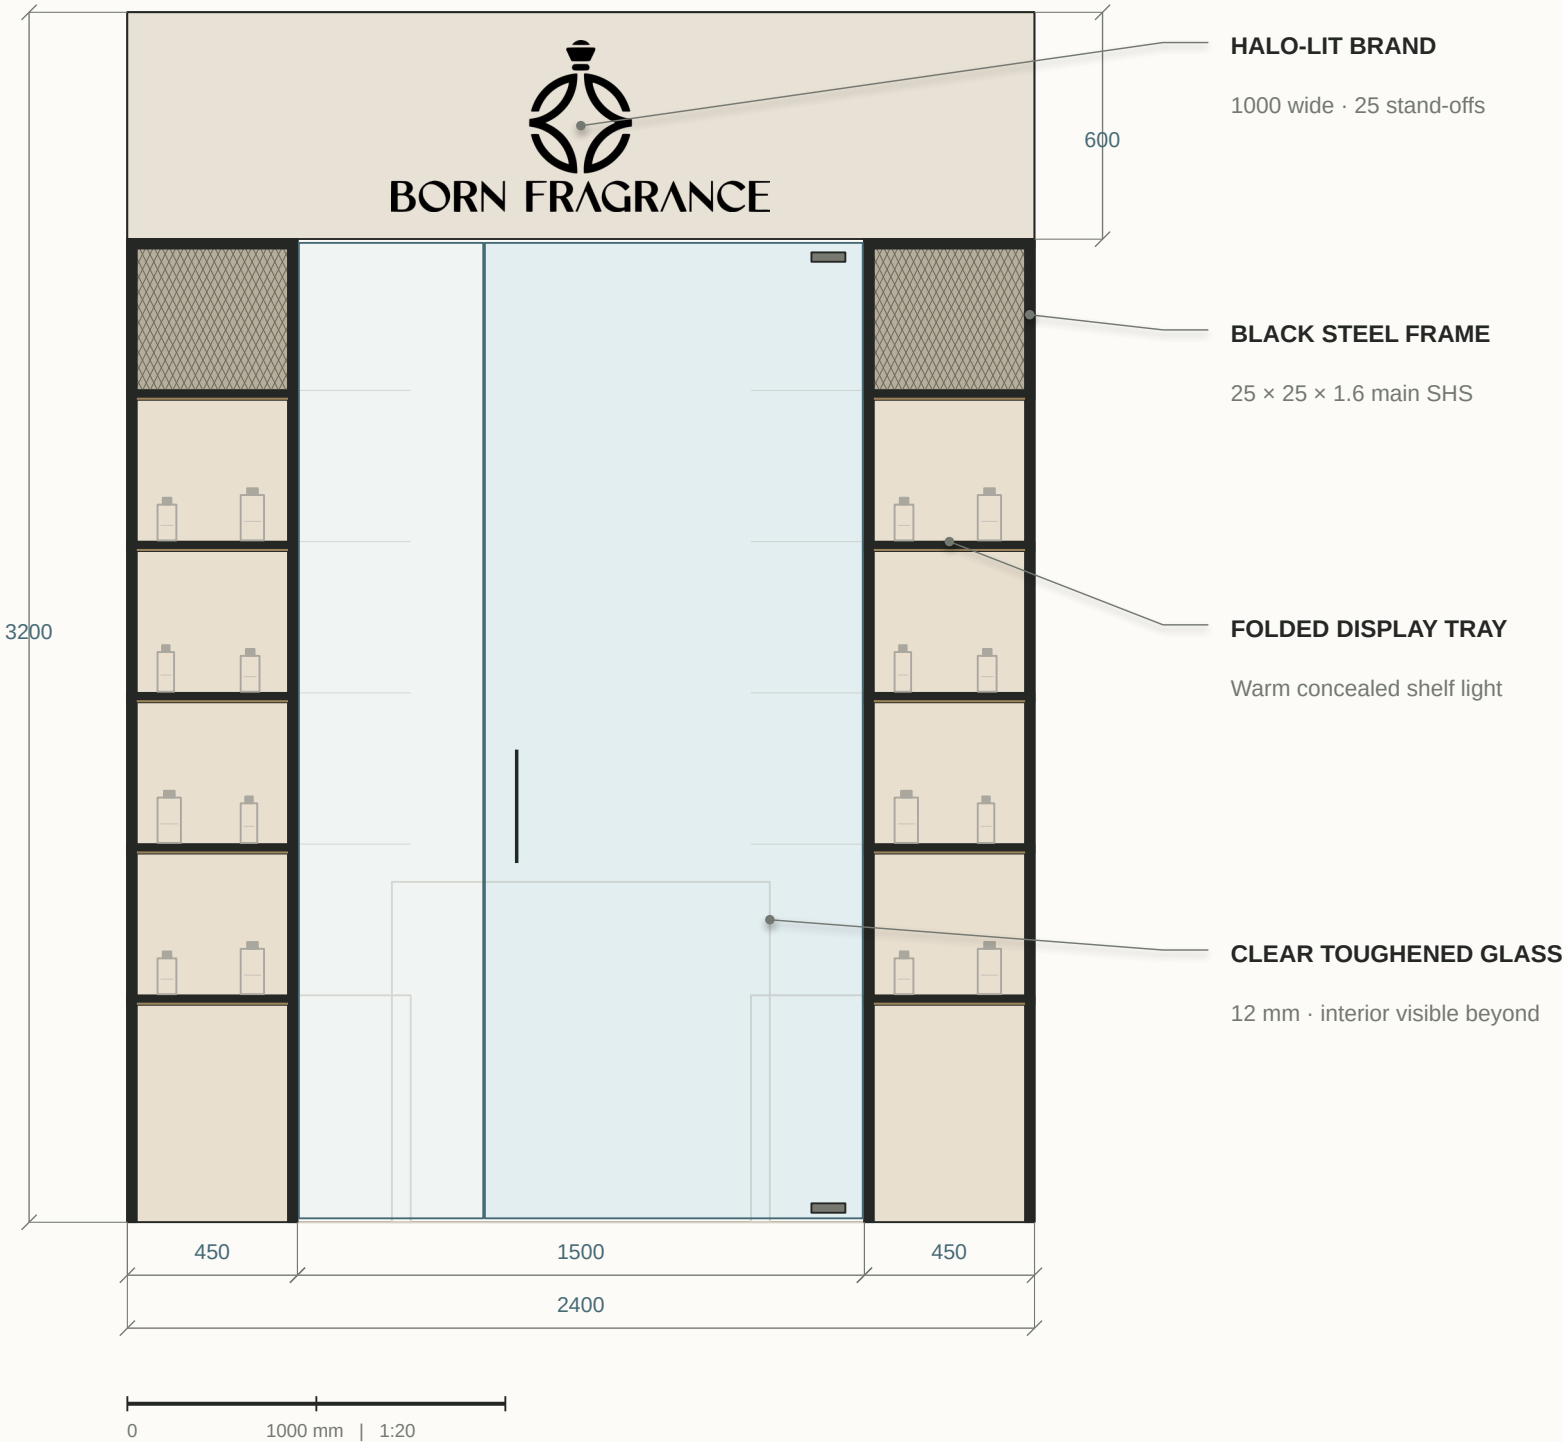

HALO LETTER / BACKING

STAND-OFF SECTION 1:2




25 stand-off · halo behind black letters
Backing / wall support / drivers TBC #16

REAR FOCAL WALL / INTERNAL ELEVATION




Rear focal wall · developed shelving + owner-directed counter front

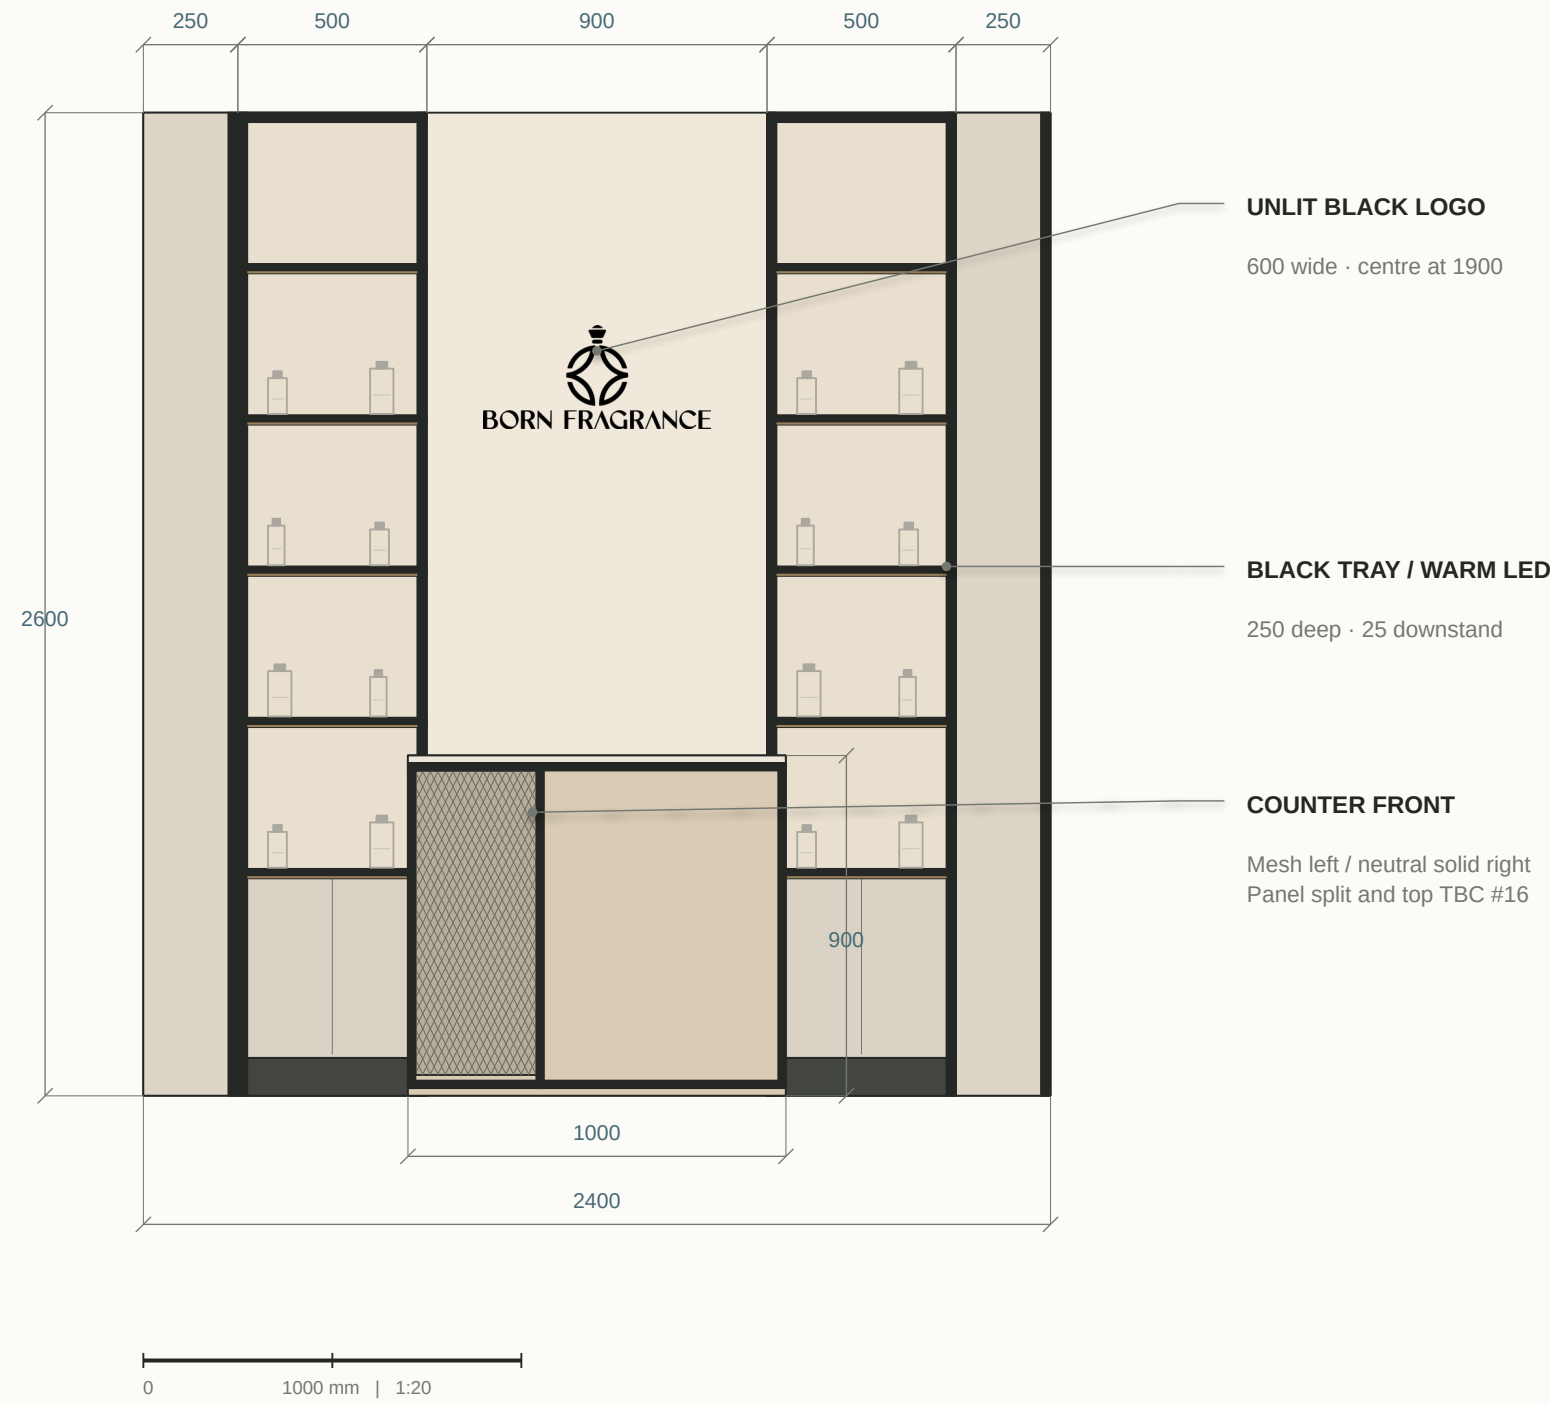


REAR SHELF / FRAME

SECTION 1:2

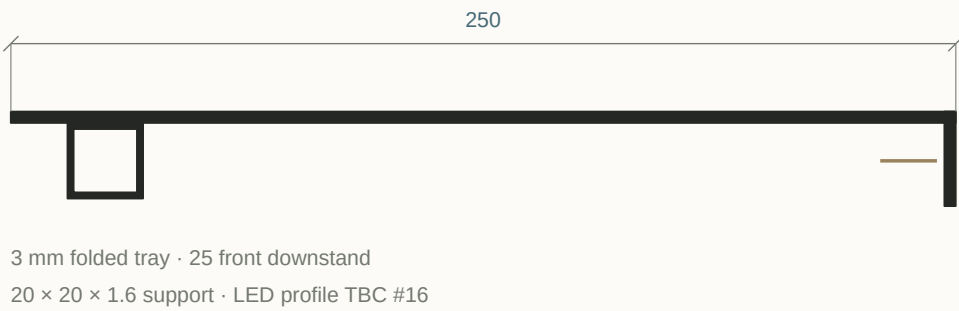

COUNTER / FOOTPRINT

PLAN 1:10

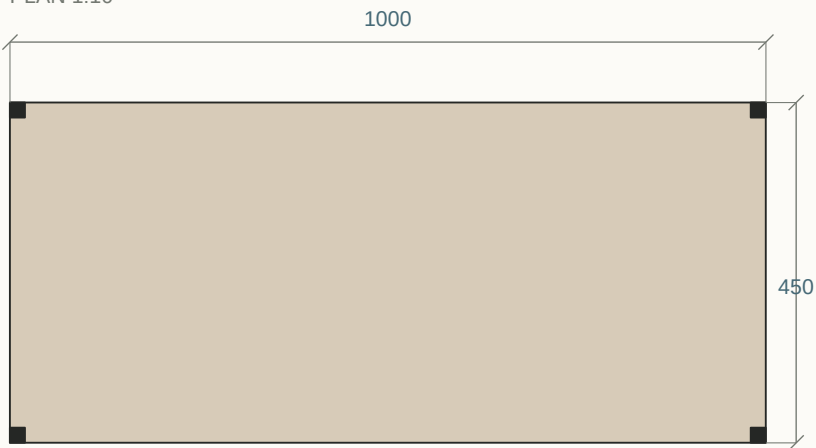



20 × 20 frame · front split TBC #16

LEFT DISPLAY / INTERNAL ELEVATION

Developed display elevation · interfaces + material codes · bottles indicative only

BLACK STEEL / NEUTRAL PPC / EXPANDED MESH / 3000 K LED


SOLID COLUMN
RETURN
Display faces street

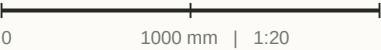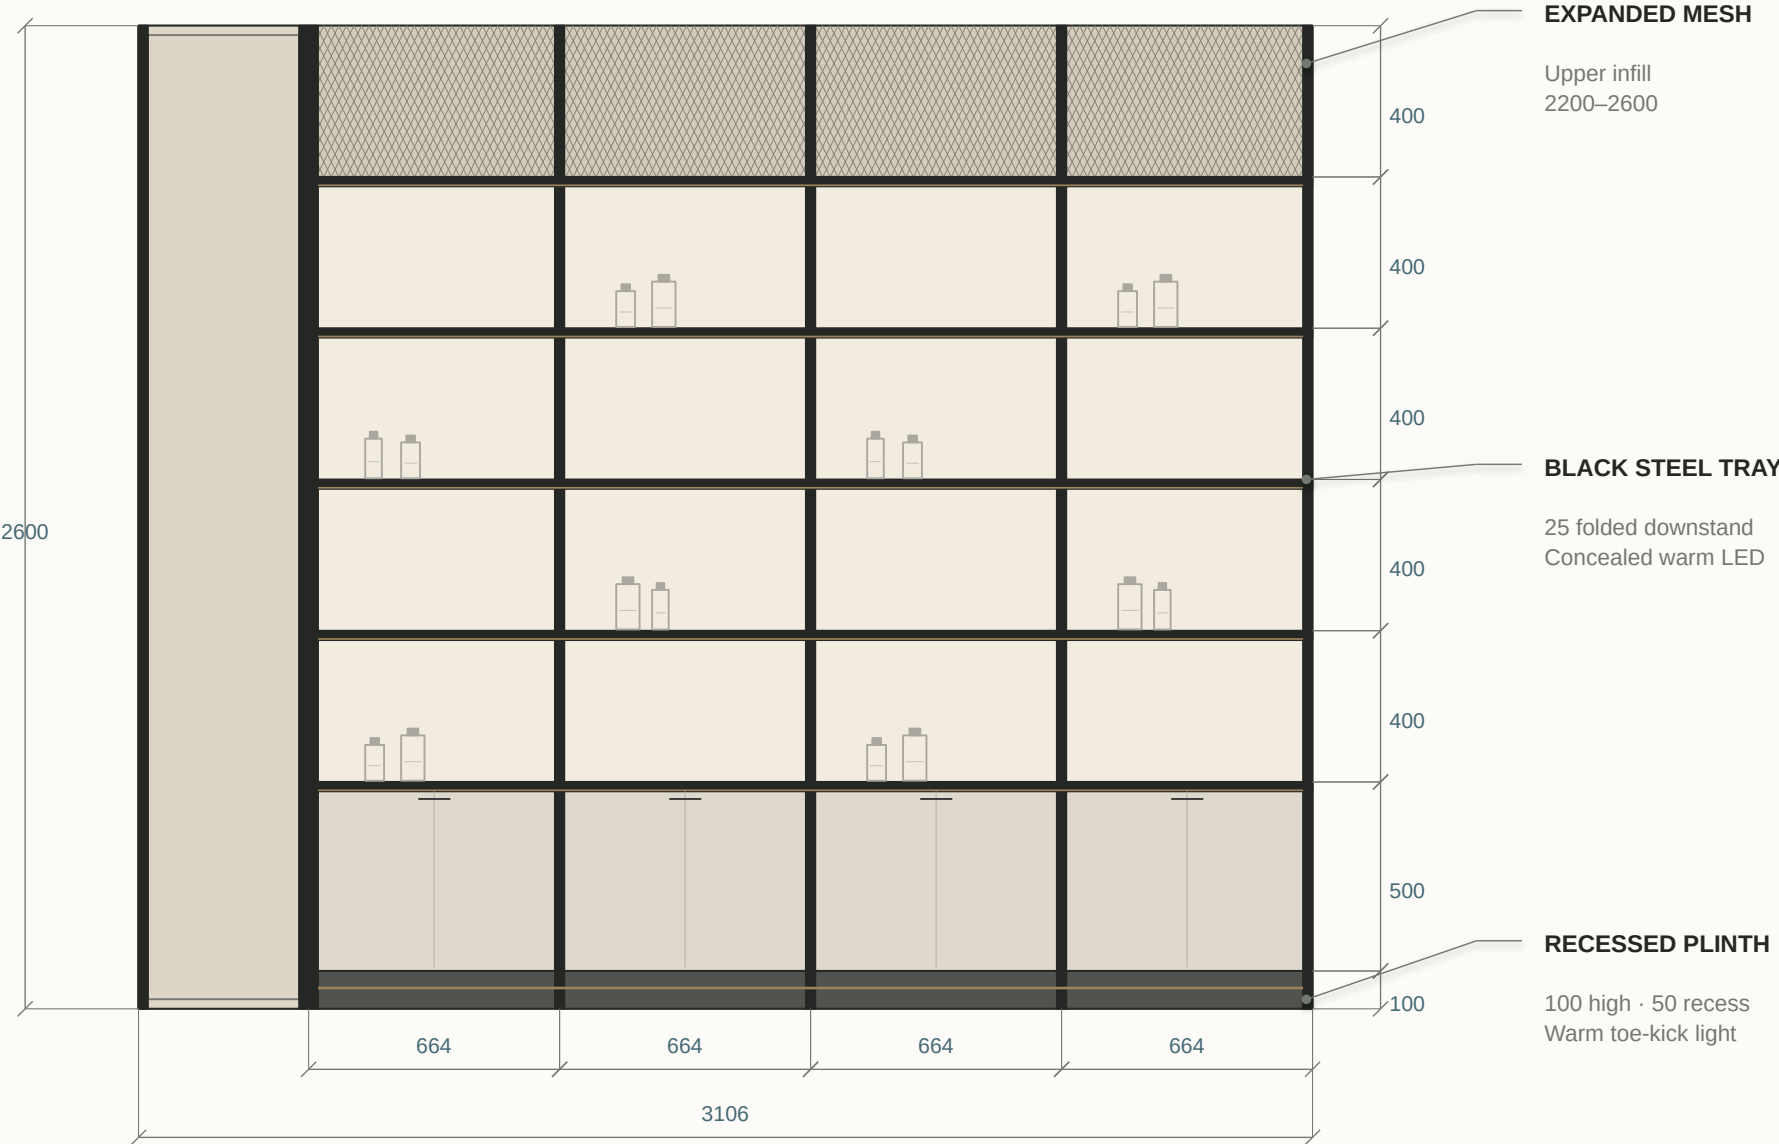

INDICATIVE BOTTLES · NOT A STOCK / CAPACITY SCHEDULE

SHELF / FRONT EDGE


SECTION 1:2

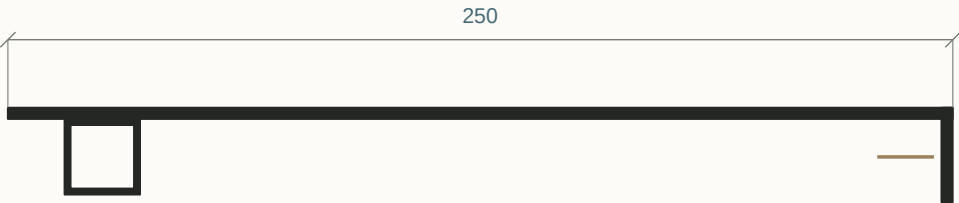

3 mm folded tray · 25 front downstand
20 × 20 × 1.6 support · LED profile TBC #16

CABINET / PLINTH

SECTION 1:5

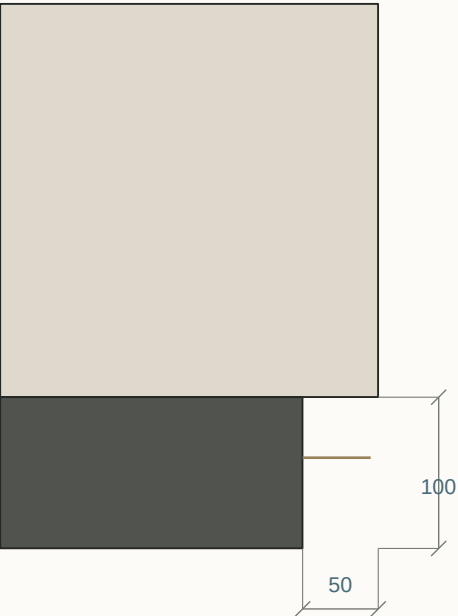


100 high · 50 recess · warm toe-kick LED

RIGHT DISPLAY / INTERNAL ELEVATION


Developed display elevation · interfaces + material codes · bottles indicative only

BLACK STEEL / NEUTRAL PPC / EXPANDED MESH / 3000 K LED

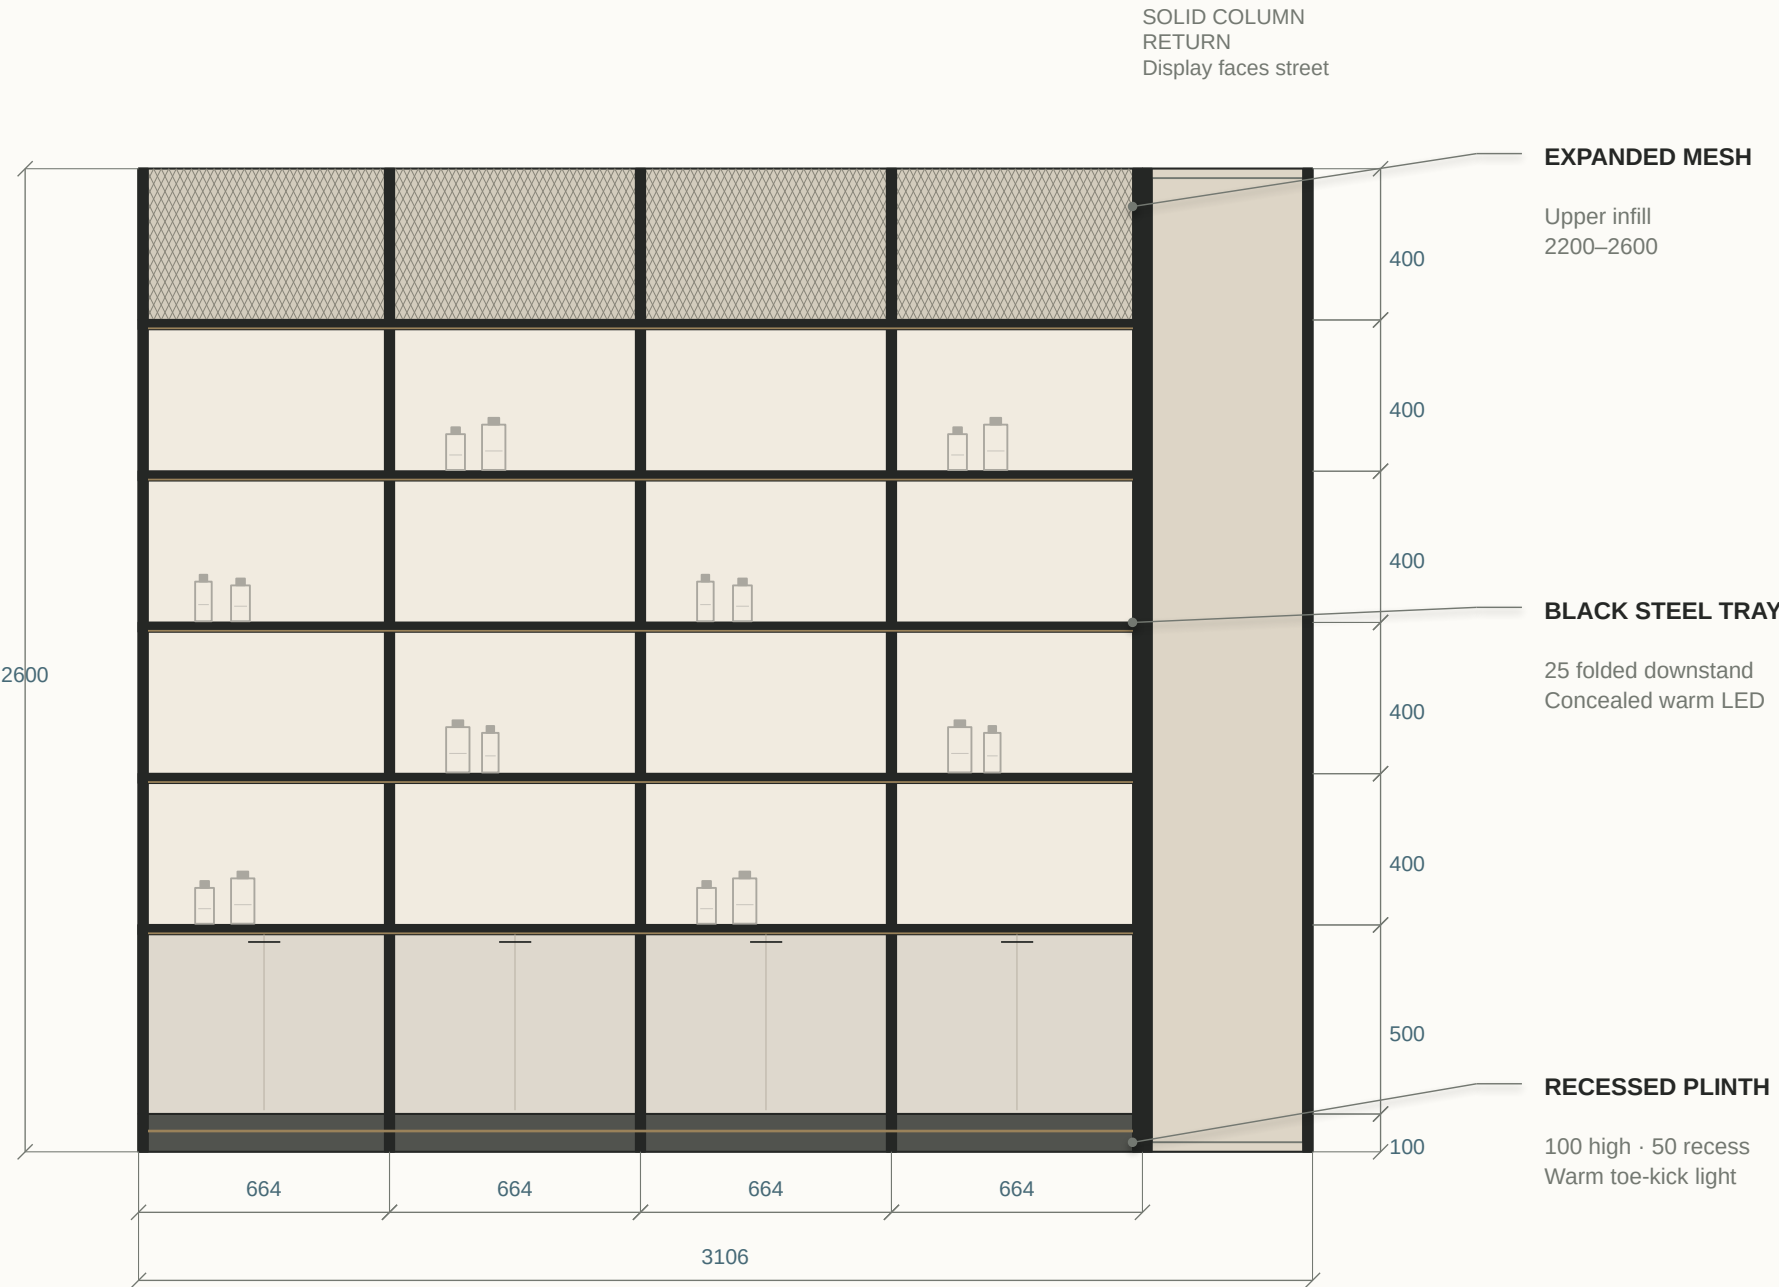


SHELF / FRONT EDGE

SECTION 1:2

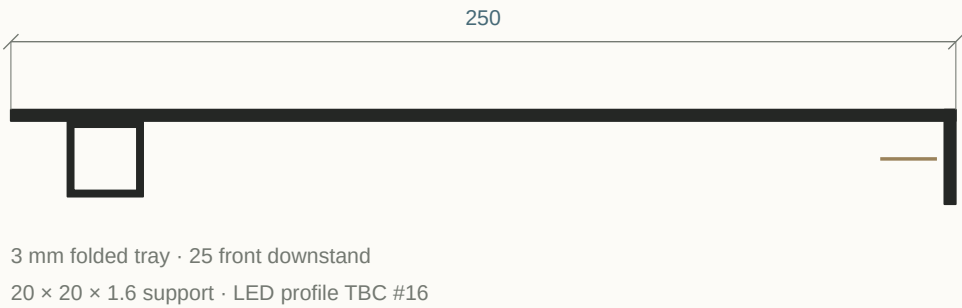

CABINET / PLINTH

SECTION 1:5

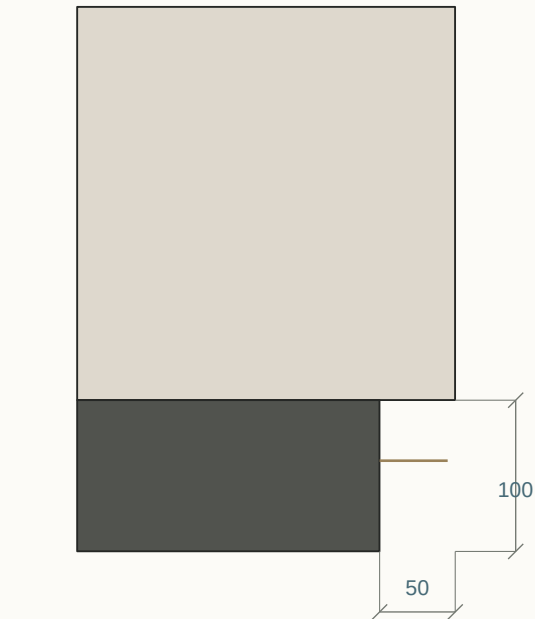


100 high · 50 recess · warm toe-kick LED

INDICATIVE BOTTLES · NOT A STOCK / CAPACITY SCHEDULE

SPATIAL ASSEMBLY / CUTAWAY AXONOMETRIC



Spatial cutaway · orthographic projection · direct material and interface annotations

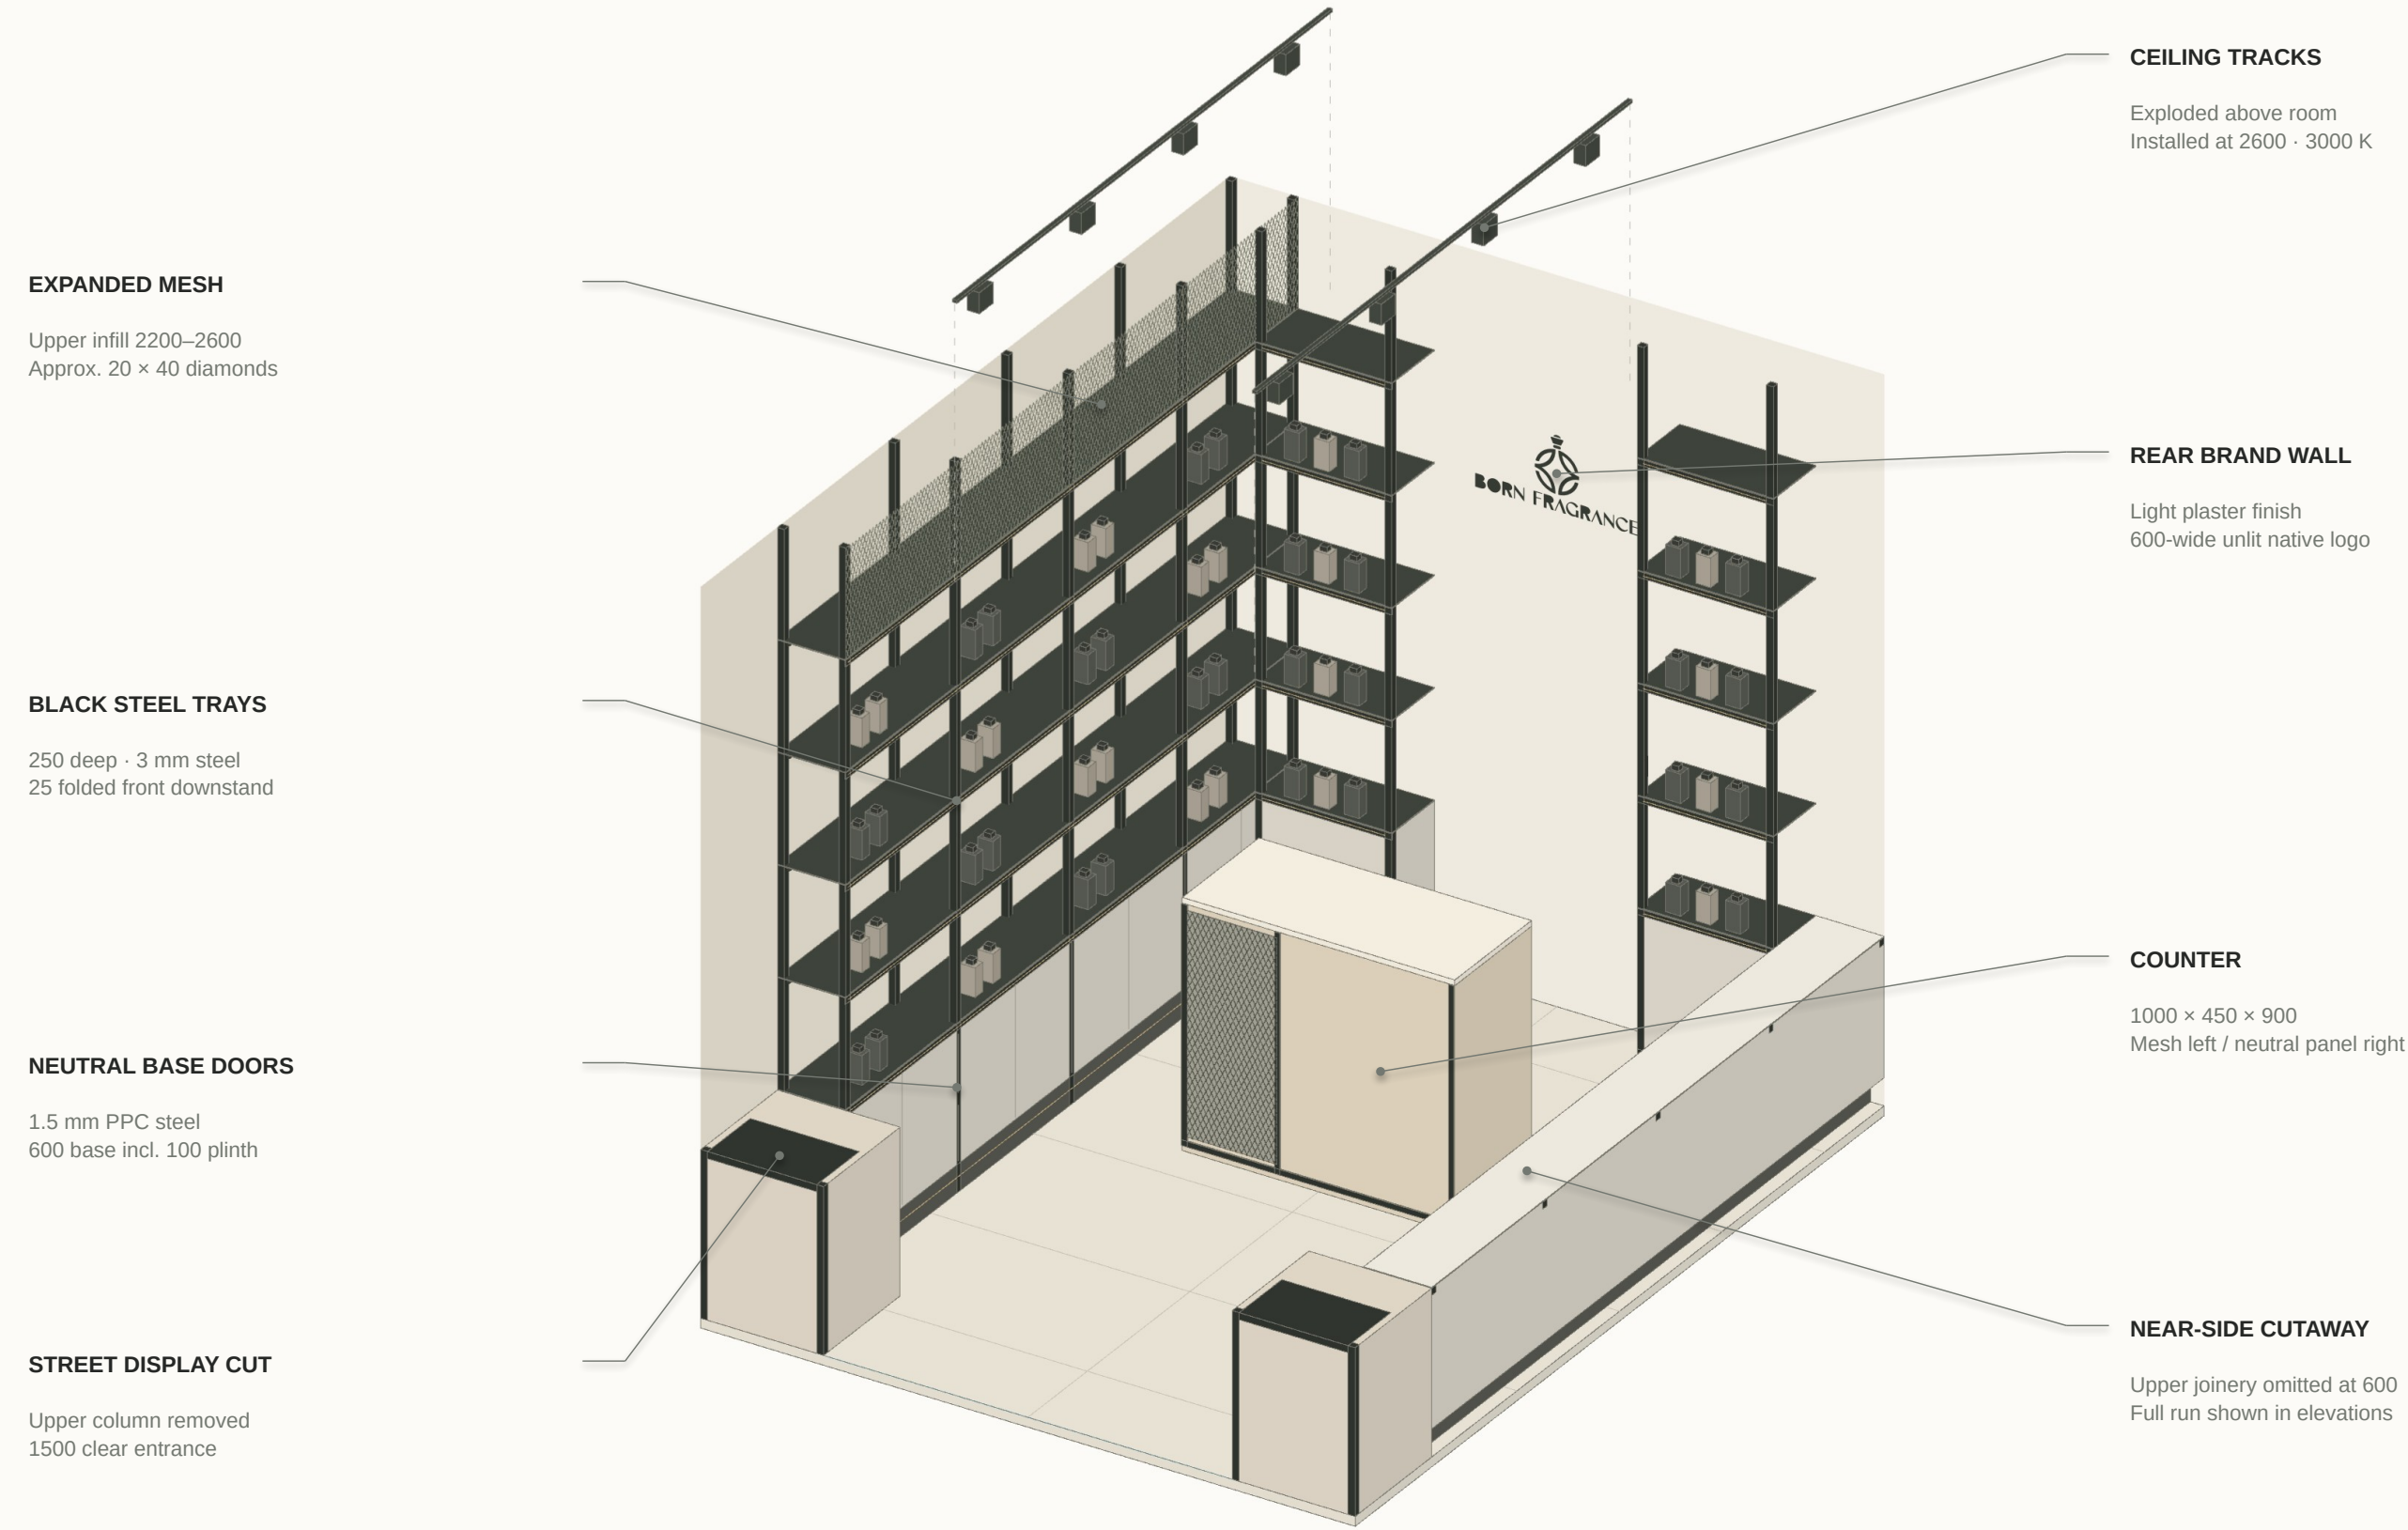

ORTHOGRAPHIC CUTAWAY · NTS · ceiling plane removed