
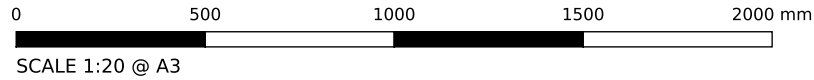


MATERIALS (LOCKED)

M1 Raw textured light plaster
M2 25x25x1.6 / 20x20x1.6 MS SHS, matte black PPC
M3 ~20x40 diamond expanded mesh, black
M4 1200x600 stone-look porcelain floor
L1 Concealed 3000 K LED under shelves
Heights not listed are TBC - never scaled.

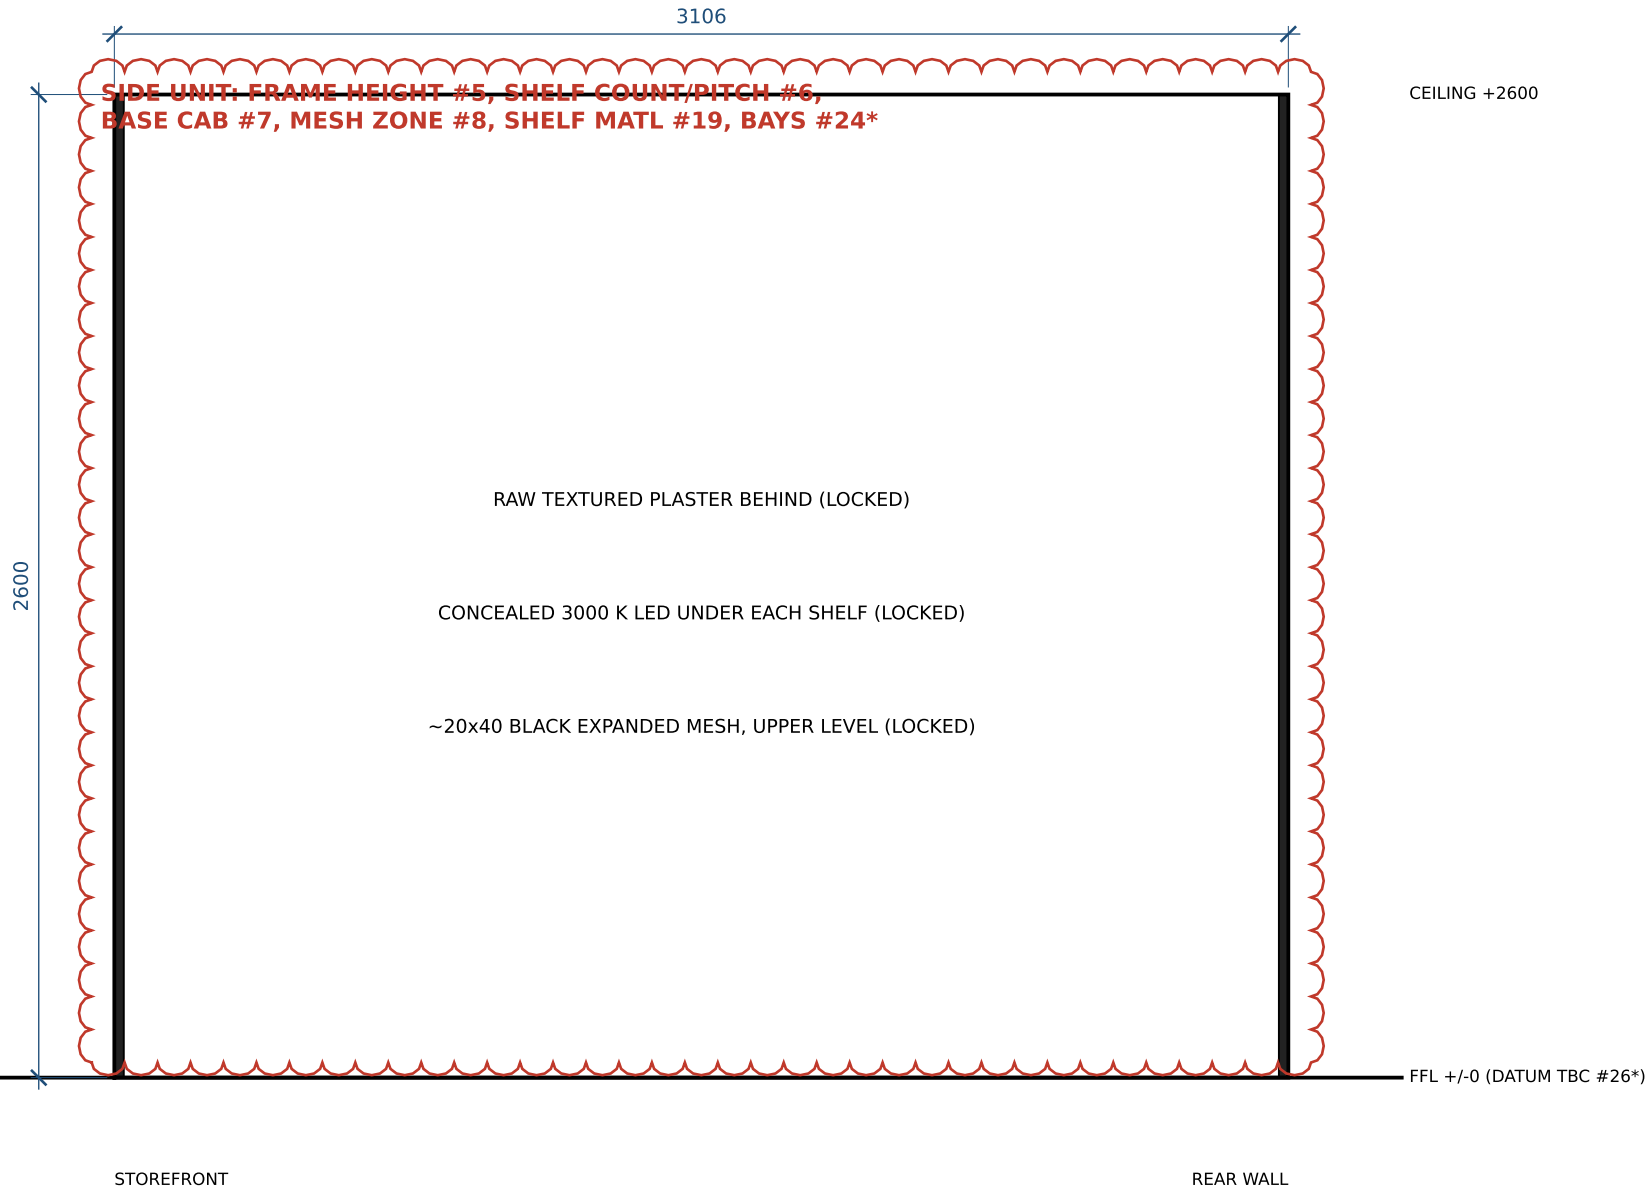

BORN FRAGRANCE

PROJECT BORN FRAGRANCE - shop fit-out

SHEET **SD-07**

TITLE **LEFT ELEVATION (INTERNAL)**

SCALE 1:20 @ A3

DATE 2026-10-05

REV 00 - preliminary

SPEC spec/SHOP_SPEC.json @ e1fbc1c

DRAWN Claude Code (AI), for owner review

TBC ITEMS ON THIS SHEET

- #5 Display frame height (to ceiling or stopped short)
- #6 Shelf count and pitch per bay
- #7 Base cabinet height and door type
- #8 Mesh extent on side walls
- #9 Rear wall bay width, shelf count, logo size and height
- #18 Storefront display column depth, and shelf facing (street, shop or both)
- #19 Shelf material and thickness (render board: "black metal shelf")
- #24* Side bay count, widths and upright spacing

* proposed item, not yet in spec/TBC.md
TBC items are shown in revision clouds.
Dimensions computed from SHOP_SPEC.json.
Do not scale from the render.

PRELIMINARY - NOT FOR CONSTRUCTION