


A small space. A distinctive presence.

BORN FRAGRANCE / RETAIL INTERIOR

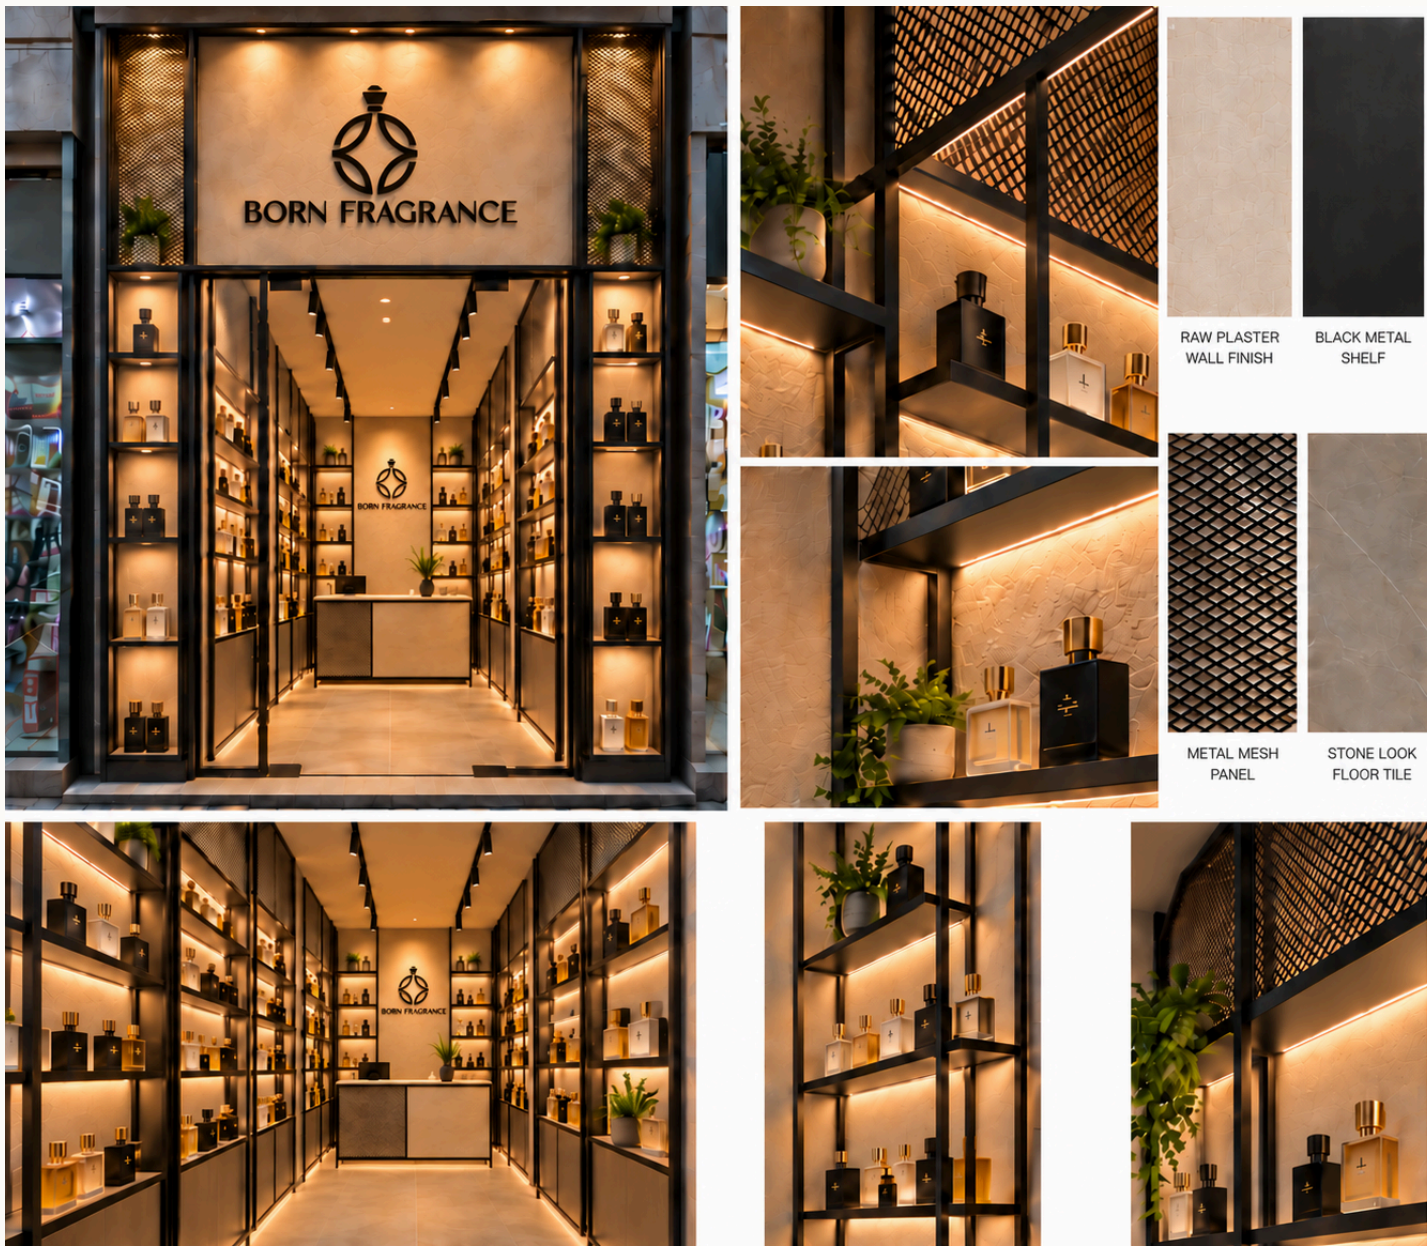

Approved render — design intent only. Do not measure. Styling props shown in the render are excluded from the technical scope.

Fine black steel lines, light textured surfaces and warm integrated lighting create a focused setting for fragrance.

2400 × 3106 mm

Internal size · survey pending

2600 mm


Ceiling height

Rev A

Coordination issue

The layout

01 / DISPLAY & FURNITURE PLAN

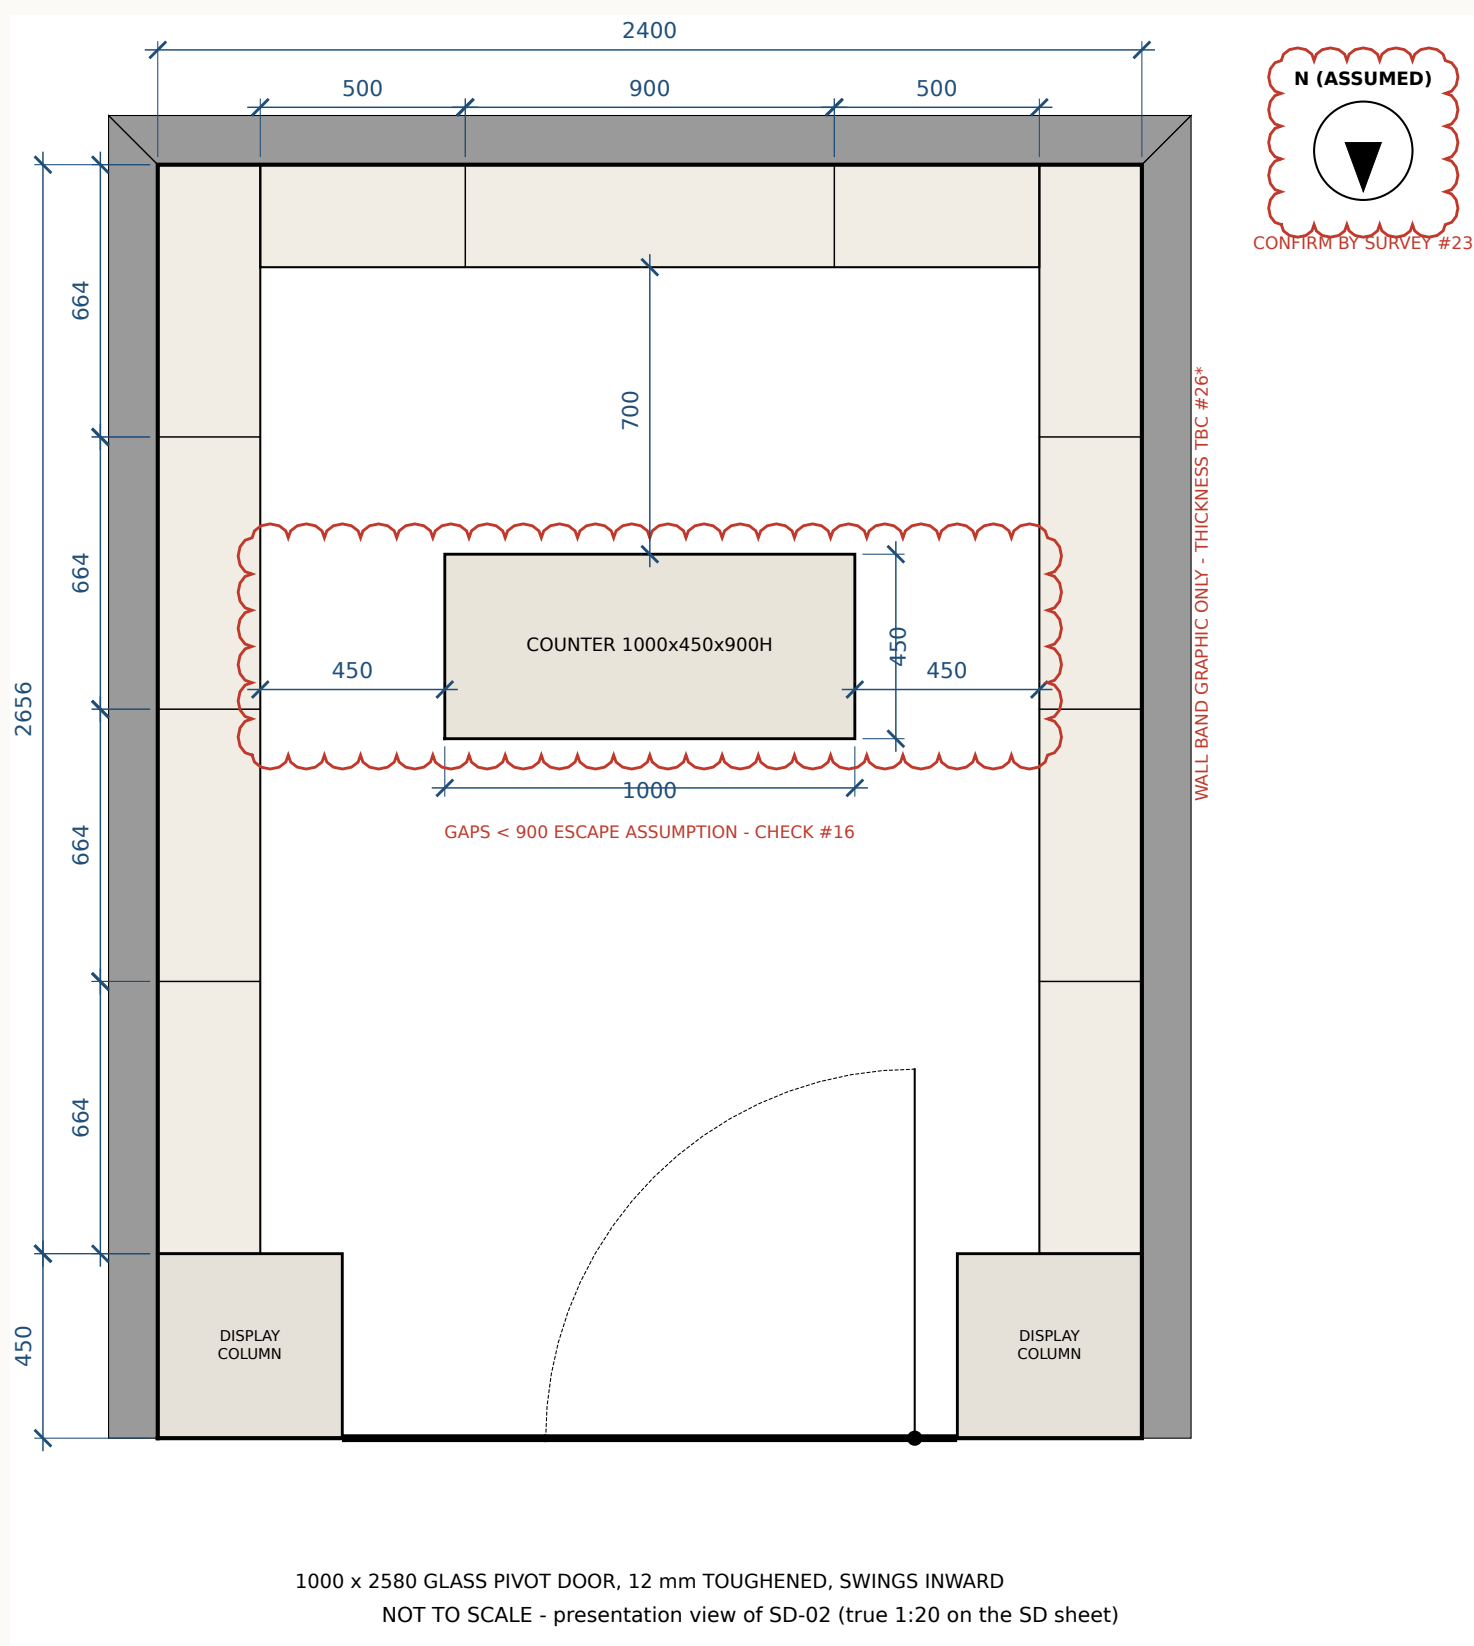

NOT TO SCALE · presentation view of SD-02


Side display runs: 2656 mm, four 664 mm modules per side.

Counter: 1000 × 450 × 900 mm, centred at x=700–1700; rear edge y=2156, 700 mm to rear unit.

CHECK — TBC #16: 450 mm each side of counter. Consultant to confirm escape and staff access.

The street presence

02 / STOREFRONT

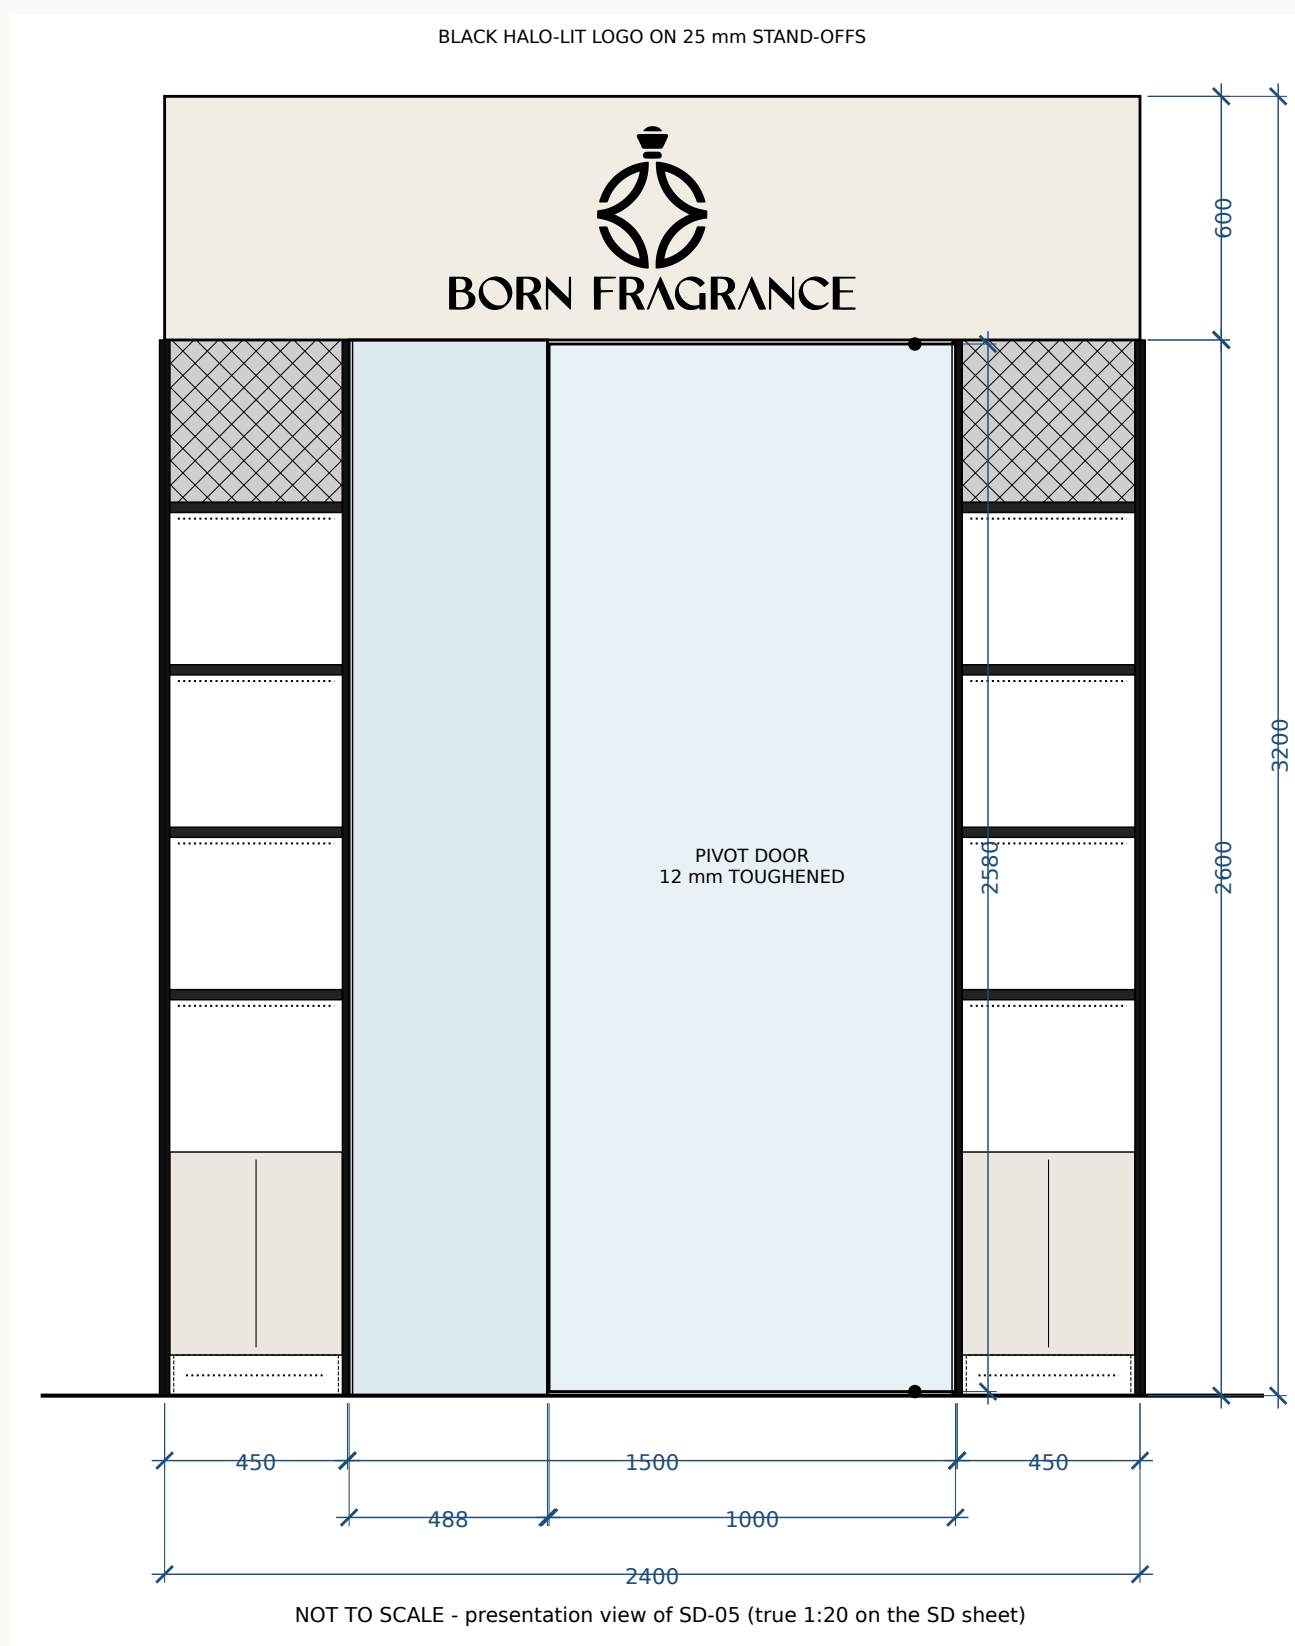

NOT TO SCALE · presentation view of SD-05


Frontage: $450 + 1500 + 450 = 2400$ mm; columns 450×450 mm face the street.

Pivot door: 1000 W $\times$ 2580 H mm. Fixed glass: 488 mm; glazier to confirm gaps.

Exterior logo: 1000×452.98 mm, black halo-lit on 25 mm stand-offs; 600 mm sign band, 3200 mm overall height.

The focal wall

03 / REAR ELEVATION

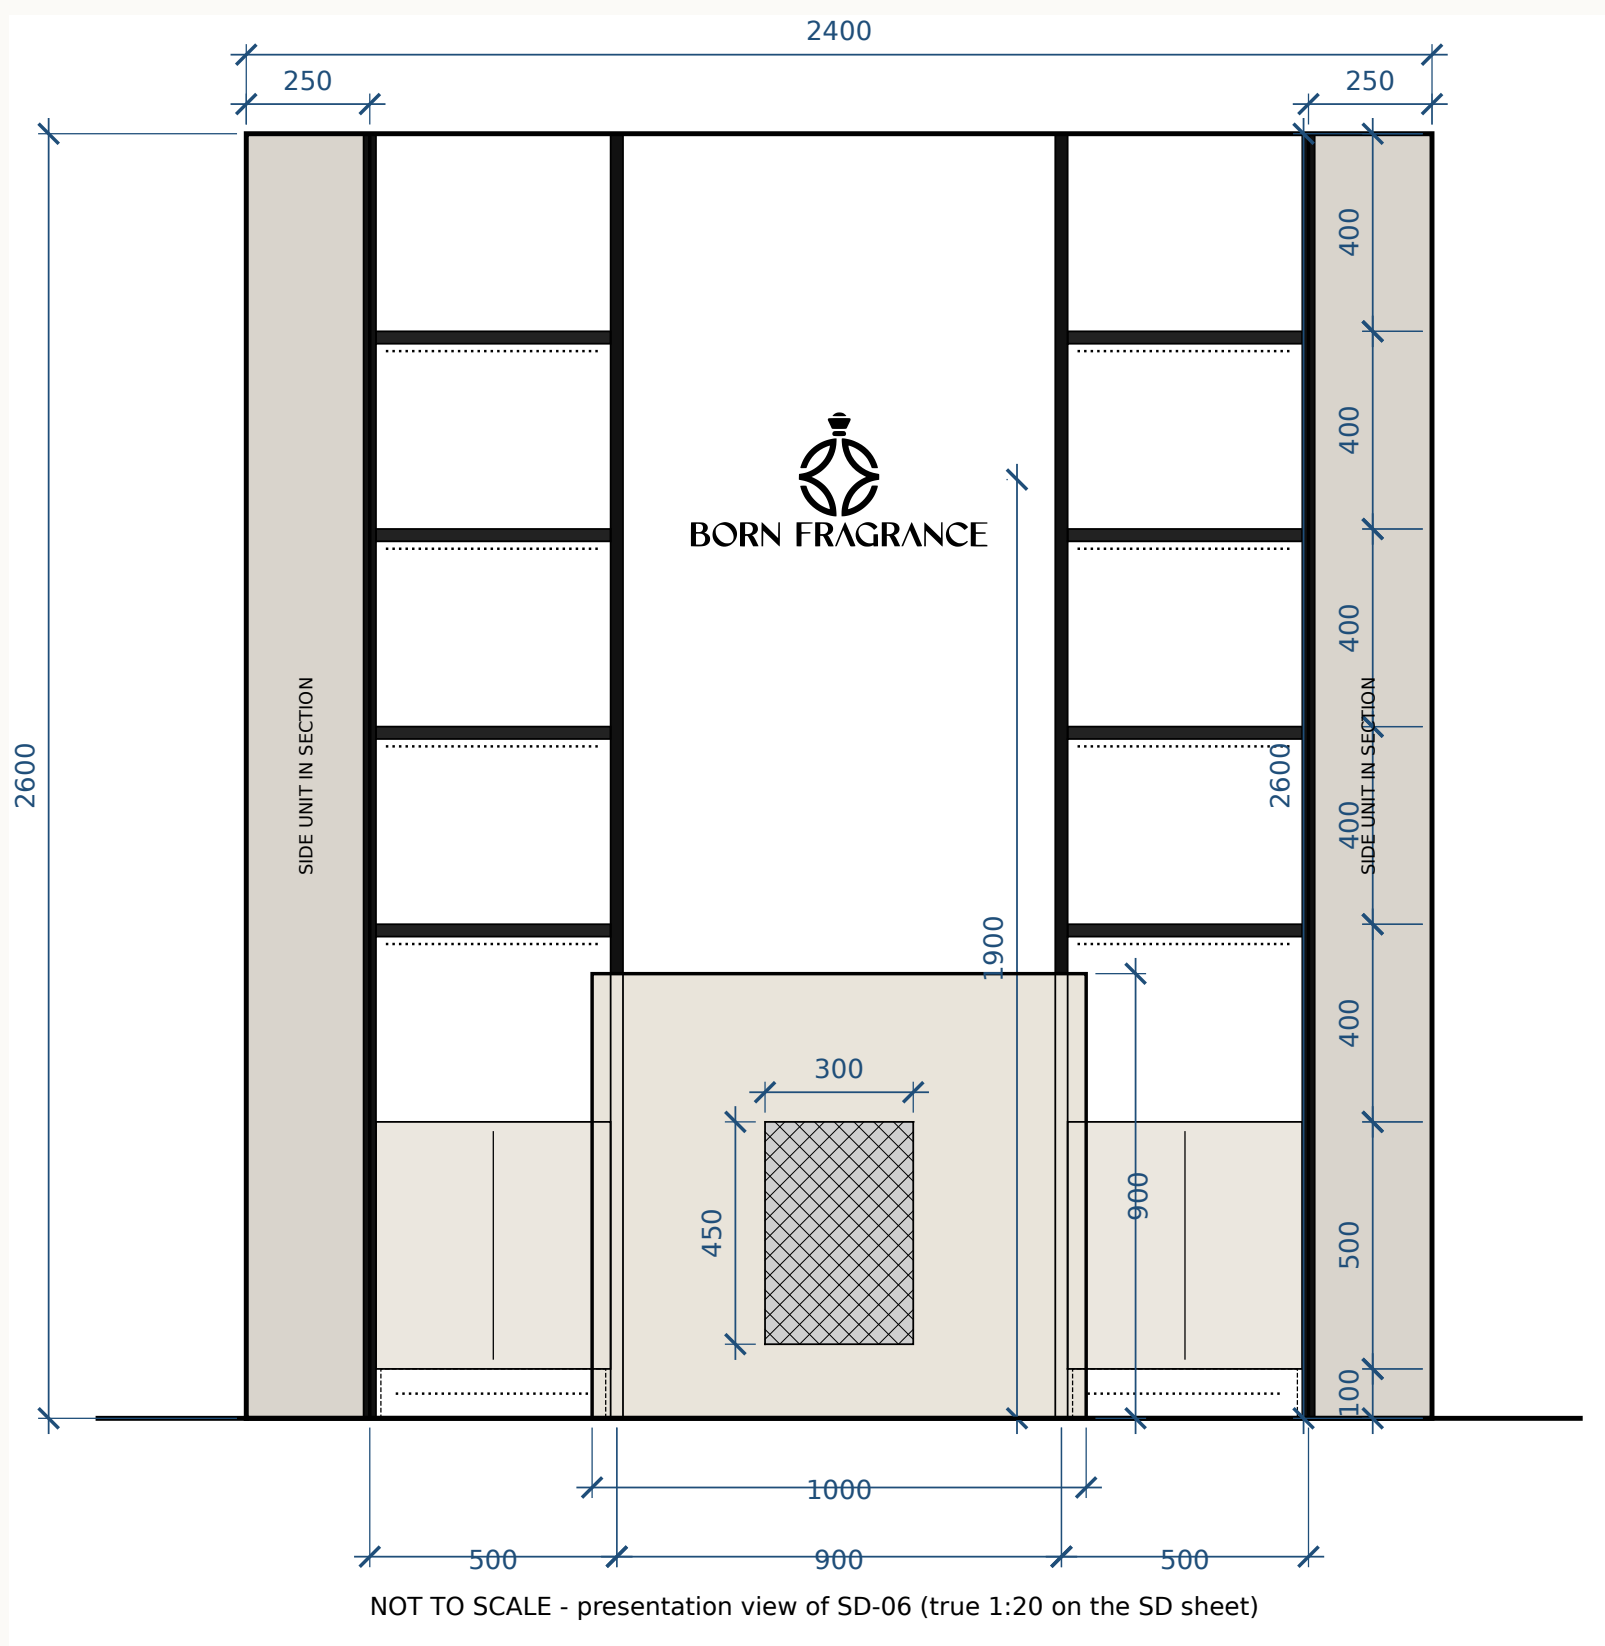

NOT TO SCALE · presentation view of SD-06


Rear zones: $500 + 900 + 500 = 1900$ mm between side units; rear unit 250 mm deep.

Interior logo: 600×271.8 mm, centred at 1900 mm AFFL, non-illuminated black.

No mesh on rear display bays. Counter mesh insert: 300×450 mm, centred, bottom 150 mm above floor.

The display system

04 / LEFT ELEVATION

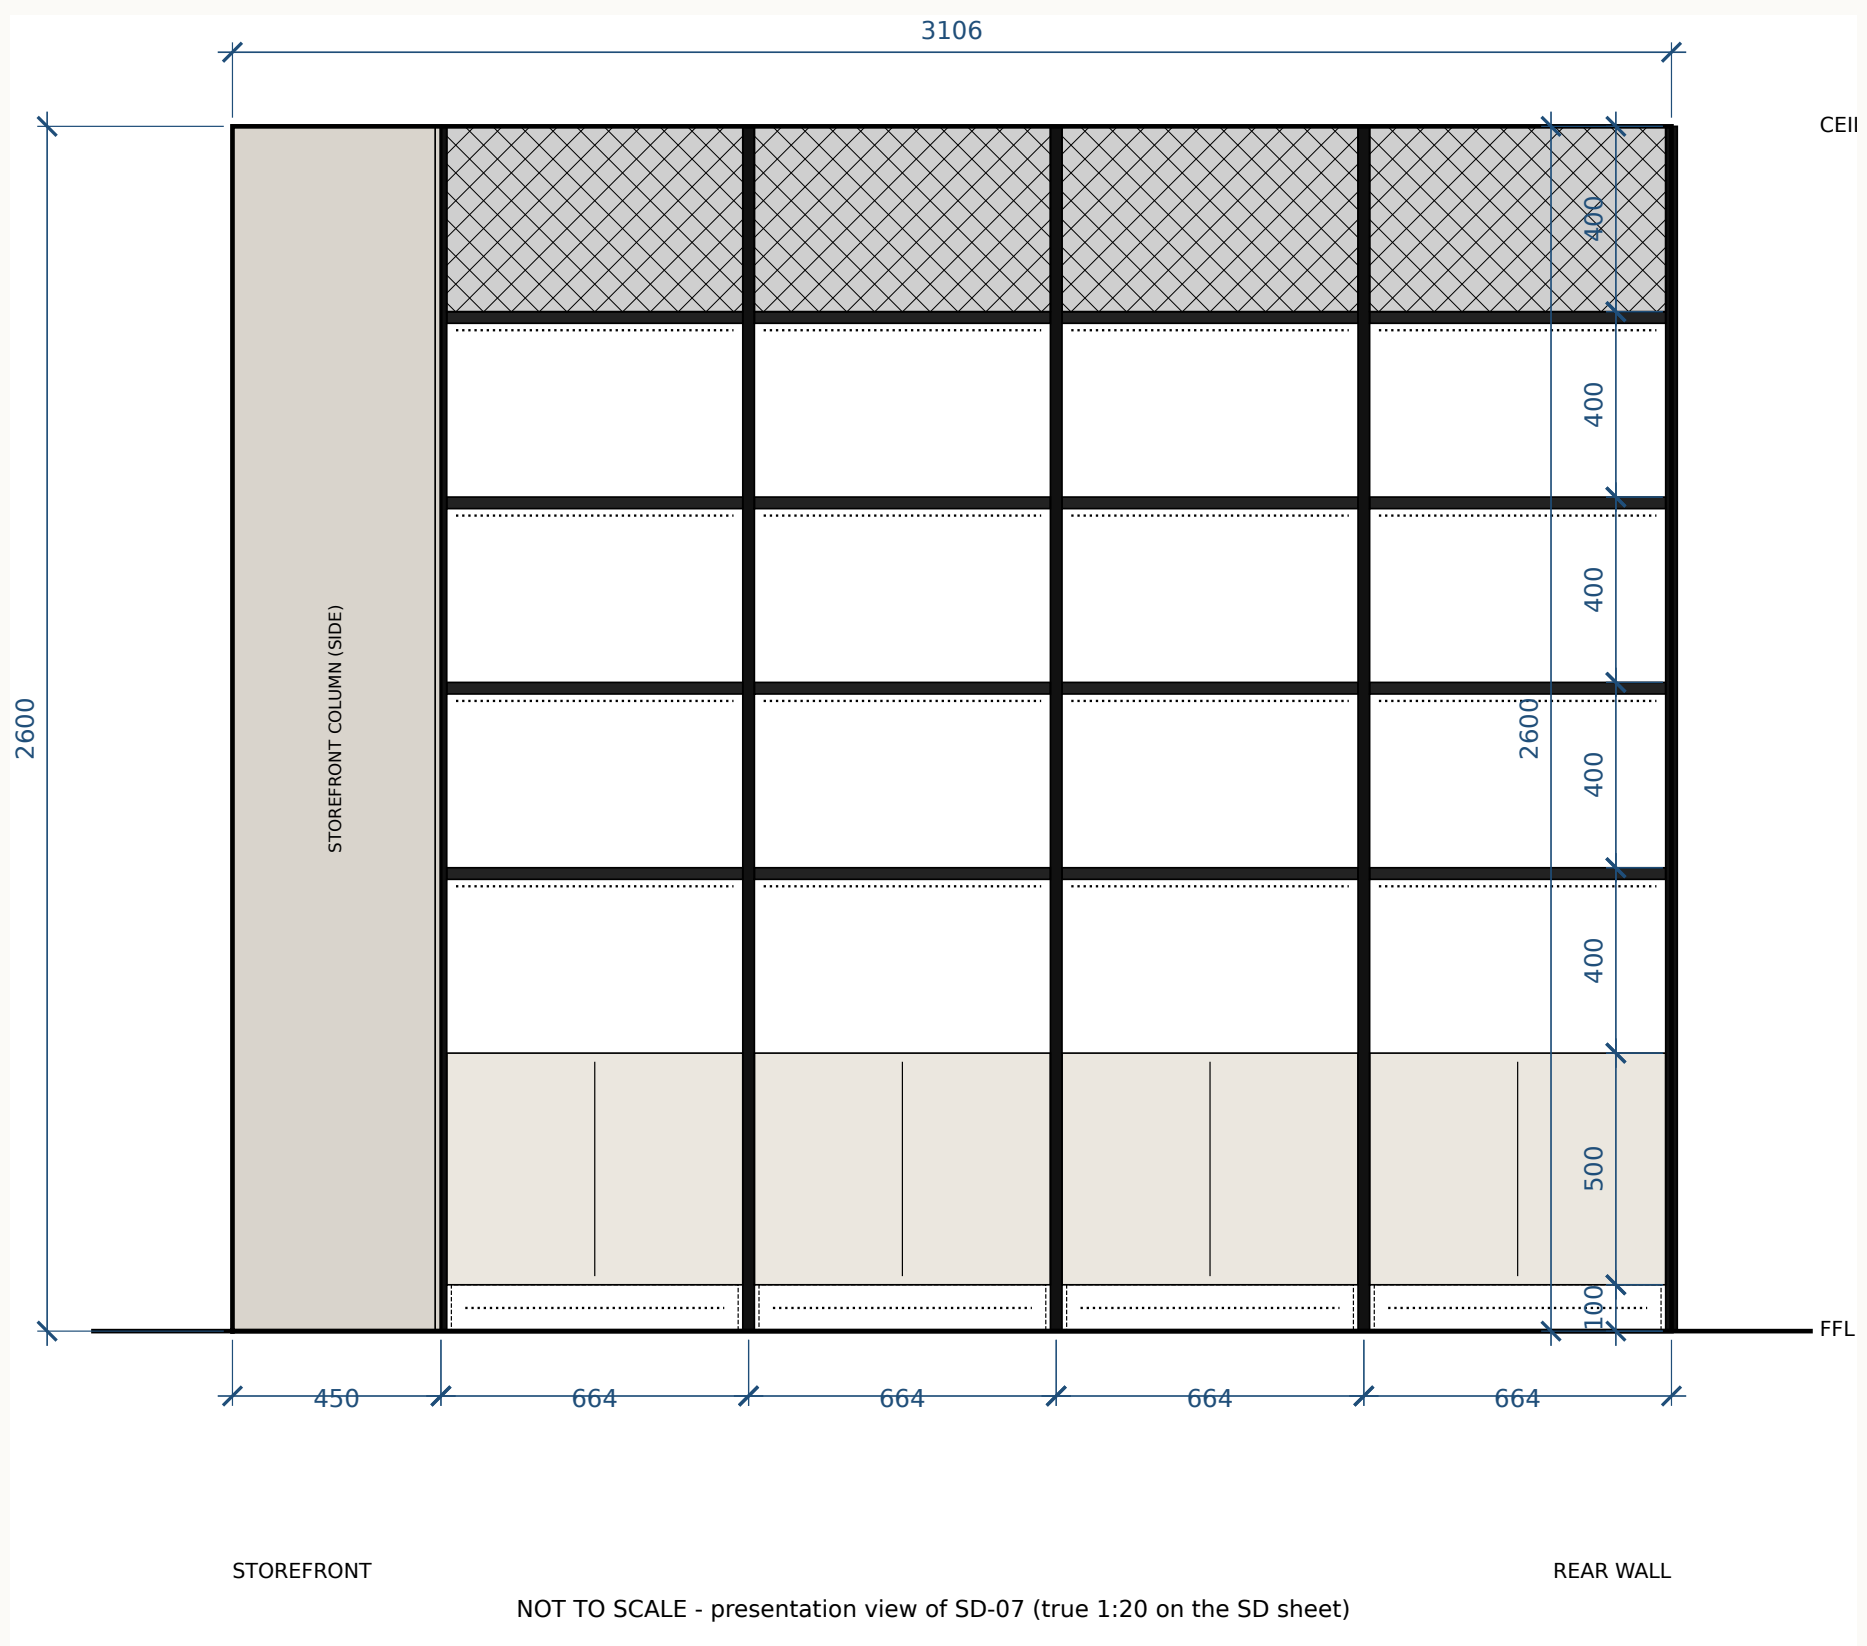

NOT TO SCALE · presentation view of SD-07

Shelf levels: 600, 1000, 1400, 1800 and 2200 mm AFFL; frame height 2600 mm.


Front mesh infill: 2200–2600 mm. Shelf depth: 250 mm.

3 mm folded MS shelves with 25 mm front downstand concealing LED profile.

600 mm base cabinet includes a 100 H × 50 D mm recessed plinth.

A continuous rhythm

05 / RIGHT ELEVATION

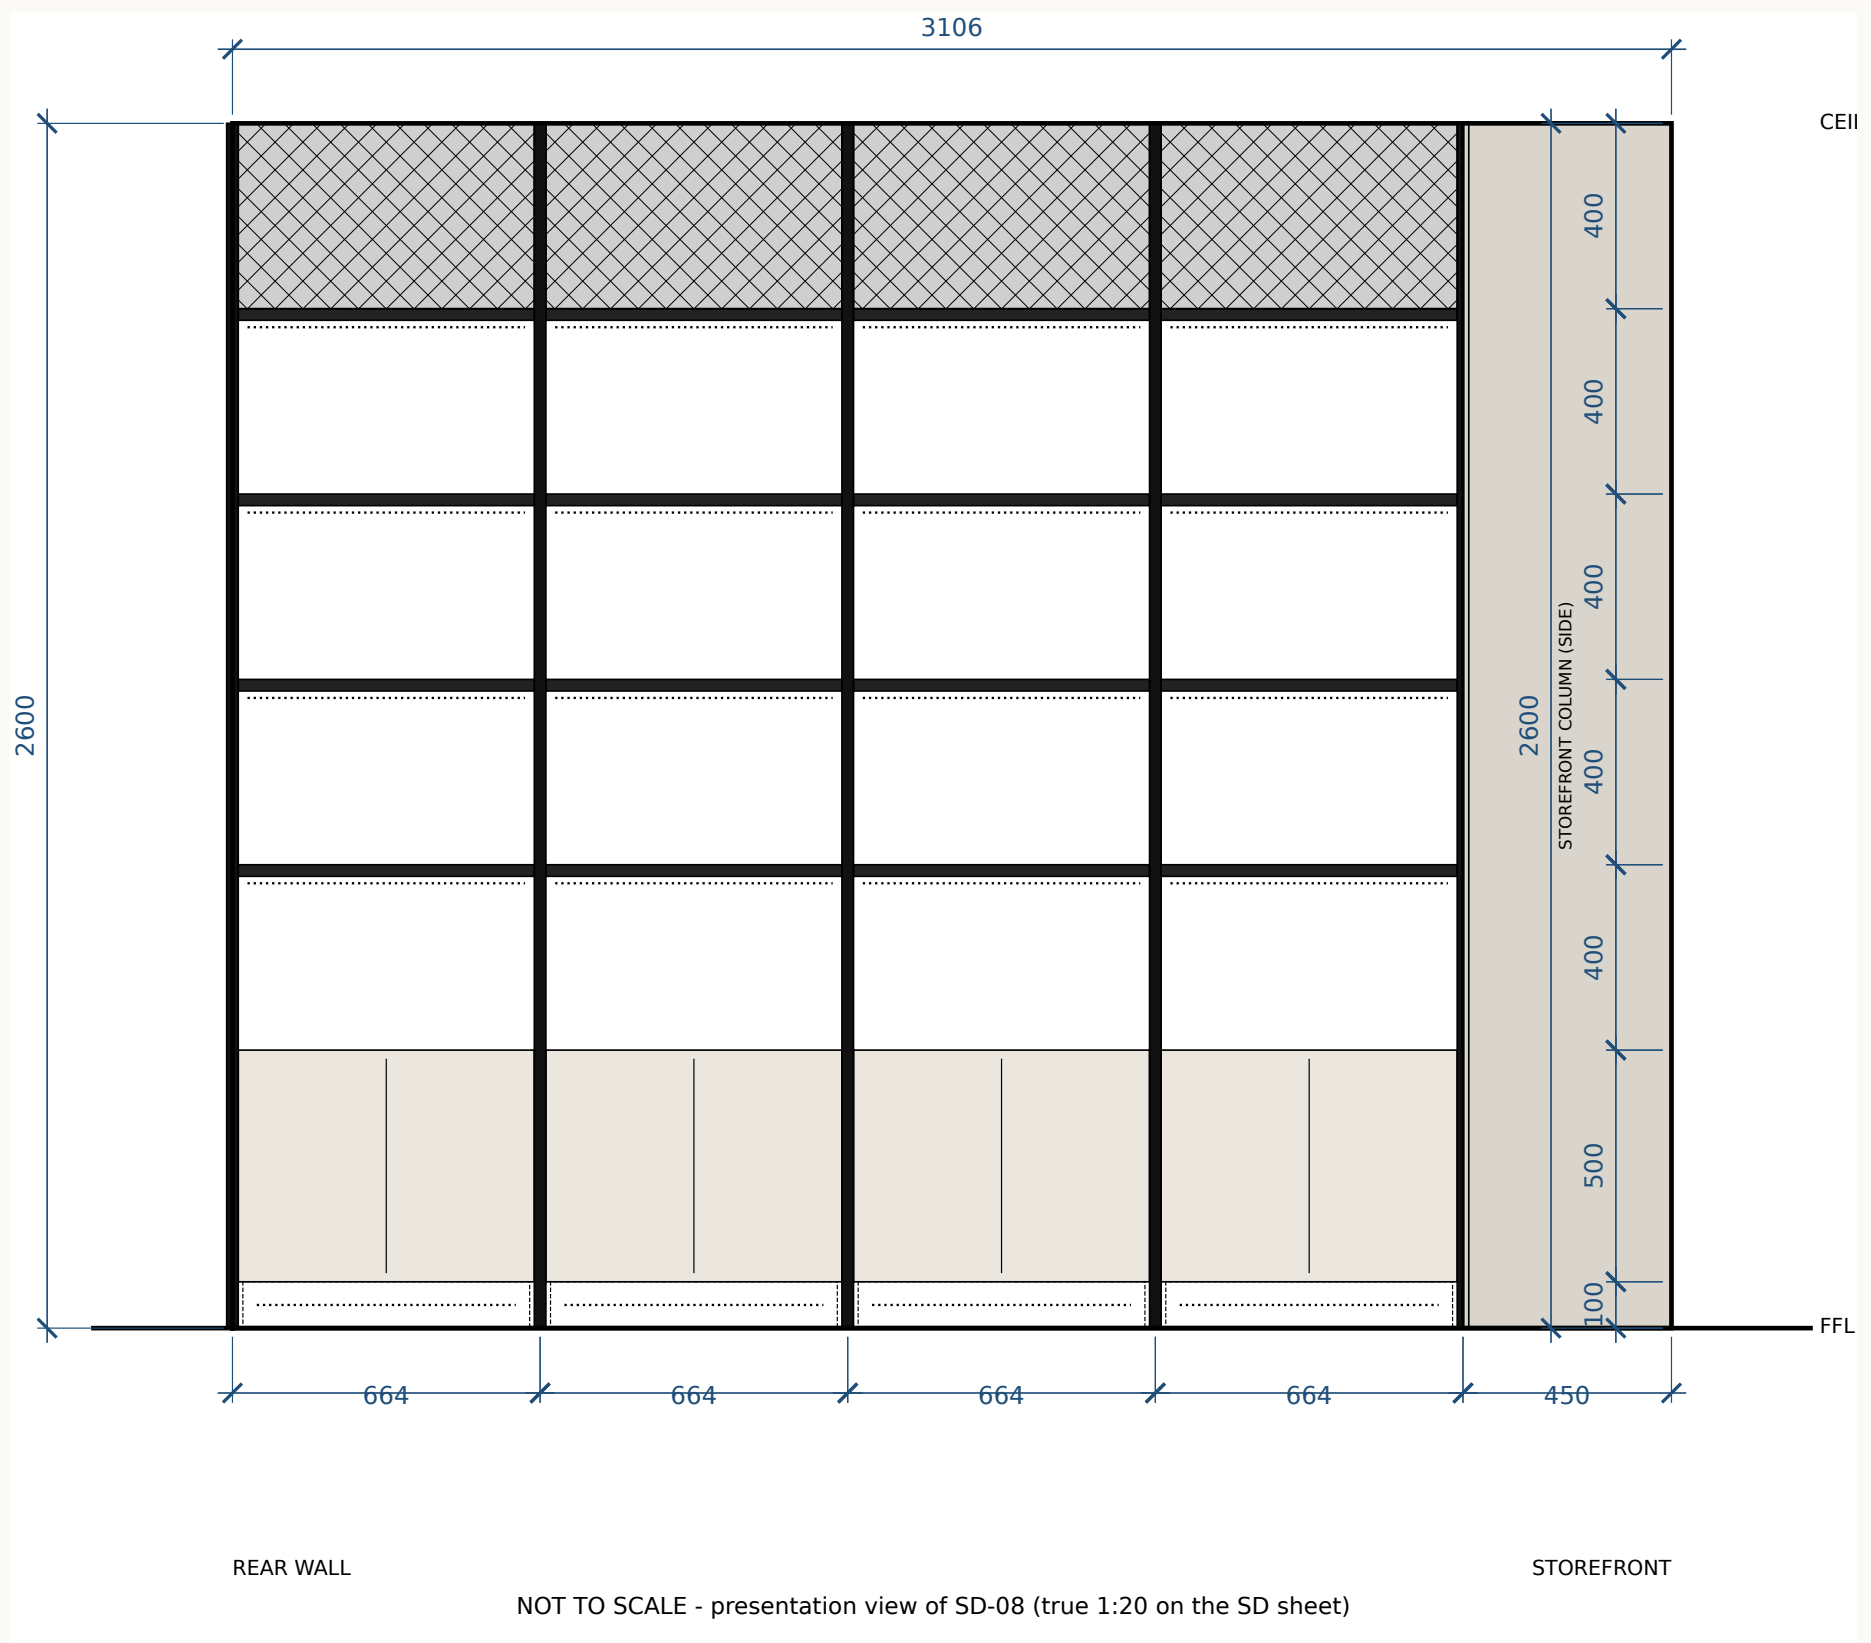

NOT TO SCALE · presentation view of SD-08


Four 664 mm bays over each 2656 mm side run, behind storefront columns to the rear wall.

1.5 mm powder-coated steel cabinet doors: light neutral, flush and handleless.

CHECK — TBC #16: fix frames to floor and walls; no fixing to gypsum ceiling. Consultant to confirm anchors and substrate.

Light, carefully placed

06 / CEILING & INTEGRATED LIGHTING

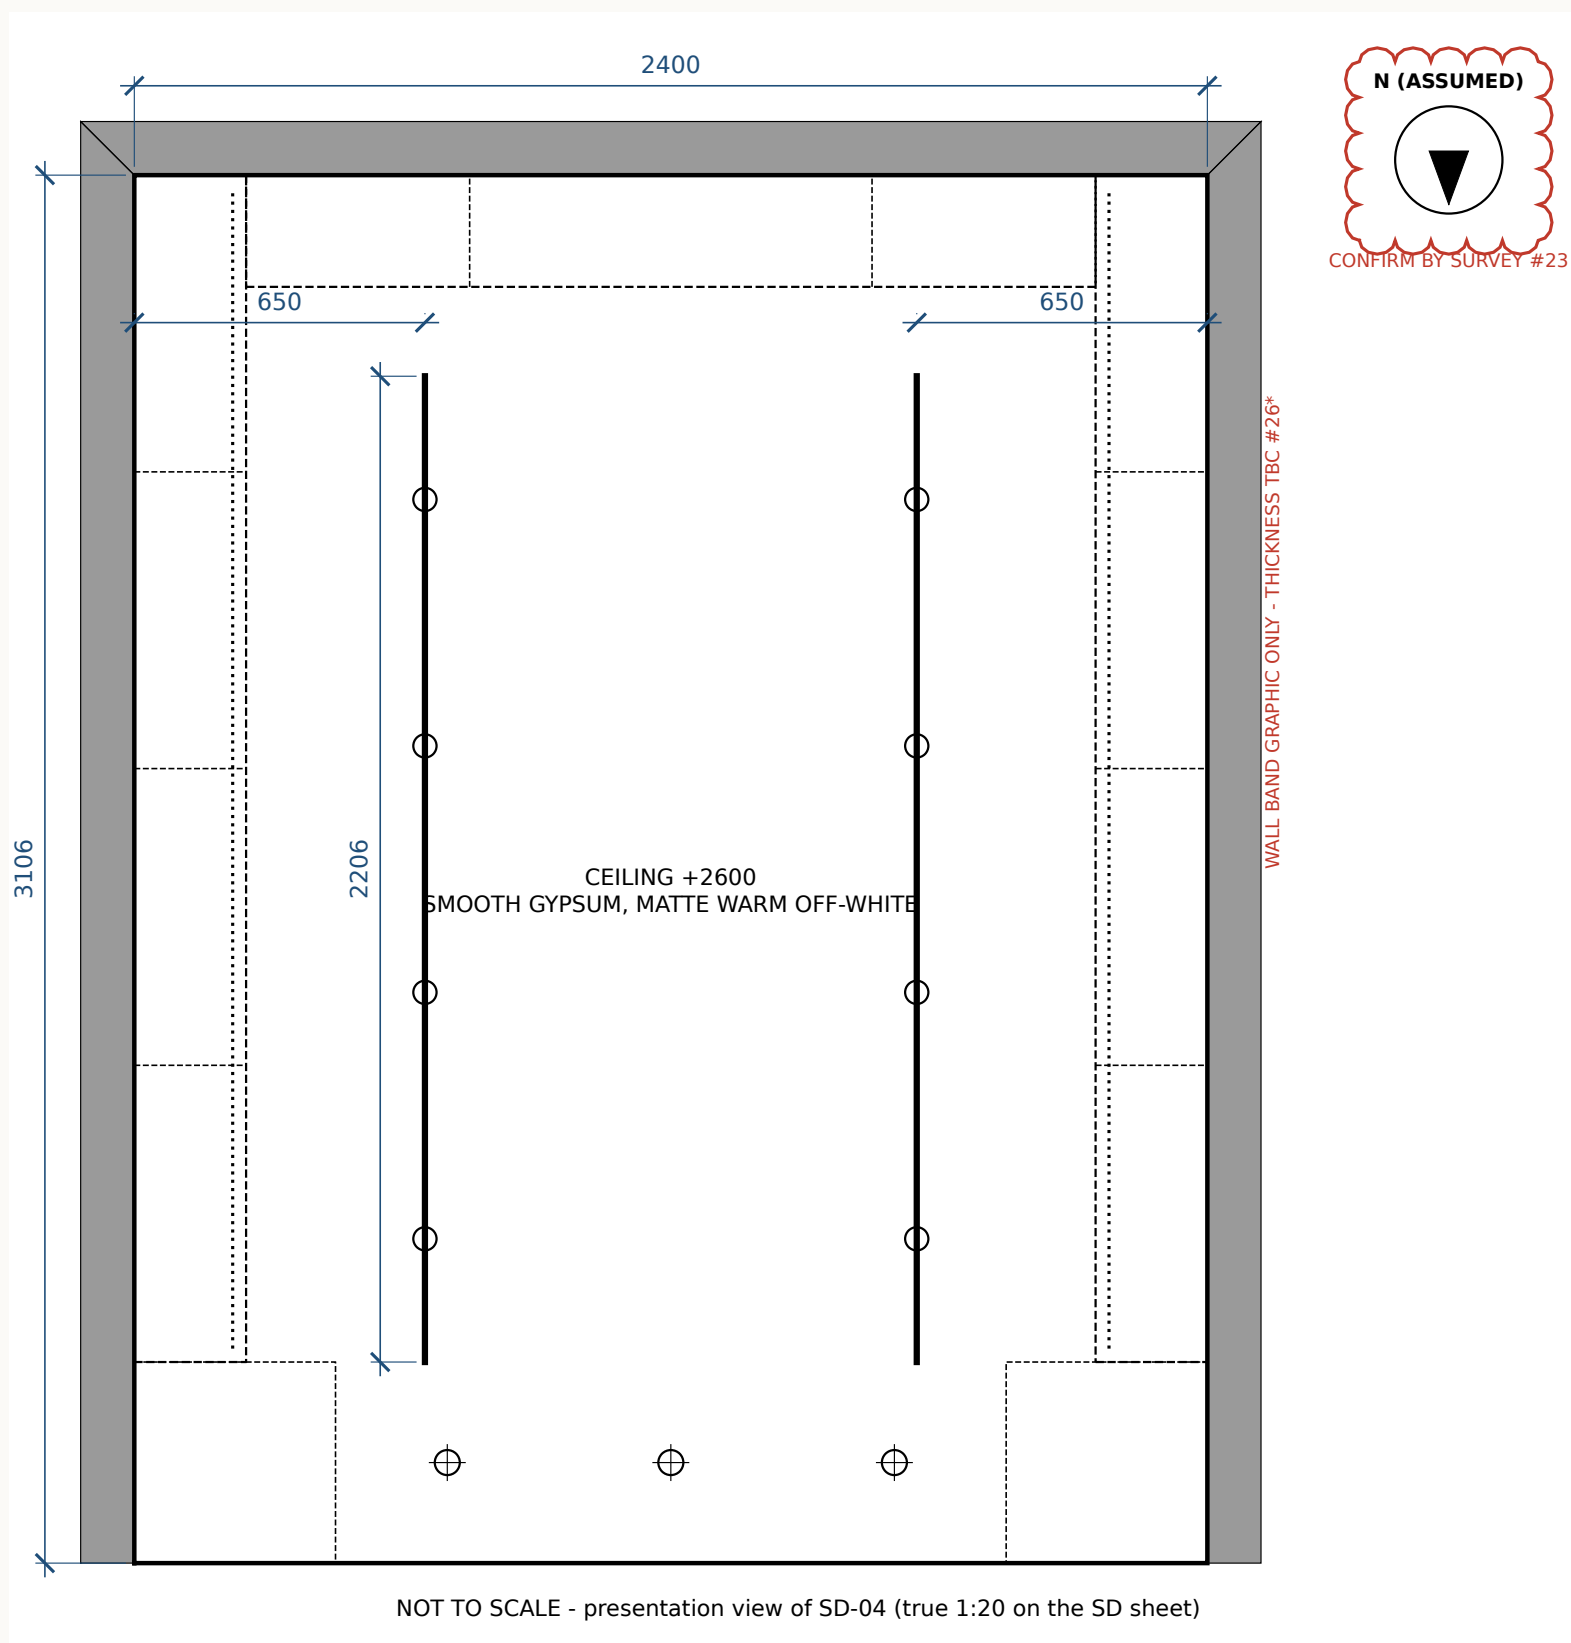

NOT TO SCALE · presentation view of SD-04


3000 K lighting: two black tracks at x=650/1750, 2206 mm long, four adjustable spots per track.

Three recessed downlights; smooth gypsum ceiling, matte warm off-white.

Concealed shelf LEDs and two 2656 mm toe-kick runs within recessed plinths.


Material character

07 / FINISHES & FABRICATION

 


Black steel

Matte black powder coat. Main frame 25×25×1.6 MS SHS; secondary frame 20×20×1.6 MS SHS.

 


Light-neutral steel

1.5 mm powder-coated steel cabinet doors; flush, handleless. No timber.

 


Textured plaster

Raw light textured plaster. Swatch is indicative; approve physical finish sample.

 

Stone-look porcelain

1200×600 mm rectified porcelain, 2 mm grout; option A with 5 mm perimeter movement joints.

 

Clear glass

12 mm clear toughened glass pivot door. Glazier to confirm fabrication and hardware.

Palette colours are indicative screen references, not procurement specifications.



Expanded mesh

Black diamond expanded metal, approximately 20×40 mm. Upper side display infill only.

Finishing the picture

08 / COUNTER, CEILING & LIGHT

M7 — counter front and top

Light neutral panel with a simple light-coloured top.

M9 — ceiling

Smooth gypsum, matte warm off-white. Frame fixings must not load the gypsum ceiling.

L1 — lighting

3000 K concealed LEDs, black track spots and recessed downlights.

Floor setting-out

Option A: 1200 mm across, 2 mm grout, 5 mm perimeter joint; end cuts 1194 / 343 mm.

Excluded from the technical scope: timber, brass, decorative arches, heavy joinery, pendants, decorative ceiling features, plants and loose products. Reference boards inform composition only.

Ready for coordination

09 / OPEN ITEMS & SOURCE DOCUMENTS

TBC #4 — finished dimensions

Verify 2400 × 3106 mm clear internal size after plaster before fabrication.

TBC #16 — consultant review

Confirm counter access and escape, frame anchors, substrate capacity, fire and MEP requirements. The 450 mm counter side gaps remain a CHECK.

TBC #23 — orientation

North toward storefront is an assumption pending survey.

TBC #26 — construction and datum

FFL ±0 and 100 mm wall thickness are assumed; confirm construction and datum on site.

Original SD-01–SD-08 technical sheets remain A3 landscape at 1:20. This portrait document is a presentation summary; its drawing views are not to scale.

Source: Claude HANDOFF.md and unchanged SVGs at 294170887075; Rev A spec on main at 0e28b4e.