



SETTING-OUT POINTS (mm, from datum)

- A x=0 y=0 datum, front-left internal corner
- B x=2400 y=0 front-right corner
- C x=2400 y=3106 rear-right corner
- D x=0 y=3106 rear-left corner
- E x=450 y=0 left column inner face
- F x=1950 y=0 right column inner face
- G x=454 y=0 fixed glass
- H x=946 y=0 door leaf
- J x=250 y=- left unit face line
- K x=2150 y=- right unit face line

Glass joints 4 mm (glazier to confirm).

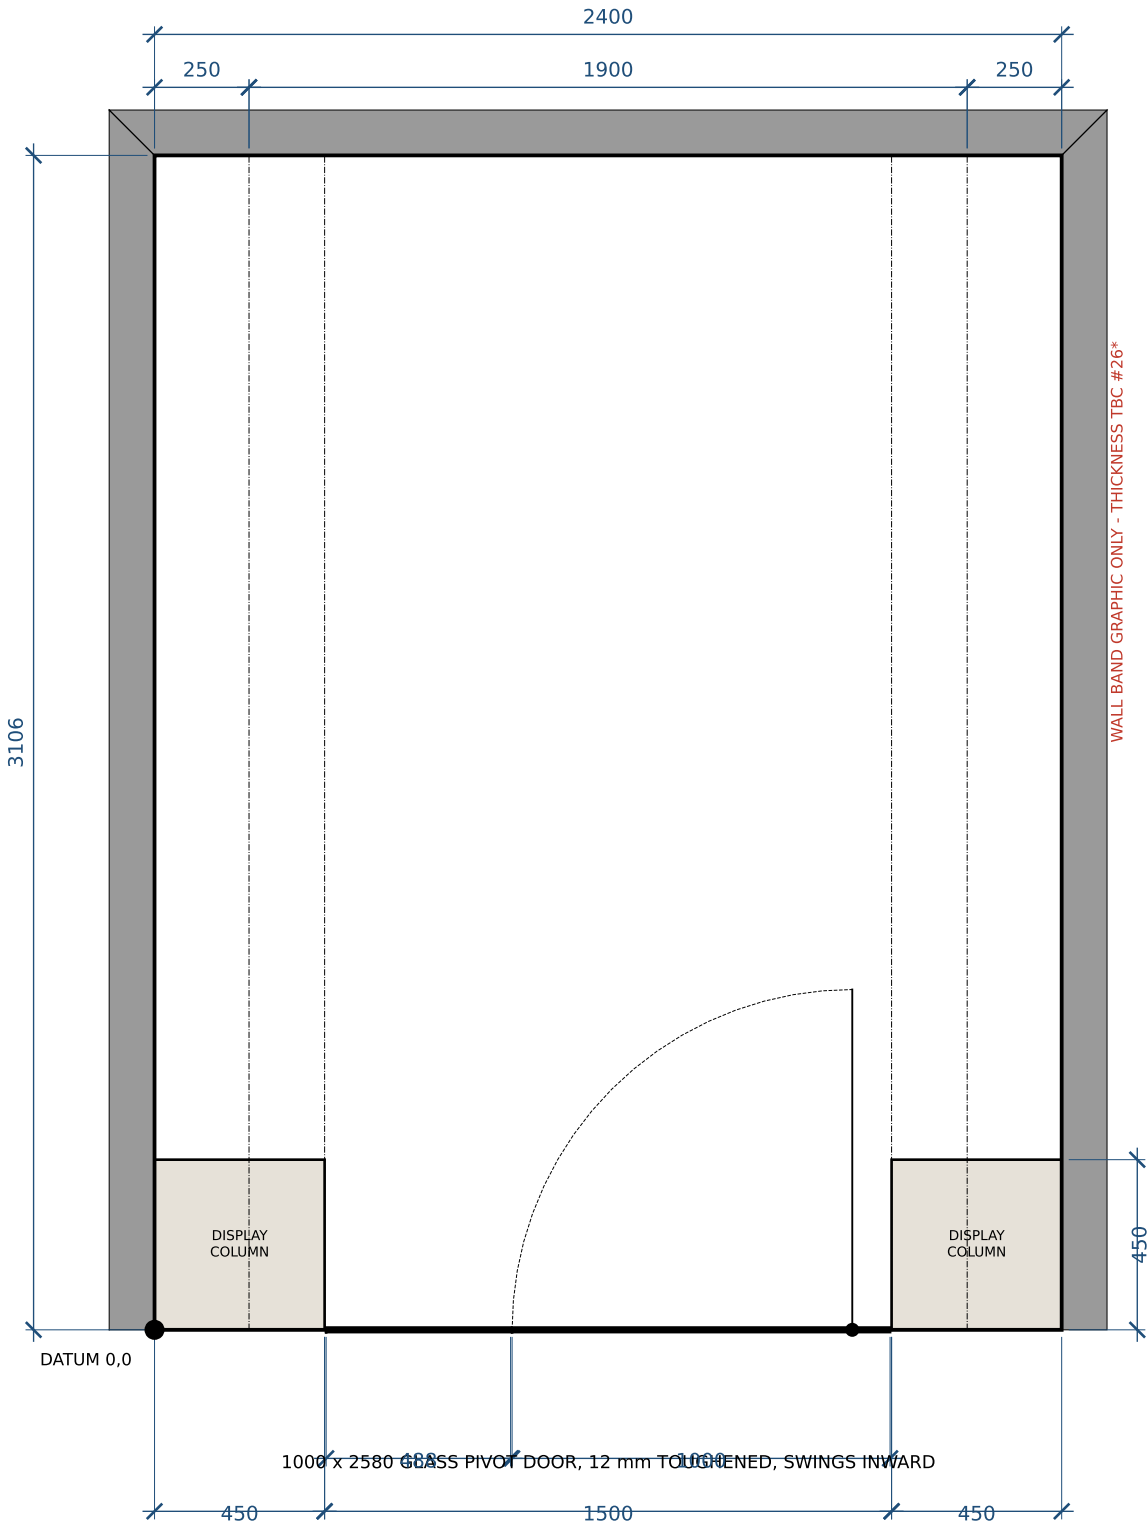

Site / consultant items still open: #4 finished size, #16 MEP/fire, #23 north, #26 datum + wall thickness. Verify before fabrication.

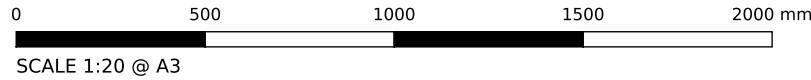

BORN FRAGRANCE

PROJECT BORN FRAGRANCE - shop fit-out

SHEET SD-01

TITLE SETTING-OUT PLAN

SCALE 1:20 @ A3

DATE 2026-10-05

REV A - owner-approved TBC answers

SPEC spec/SHOP_SPEC.json @ e1fbc1c

DRAWN Claude Code (AI), for owner review

TBC ITEMS ON THIS SHEET

- #4 Is 2400 x 3106 the finished size (after plaster)?
- #16 Fixings, MEP, fire and escape requirements
- #23* North direction
- #26* Vertical datum (FFL) and wall thickness / construction

* proposed item, not yet in spec/TBC.md
TBC items are shown in revision clouds.
Dimensions computed from SHOP_SPEC.json.
Do not scale from the render.

FOR COORDINATION - SITE ITEMS OPEN