



MATERIALS (LOCKED)

M1 Raw textured light plaster
M2 25x25x1.6 / 20x20x1.6 MS SHS, matte black PPC
M3 ~20x40 diamond expanded mesh, black
M4 1200x600 stone-look porcelain floor
L1 Concealed 3000 K LED under shelves
Heights not listed are TBC - never scaled.

BLACK HALO-LIT LOGO ON 25 mm STAND-OFFS

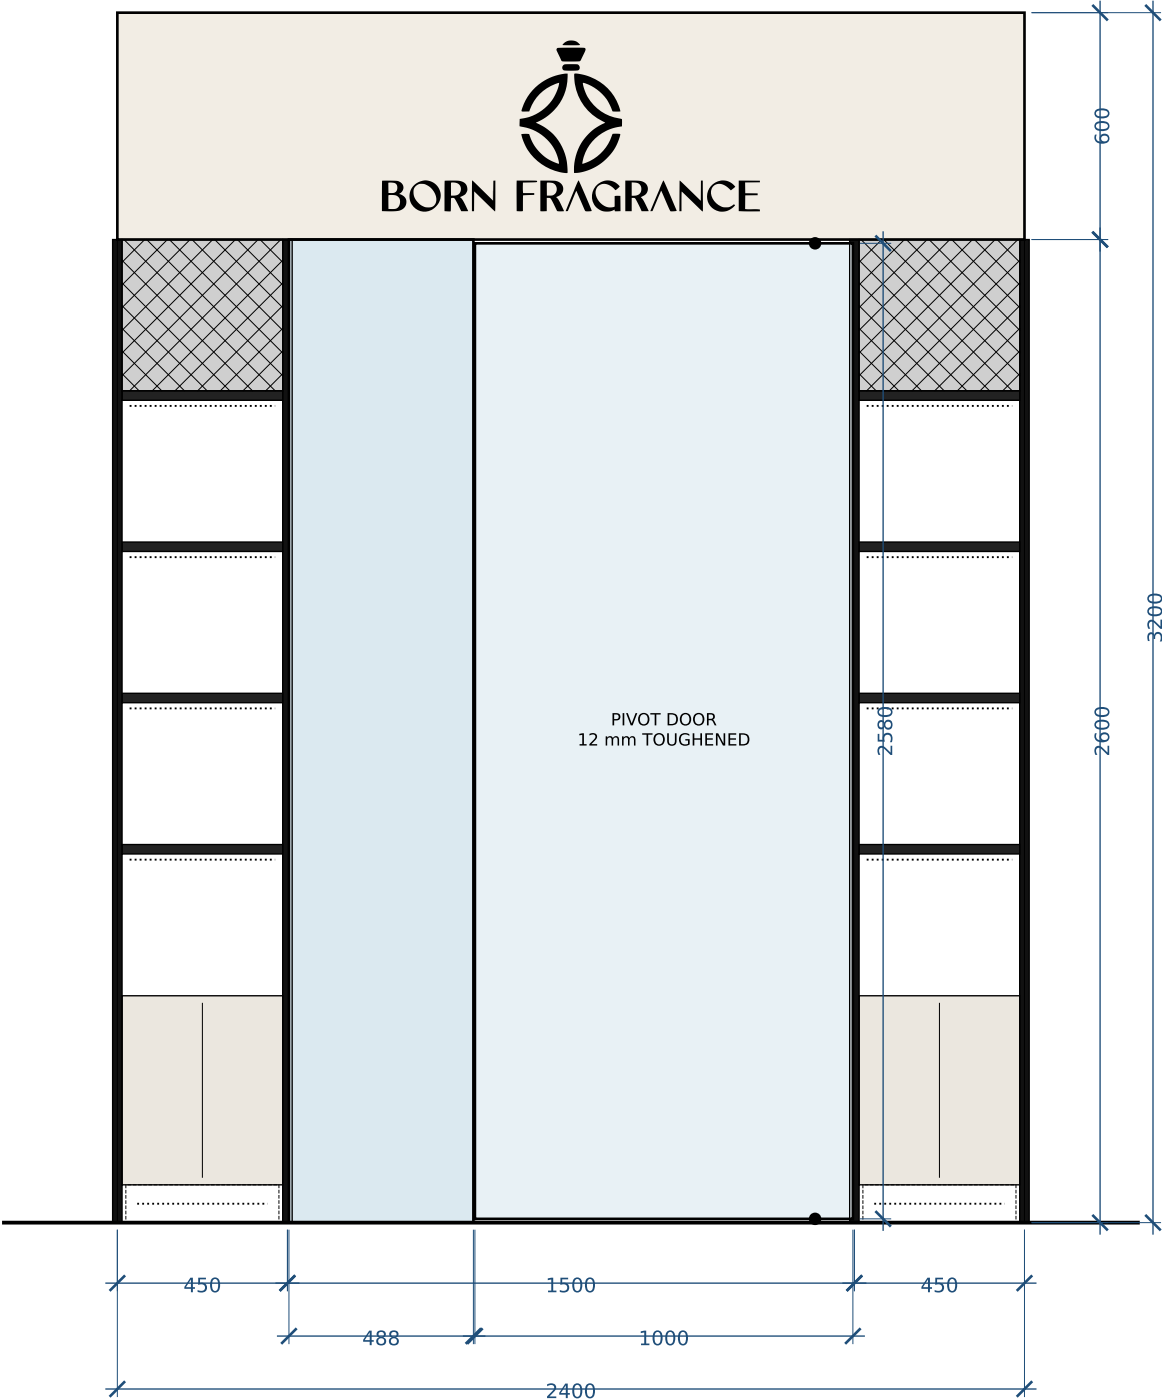

Site / consultant items still open: #4 finished size, #16 MEP/fire, #23 north, #26 datum + wall thickness. Verify before fabrication.

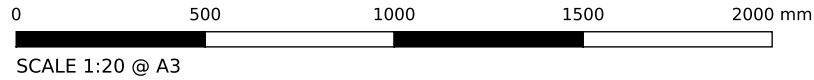

BORN FRAGRANCE

PROJECT BORN FRAGRANCE - shop fit-out

SHEET SD-05

TITLE STOREFRONT ELEVATION (EXTERNAL)

SCALE 1:20 @ A3

DATE 2026-10-05

REV A - owner-approved TBC answers

SPEC spec/SHOP_SPEC.json @ f6c03c6

DRAWN Claude Code (AI), for owner review

TBC ITEMS ON THIS SHEET

#4 Is 2400 x 3106 the finished size (after plaster)?
#16 Fixings, MEP, fire and escape requirements
#23* North direction
#26* Vertical datum (FFL) and wall thickness / construction
#16 Fixings, MEP, fire and escape requirements
* proposed item, not yet in spec/TBC.md
TBC items are shown in revision clouds.
Dimensions computed from SHOP_SPEC.json.
Do not scale from the render.
FOR COORDINATION - SITE ITEMS OPEN